WOHNRAUM, DER SICH *RECHNET*.

Die Richtlinie Mietwohnraum 2026 für Wohnungsunternehmen, Genossenschaften, Investorinnen und Investoren sowie Kommunen.



Referenzprojekt Brauerstraße, Rotenburg (Wümme)
19 barrierefreie Wohnungen · mit Förderung der NBank

PGN ARCHITEKTEN STADTPLANER INGENIEURE

Herausgeber
Planungsgemeinschaft Nord GmbH Rotenburg (Wümme)

Stand
11/2026

BIS ZU 80 %
Förderquote aus Darlehen und Zuschuss
der zuwendungsfähigen Kosten · Programmteil 2.1


1 AUSGANGSLAGE: *HERSTELLUNGSKOSTEN, ZINSEN, KAPITALDIENST, BESTAND*

Herstellungs- und Finanzierungskosten im Zeitverlauf und ihre Auswirkung auf den monatlichen Kapitaldienst je m² Wohnfläche. Bestand und Entwicklung der gebundenen Wohnungen in Niedersachsen.

HERSTELLUNGSKOSTEN SEIT 2020 UM *52,9 %* GESTIEGEN

Herstellungs- und Grundstückskosten je m² Wohnfläche


in €, Bruttokosten, deutsche Großstädte

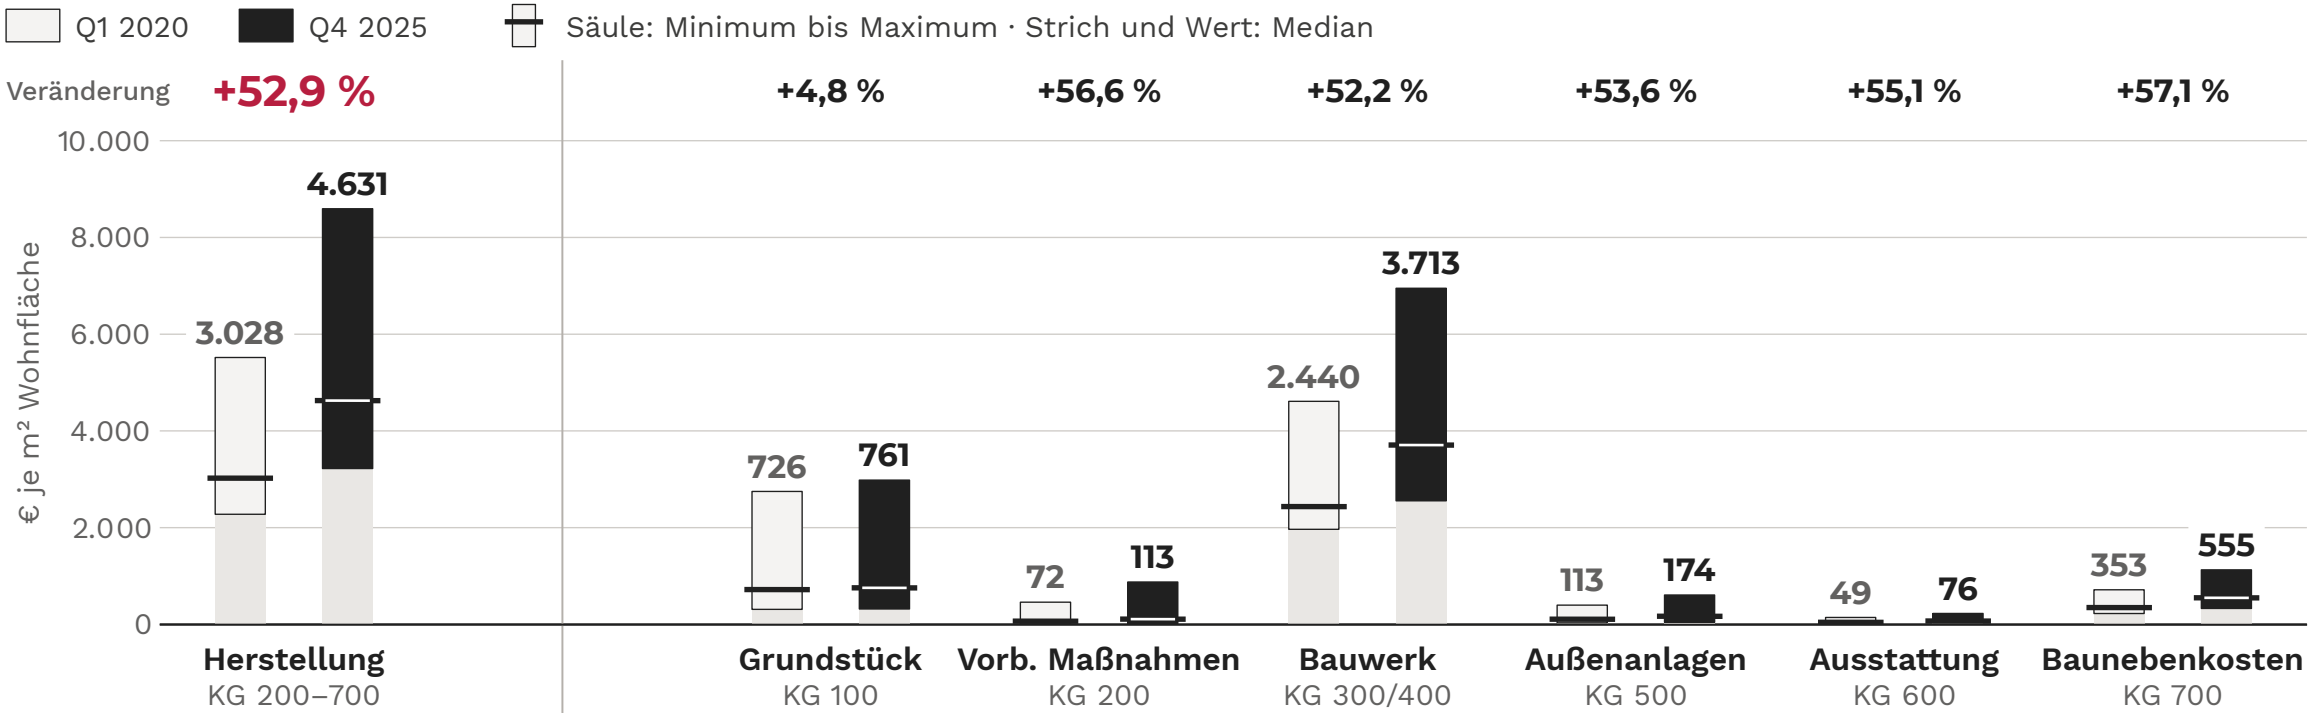

SOLLZINS BEI 10 JAHREN ZINSBINDUNG SEIT 2020 VON 0,46 AUF *3,86 %* GESTIEGEN

Sollzins p. a. nach Zinsbindung


in %, Monatswerte 01/2016 bis 11/2026, Top-Konditionen Wohnungswirtschaft

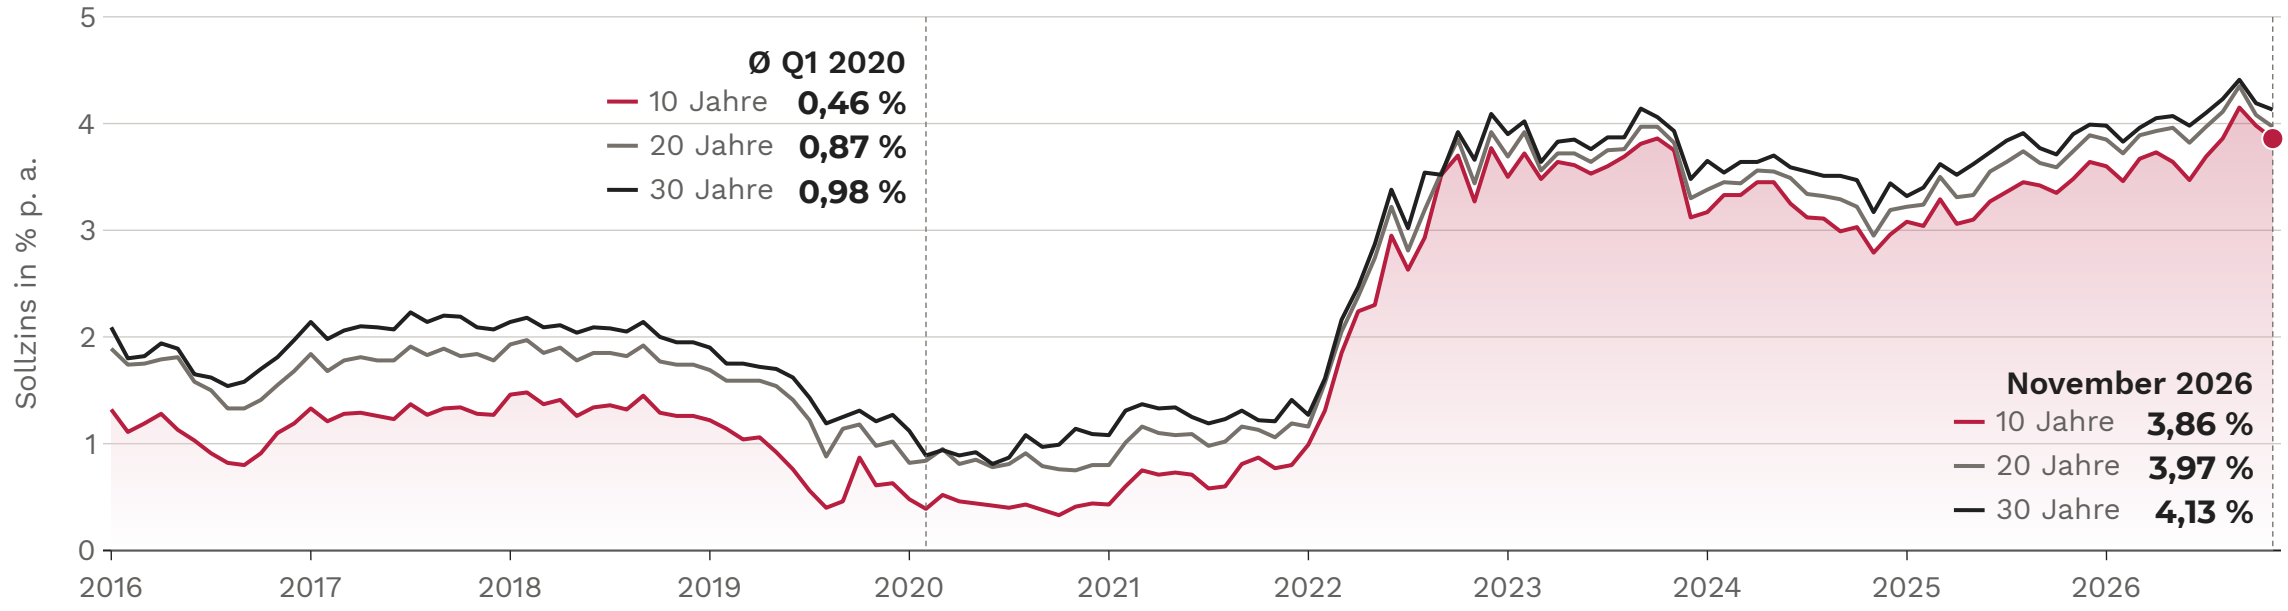

KAPITALDIENST JE m² UND MONAT SEIT 2020 VON 7,22 AUF *17,55 €* GESTIEGEN

Kapitaldienst je m² und Monat, frei finanziert

in €, ARGE-Median deutscher Großstädte, ohne Grundstück

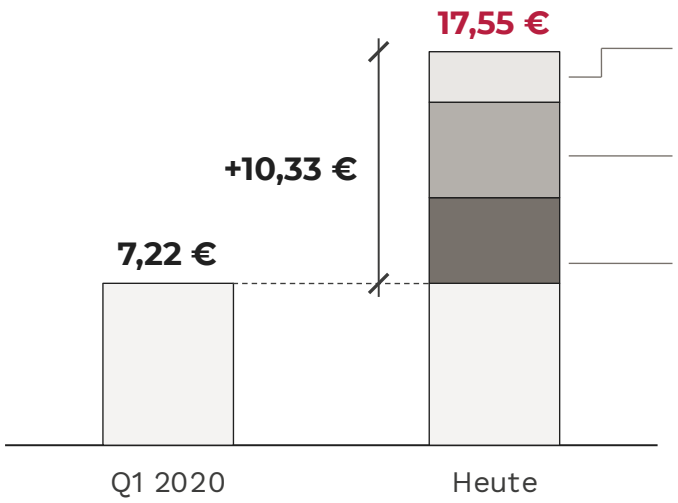

Wechselwirkung **+2,25 € · 22 %**
höherer Zins auf die höheren Kosten

Zins **+4,26 € · 41 %**
höherer Zins auf die Kosten von 2020

Herstellungskosten **+3,82 € · 37 %**
höhere Kosten zum Zins von 2020

ⓘ Kosten Q4 2025, Zins 11/2026

Rechenweg je m² Wohnfläche

jährliche Annuität über 30 Jahre

Kapitaldienst je m² und Monat
= Herstellungskosten × Fremdkapitalanteil
× Kapitaldienstsatz ÷ 12


	Q1 2020	HEUTE
Herstellungskosten je m²	**3.028 €**	**4.631 €**
× Fremdkapitalanteil	**80 %**	**80 %**
Sollzins p. a.	**0,46 %**	**3,86 %**
+ anfängliche Tilgung	**3,116 %**	**1,825 %**
= Kapitaldienstsatz	**3,576 %**	**5,685 %**
Kapitaldienst je m² und Monat	**7,22 €**	**17,55 €**

Quellen: ARGE e. V. (2026), S. 34; Dr. Klein Wowi Finanz AG (2026); eigene Rechnung; Methode in Anlehnung an GdW (2026), Kapitaldienst-Methode

BESTAND GEBUNDENER WOHNUNGEN SEIT 2016 UM *40,6 %* GESUNKEN

Bestand gebundener Mietwohnungen in Niedersachsen

Wohnungen mit Belegungs- und Mietbindung, Bestand zum 31.12.

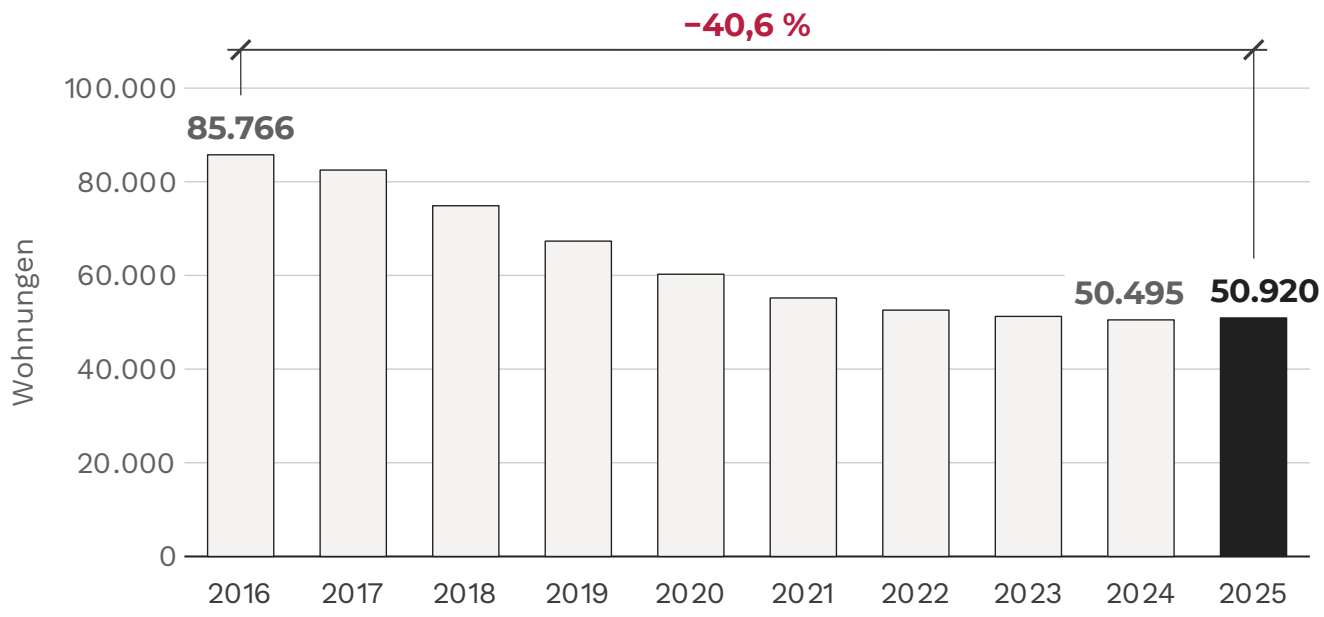

2015 BIS 2024

28 %

ausgelaufener Bindungen ersetzt

58.024 Bindungen ausgelaufen, rund 16.000 Wohnungen neu gefördert.

Quellen: BT-Drs. 21/7303, Antwort der Bundesregierung vom 21.07.2026; NBank-Wohnungsmarktbericht 2025

THEMA IST *PROGRAMMTEIL 2.1*: NEUBAU MIT DARLEHEN UND ZUSCHUSS

1 Ausgangslage
Herstellungskosten, Zinsen, Kapitaldienst, Bestand

2 Programmteil 2.1
Neuerungen, Höchstmiete, Fördersätze, Eckdaten

3 Modellrechnung
14 Wohnungen, gefördert und frei finanziert

4 Umsetzung
Antragsweg und Planung mit PGN

Die sechs Programmteile der Richtlinie

Die Programmteile 2.2 bis 2.6 stehen in der Broschüre und im Anhang A1.

2.1	2.2	2.3	2.4	2.5	2.6
Neubau, Änderung und Erweiterung, Ersterwerb	**Energetisch hochwertiger Neubau**	**Klimagerechte Modernisierung**	**Ostfriesische Inseln**	**Belegungsbindungen erwerben**	**Auslaufende Bindungen verlängern**
in diesem Vortrag	Broschüre S. 12	Broschüre S. 14	Broschüre S. 13	Broschüre S. 15	Broschüre S. 15

2 PROGRAMMTEIL 2.1: *NEUERUNGEN, HÖCHSTMIETE, FÖRDERSÄTZE, ECKDATEN*

Änderungen gegenüber den Förderkonditionen 2024.
Höchstmieten nach Einkommensgruppe, Fördersätze für Darlehen und Zuschuss, Eckdaten des Darlehens.

ZUSCHUSS VON BIS ZU 40 % ERSETZT SEIT 01.07.2026 DEN TILGUNGSNACHLASS


Programmteil 2.1 im Vergleich

MERKMAL	BIS 30.06.2026	SEIT 01.07.2026	WIRKUNG
Förderquote	Darlehen bis 75 % der Gesamtkosten	Darlehen und Zuschuss bis 80 % der zuwendungsfähigen Kosten	+5 Prozentpunkte
Nicht rückzahlbar	Tilgungsnachlass 30 % des Darlehens, nur bei geringen Einkommen	Zuschuss bis 40 % (A), 20 % (B), 10 % (C) der Kosten	A: von 22,5 auf 40 % der Kosten. B und C: neu
Eigenmittel	25 % der Gesamtkosten	20 % der zuwendungsfähigen Kosten	–5 Prozentpunkte. Geld oder Grundstück weiter mindestens 10 %
Bemessungsgrenze je m², Mietenstufe I–III / IV–VII	5.330 / 5.550 €, Gesamtkosten mit Grundstück	5.250 / 5.460 € (Stand 01.10.2026), nur Herstellungskosten. Grundstück zusätzlich bis zum Bodenrichtwert	Das Grundstück zählt nicht mehr auf die Grenze
Höchstmiete Jahr 1 bis 3 je m², Mietenstufe I–III / IV–VII	6,30 / 6,60 € (geringe Einkommen)	6,50 / 6,80 € (Gruppe A)	+0,20 €

HÖCHSTMIETE VON 6,50 BIS 9,00 € JE m², *DREI JAHRE FEST*

Höchstmiete nettokalt, Jahre 1–3

€ je m² und Monat · nach Einkommensgruppe und Mietenstufe

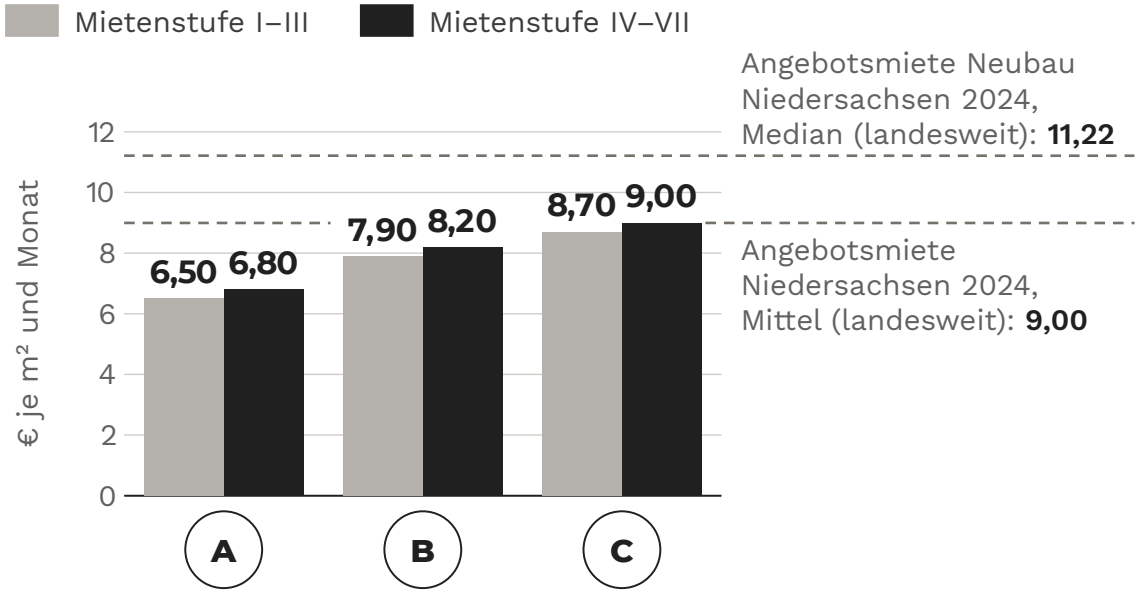

ⓘ Ab Effizienzhaus-40-Niveau bis zu +0,30 €.

Mietentwicklung

Gruppe A · Mietenstufe IV–VII

Jahre 1–3		**6,80 €**
ab Jahr 4	höchstens	**7,21 €**
ab Jahr 7	höchstens	**7,66 €**

Zulässige Mieterhöhung

- ab Jahr 4 höchstens +6,15 % in drei Jahren (Betriebskosten ausgenommen)
- auch bei Wiedervermietung
- keine Staffel- oder Indexmiete


Gruppen

- A bis Einkommensgrenze, B bis +40 %, C bis +60 %
- B und C nur mit Zulassung

IN JEDER EINKOMMENSGRUPPE BIS ZU *80 %* FÖRDERQUOTE

Fördersätze je Einkommensgruppe

Höchstsätze in % der zuwendungsfähigen Kosten

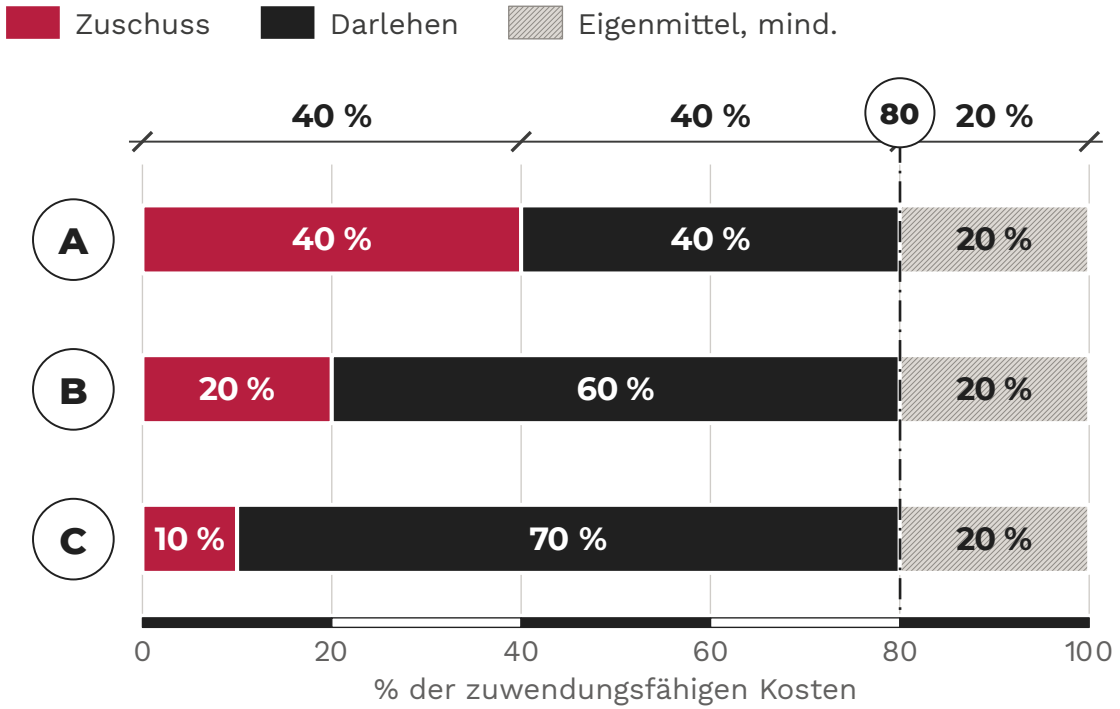

Zuschuss

- nicht rückzahlbar
- nur zusammen mit dem Darlehen

Eigenmittel


- mindestens 20 % der zuwendungsfähigen Kosten
- davon soll mindestens die Hälfte Geld oder lastenfreies Grundstück sein

Bemessungsgrenze

- Obergrenze der zuwendungsfähigen Herstellungskosten je m² Wohnfläche
- seit 01.10.2026: 5.250 € in Mietenstufe I–III, 5.460 € in IV–VII
- Fortschreibung zum 01.04. und 01.10., aktueller Wert auf nbank.de

35 JAHRE ZINSFREI UND GEBUNDEN, HÖCHSTENS 42 JAHRE LAUFZEIT

Darlehen und Bindung im Zeitverlauf

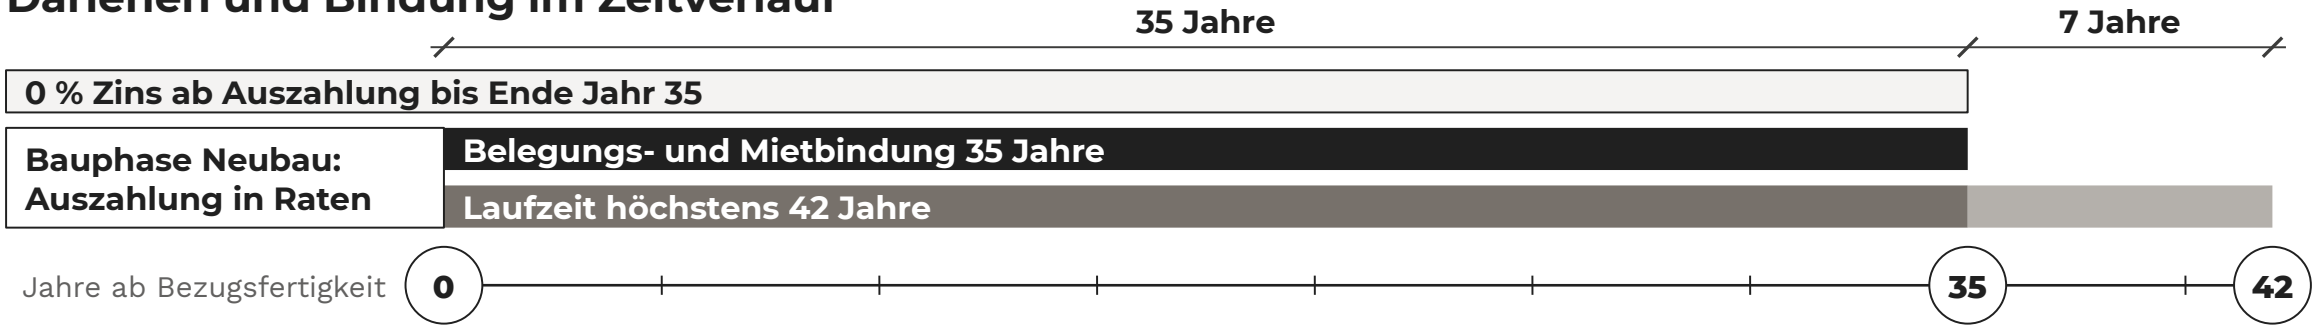

ⓘ Ab Jahr 36: Zins bis zu 3 Prozentpunkte über dem Basiszinssatz (§ 247 BGB), höchstens marktüblich.

0,5 % p. a.

Verwaltungskostenbeitrag

auf das Restkapital, ab Auszahlungsbeginn

1 % / 0,75 %

Bearbeitungsentgelt, einmalig

des Darlehens / des Zuschusses

mind. 2,38 % p. a.

Tilgung

Rechnerisch bei 42 Jahren Laufzeit. Den Satz legt die NBank fest.

3 MODELLRECHNUNG: *14 WOHNUNGEN, GEFÖRDERT UND FREI FINANZIERT*

Modellhaus: PGN-Projekt in Neu Wulmstorf mit 828 m² Wohnfläche. Vergleich der Förderung nach Programmteil 2.1 mit der freien Finanzierung.

14 WOHNUNGEN FÜR 3,0 MIO. €, DAVON BIS ZU *2,4 MIO. €* FÖRDERUNG

PGN-Projekt in Neu Wulmstorf · 14 Wohnungen · 828 m² Wohnfläche · Gruppe A · Mietenstufe VI

Finanzierung 3,0 Mio. €, Höchstsätze



Rechenweg, in €

1		Herstellungskosten, 828 m² × 3.579 €	**2.963.412**
		Bemessungsgrenze 5.460 € je m²: eingehalten Grundstück im Bestand, nicht angesetzt	
2	=	**zuwendungsfähige Kosten**	**2.963.412**
3		Eigenmittel, mindestens 20 %	**592.682**

ⓘ Von den Eigenmitteln sollen mindestens 296.341 € Geld oder lastenfreies Grundstück sein. In dieser Rechnung sind die Eigenmittel ganz Geld, weil das Grundstück nicht angesetzt ist.

BIS ZU

84.669 €

Ø Zuschuss je Wohnung

plus Darlehen in gleicher Höhe

MIND.

42.334 €

Ø Eigenmittel je Wohnung

20 % von 211.672 € je Wohnung

ALLE DREI GRUPPEN TRAGEN SICH AB JAHR 1, IN A BLEIBEN *15.003 €* ZAHLUNGSÜBERSCHUSS

Jahresrechnung Jahr 1, in € p. a.

Höchstmiete nettokalt, Mietenstufe VI: 6,80 | 8,20 | 9,00 € je m² und Monat (A | B | C)

		POSITION	A	B	C
1		Sollmiete zur Höchstmiete	**67.565**	**81.475**	**89.424**
2	–	Mietausfall/Leerstand, 2 %	**1.351**	**1.630**	**1.788**
3	–	Objektverwaltung, 367 € je Wohnung	**5.138**	**5.138**	**5.138**
4	–	Instandhaltung, 14,40 € je m²	**11.923**	**11.923**	**11.923**
5	=	**Überschuss vor Kapitaldienst**	**49.152**	**62.784**	**70.574**
6	–	Verwaltungskostenbeitrag, 0,5 %	**5.927**	**8.890**	**10.372**
7	–	Zins NBank-Darlehen, 0 %	**0**	**0**	**0**
8	–	Tilgung 2,38 % p. a. (Annahme)	**28.223**	**42.334**	**49.390**
9	**=**	**Zahlungsüberschuss p. a.**	**15.003**	**11.560**	**10.812**

ⓘ Einmalig, außerhalb der Jahresrechnung: Bearbeitungsentgelte 20.744 | 22.226 | 22.966 €


Annahmen

- Jahr 1, Kostenstand 2026, vor Steuern
- Tilgung gleichmäßig über 42 Jahre auf 1,2 | 1,8 | 2,1 Mio. € Darlehen
- B und C nur mit Zulassung in der Förderentscheidung

34.150 € KAPITALDIENST IN JAHR 1 STATT 134.779 € FREI FINANZIERT

Kapitaldienst in Jahr 1

in € p. a. · gleiches Haus, gefördert und frei finanziert

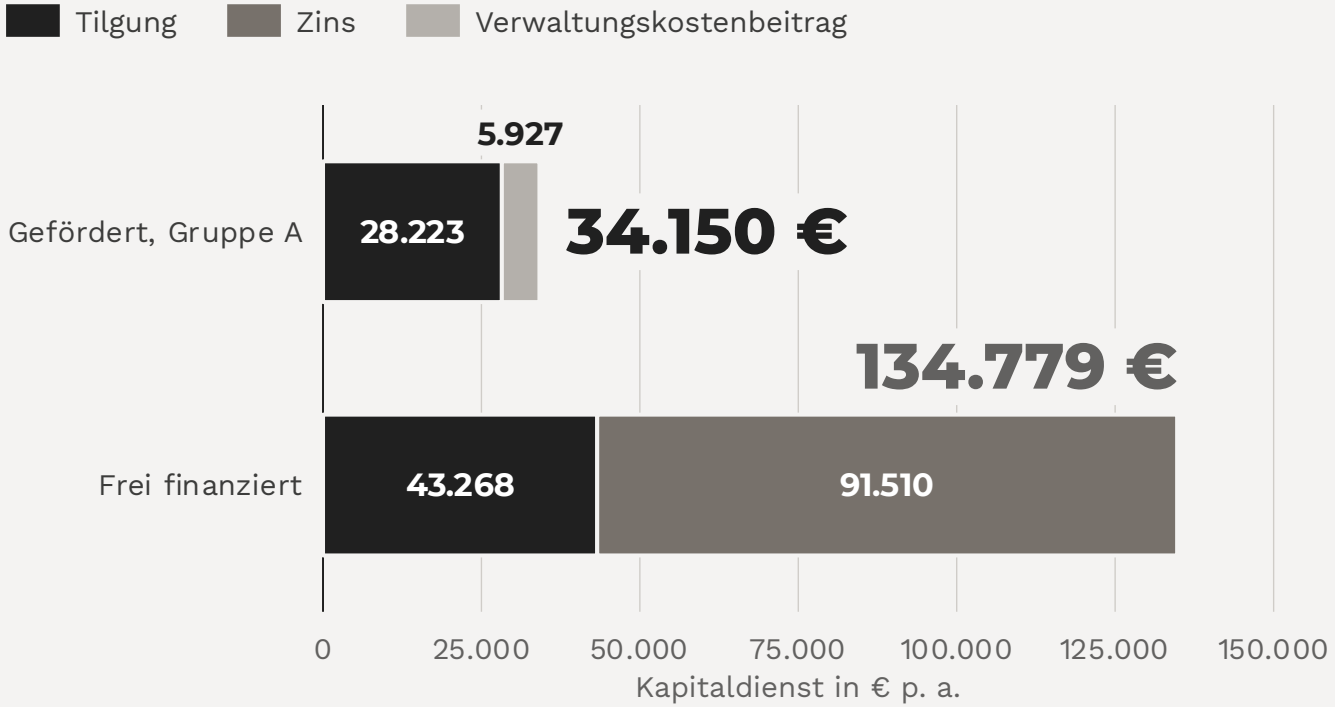


Annahmen

- Frei finanziert: gleiches Haus, Eigenmittel 0,6 Mio. €, Bankdarlehen 2,4 Mio. € zu 3,86 % Zins, jährliche Annuität über 30 Jahre
- Objektverwaltung und Instandhaltung wie gefördert
- Gefördert: Zuschuss 1,2 Mio. €, Darlehen 1,2 Mio. € zu 0 % Zins, Tilgung 2,38 % p. a.

GEFÖRDERT FLIESSEN 0 % DER MIETE IN DEN ZINS, *41,8 %* IN DIE TILGUNG

Zahlungsfluss in Jahr 1, gefördert


in € p. a. und in % der Sollmiete · Modellhaus, Gruppe A · gleicher Maßstab wie frei finanziert

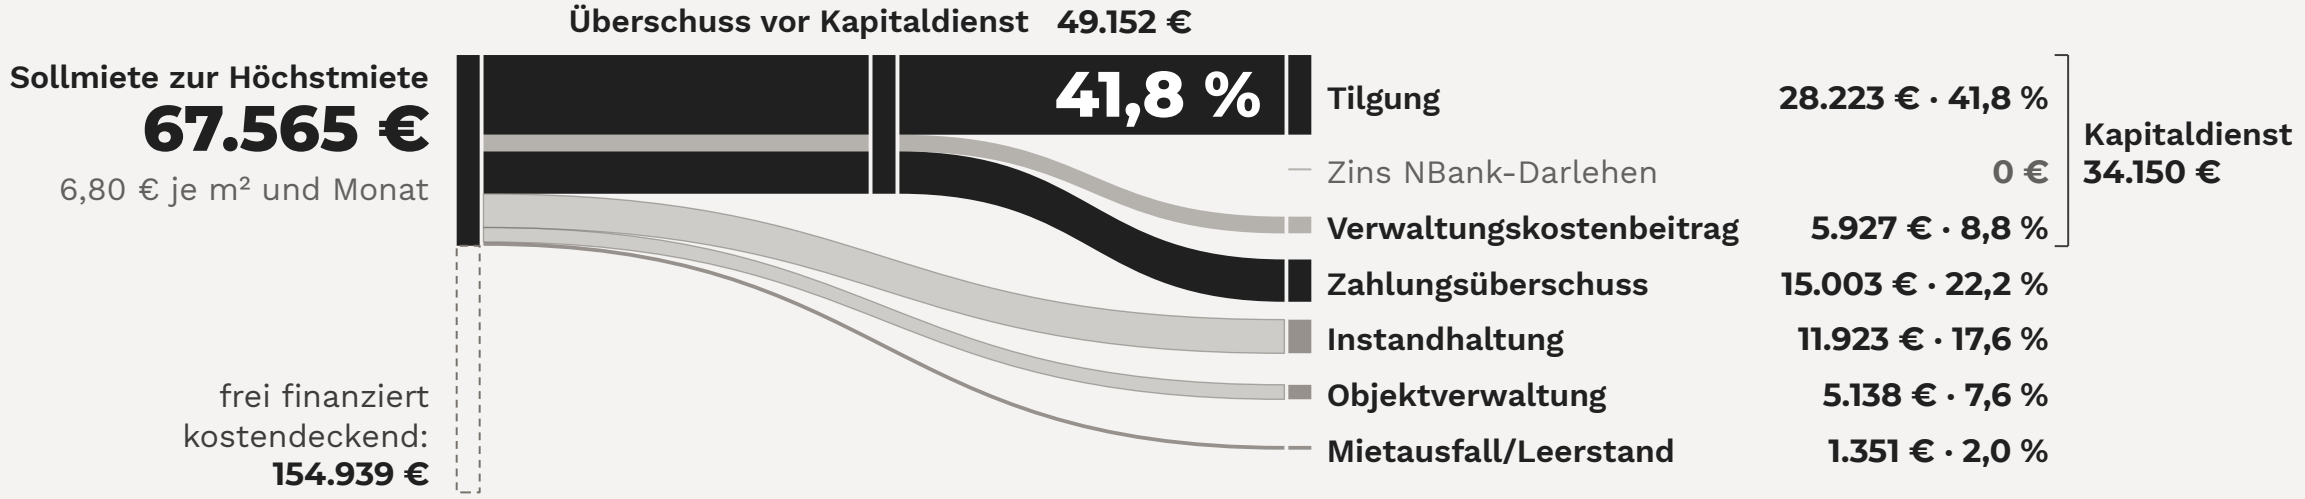

FREI FINANZIERT FLIESSEN *59,1 %* DER MIETE IN DEN ZINS, 27,9 % IN DIE TILGUNG

Zahlungsfluss in Jahr 1, frei finanziert


in € p. a. und in % der Sollmiete · Miete, bei der der Zahlungsüberschuss null ist · gleicher Maßstab wie gefördert

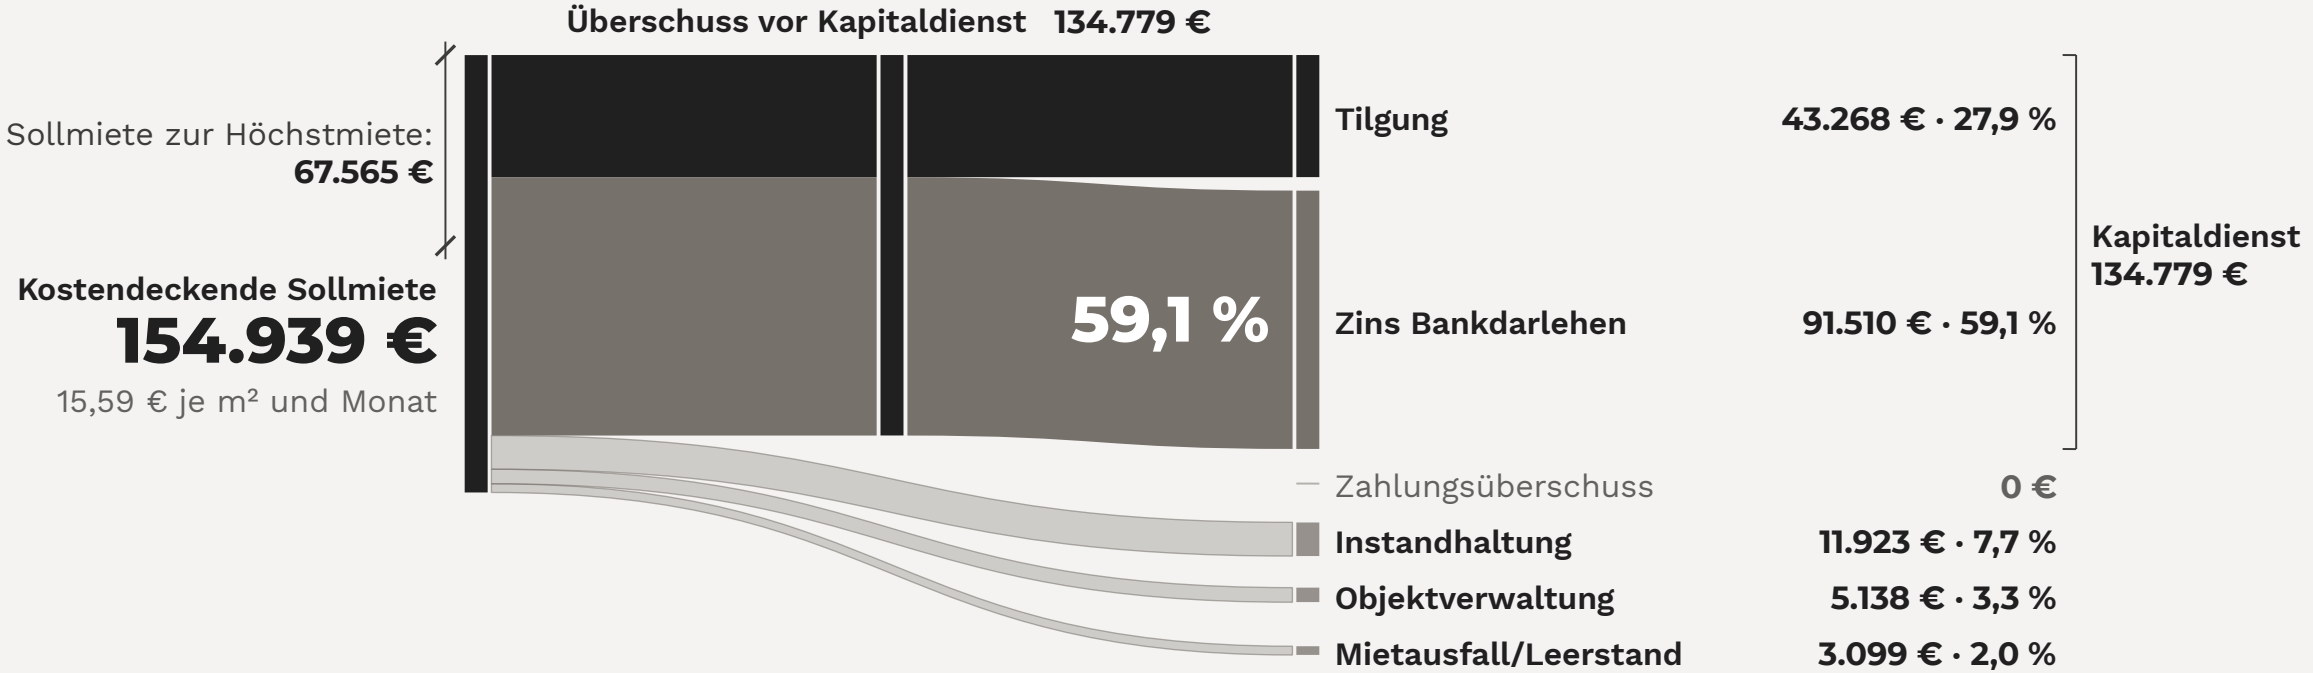

KOSTENDECKENDE ANFANGSMIETE: 5,26 € JE m² GEFÖRDERT, 15,59 € FREI FINANZIERT

Kostendeckende Anfangsmiete in Jahr 1

Miete je m² und Monat,
bei der der Zahlungsüberschuss null ist

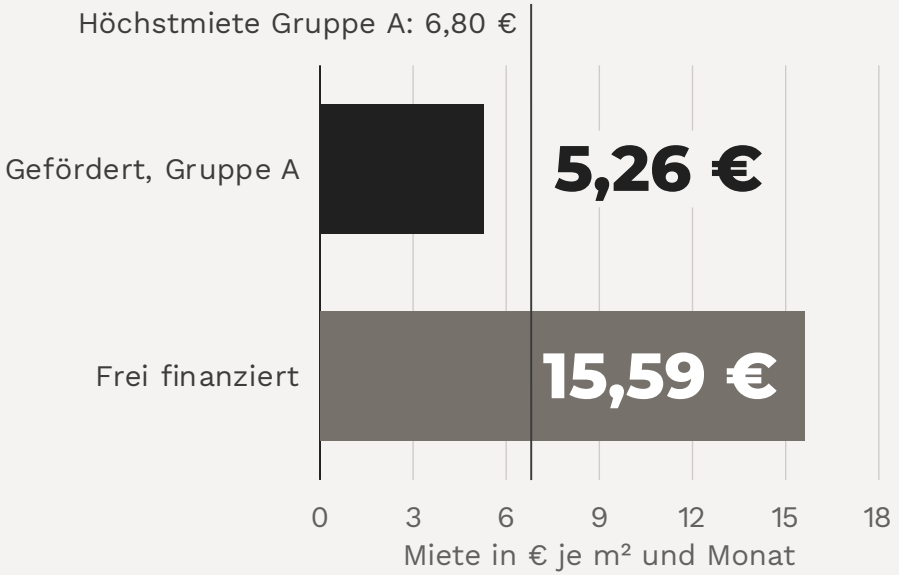

Rechenweg


Frei finanziert: 3,86 % Zins, jährliche Annuität über 30 Jahre

JAHR 1	GEFÖRDERT (A)	FREI FINANZIERT
Kapitaldienst p. a.	**34.150 €**	**134.779 €**
+ Bewirtschaftung	**17.061 €**	**17.061 €**
+ Mietausfall, 2 %	**1.045 €**	**3.099 €**
= kostendeckende Sollmiete p. a.	**52.256 €**	**154.939 €**
÷ 828 m² ÷ 12 Monate	**5,26 €**	**15,59 €**

BIS *2,90 %* TILGUNG BLEIBT IN ALLEN DREI GRUPPEN EIN ZAHLUNGSÜBERSCHUSS

Zahlungsüberschuss je Tilgungssatz

Jahr 1, in € p. a. · Tilgungssatz p. a. auf das NBank-Darlehen

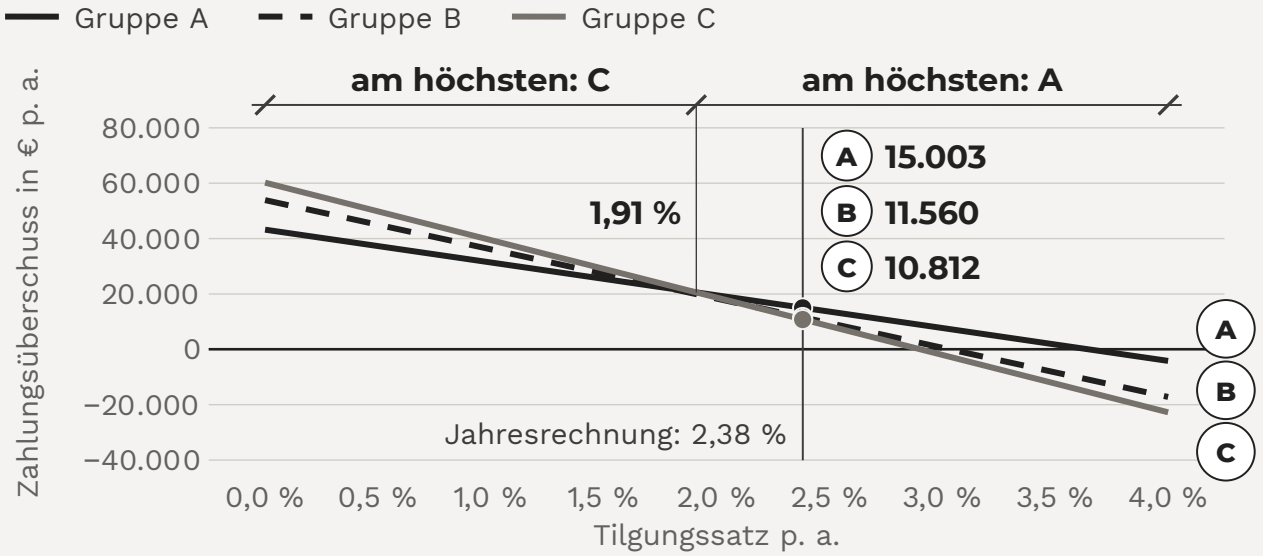

ⓘ Gilt für Herstellungskosten von 3.579 € je m². Bei höheren Kosten liegen die Schwellen niedriger, siehe Folie 23.

Ergebnis

- bei 2,38 % Tilgung Zahlungsüberschuss in allen drei Gruppen, am höchsten in A
- Zahlungsüberschuss null bei 2,90 % in C, 3,03 % in B, 3,65 % in A
- unter 1,91 % Tilgung hat C den höchsten Zahlungsüberschuss, darüber A
- B hat bei keinem Tilgungssatz den höchsten


Tilgungssatz

- legt die NBank fest
- rechnerisch mindestens 2,38 %, linear über 42 Jahre

BEI VOLLER MIETANPASSUNG WÄCHST DER ZAHLUNGSÜBERSCHUSS IN A AUF *64.860 €*

Zahlungsüberschuss je Jahr, Jahr 1 bis 35

in € p. a., nach Kapitaldienst, vor Steuern, nicht kumuliert

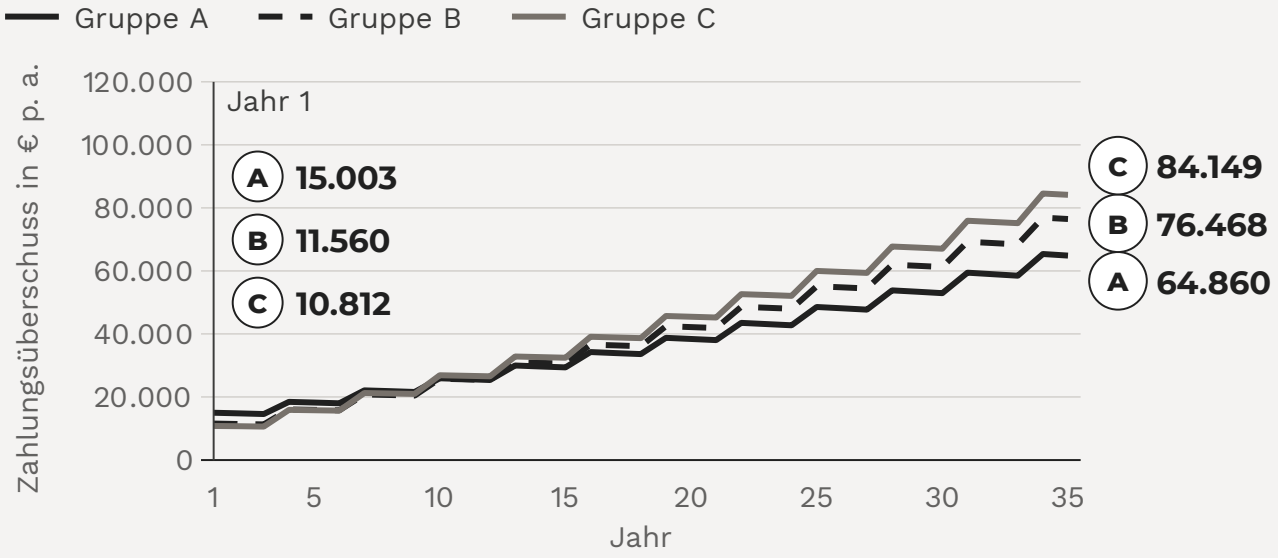

ⓘ Ohne jede Mieterhöhung bleibt in allen drei Gruppen bis Jahr 35 in jedem Jahr ein Zahlungsüberschuss.

Annahmen

- Tilgung 2,38 % p. a.
- Miete alle drei Jahre +6,15 %: Höchstwert, bester Fall
- Objektverwaltung und Instandhaltung ab Jahr 2 +2 % p. a.


Ergebnis

- kein Jahr mit Fehlbetrag
- Jahr 1: A hat den höchsten Zahlungsüberschuss
- Jahr 35: C hat den höchsten Zahlungsüberschuss

HERSTELLUNGSKOSTEN DER PGN LIEGEN *22,7 % UNTER* DEM ARGE-MEDIAN

Herstellungs- und Grundstückskosten je m² Wohnfläche, PGN und ARGE

in €, Bruttokosten, Kostenstand Q4 2025

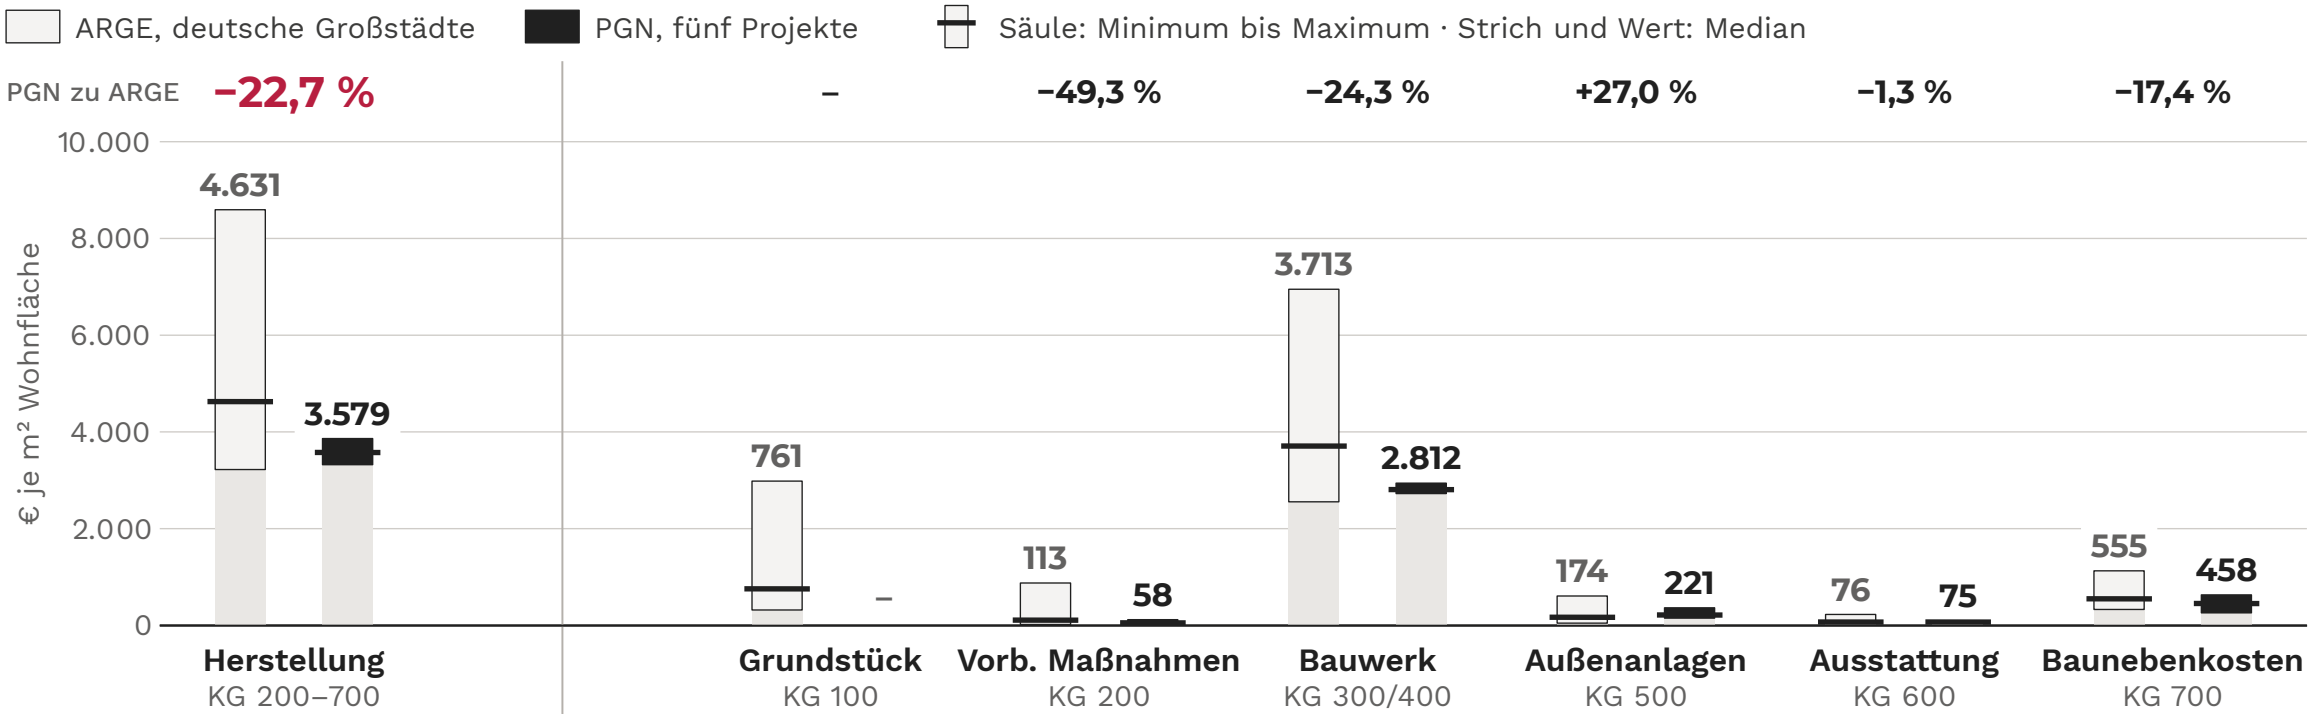


Quellen: ARGE e. V. (2026), Wohnungsbau in Deutschland 2026, S. 32; PGN, fünf Projekte

BIS RUND *5.150 €* JE m² TRÄGT SICH GRUPPE A, IM MODELLHAUS BLEIBEN 15.003 €

Zahlungsüberschuss Jahr 1, Gruppe A

in € p. a. · nach Herstellungskosten je m² Wohnfläche

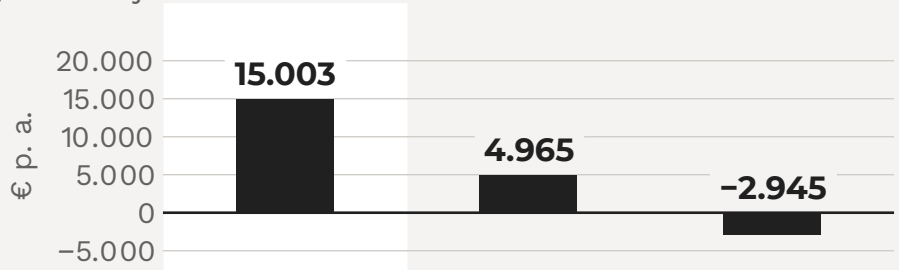

	JE m² WOHNFLÄCHE	Modellhaus 3.579 €	ARGE-Median 4.631 €	Bemessungs-grenze 5.460 €
1	Gesamtkosten	**2,96 Mio. €**	**3,83 Mio. €**	**4,52 Mio. €**
2	Förderung, 80 % der Kosten	**2,37 Mio. €**	**3,07 Mio. €**	**3,62 Mio. €**
3	Kostendeckende Anfangsmiete je m², Gruppe A	**5,26 €**	**6,29 €**	**7,10 €**
4	Zahlungsüberschuss in B	**11.560 €**	**−3.497 €**	**−15.362 €**
5	Zahlungsüberschuss in C	**10.812 €**	**−6.754 €**	**−20.597 €**

Ergebnis

- je 100 € je m² mehr sinkt der Zahlungsüberschuss in A um 954 €
- A hat einen Zahlungsüberschuss bis rund 5.150 € je m²
- B bis rund 4.380 € je m², C bis rund 4.220 € je m²

Annahme

- nur die Herstellungskosten sind geändert

SO *RECHNET SICH* GEFÖRDERTER MIETWOHNRAUM

1 Förderung → 2 Kapitaldienst → 3 Miete

80 % der Herstellungskosten.
2,4 Mio. €, davon 1,2 Mio. € Zuschuss.
Darlehen 35 Jahre zinsfrei.

34.150 € p. a. in Jahr 1.
Frei finanziert: 134.779 €.

5,26 € je m², kostendeckend.
Höchstmiete: 6,80 €.
Frei finanziert: 15,59 €.

15.003 € Zahlungsüberschuss in Jahr 1, kein Jahr mit Fehlbetrag

Herstellungskosten

bis rund 5.150 € je m². Modellhaus: 3.579 €.

Tilgungssatz

bis 3,65 % p. a. Annahme: 2,38 %.
Den Satz legt die NBank fest.

Alle Zahlen gelten für das Modellhaus in Gruppe A und stehen auf den Folien davor.

4 UMSETZUNG: *ANTRAGSWEG UND PLANUNG MIT PGN*

Antragsweg vom Vorgespräch bis zum Verwendungsnachweis.
Planungsleistungen der PGN vor und nach der Bewilligung.

ERST DIE BEWILLIGUNG, DANN *VERTRÄGE UND BAUBEGINN*

1 Vorgespräch
Wohnraumförderstelle mit Ihnen
Nachweise und Unterlagen vorab klären

2 Antrag
Sie
bei der Wohnraumförderstelle am Bauort

3 Stellungnahme
Wohnraumförderstelle
Bedarfsbestätigung, Weiterleitung an die NBank

4 Förderentscheidung
NBank
Fördervertrag.
Bearbeitungszeit der NBank: Ziel höchstens drei Monate

±0 BEWILLIGUNG Vor der Bewilligung begonnene Vorhaben werden nicht gefördert.

5 Bauausführung
Sie
Baubeginn spätestens vier Monate nach Bekanntgabe der Förderentscheidung

6 Auszahlung
NBank
in Raten nach Baufortschritt


7 Fertigstellung
Wohnraumförderstelle mit Ihnen
Fertigstellung anzeigen
Vermietung nur mit Wohnberechtigungsschein

8 Verwendungsnachweis
Sie
innerhalb von sechs Monaten nach Erfüllung des Förderzwecks

ⓘ Als Vorhabenbeginn gilt ein Werk-, Liefer-, Leistungs- oder Kaufvertrag (außer für das Baugrundstück) oder der erste Spatenstich.

PLANUNG BIS LEISTUNGSPHASE 6 IST *VOR DER BEWILLIGUNG* MÖGLICH

Leistungen der PGN nach Leistungsphasen 1 bis 9 der HOAI

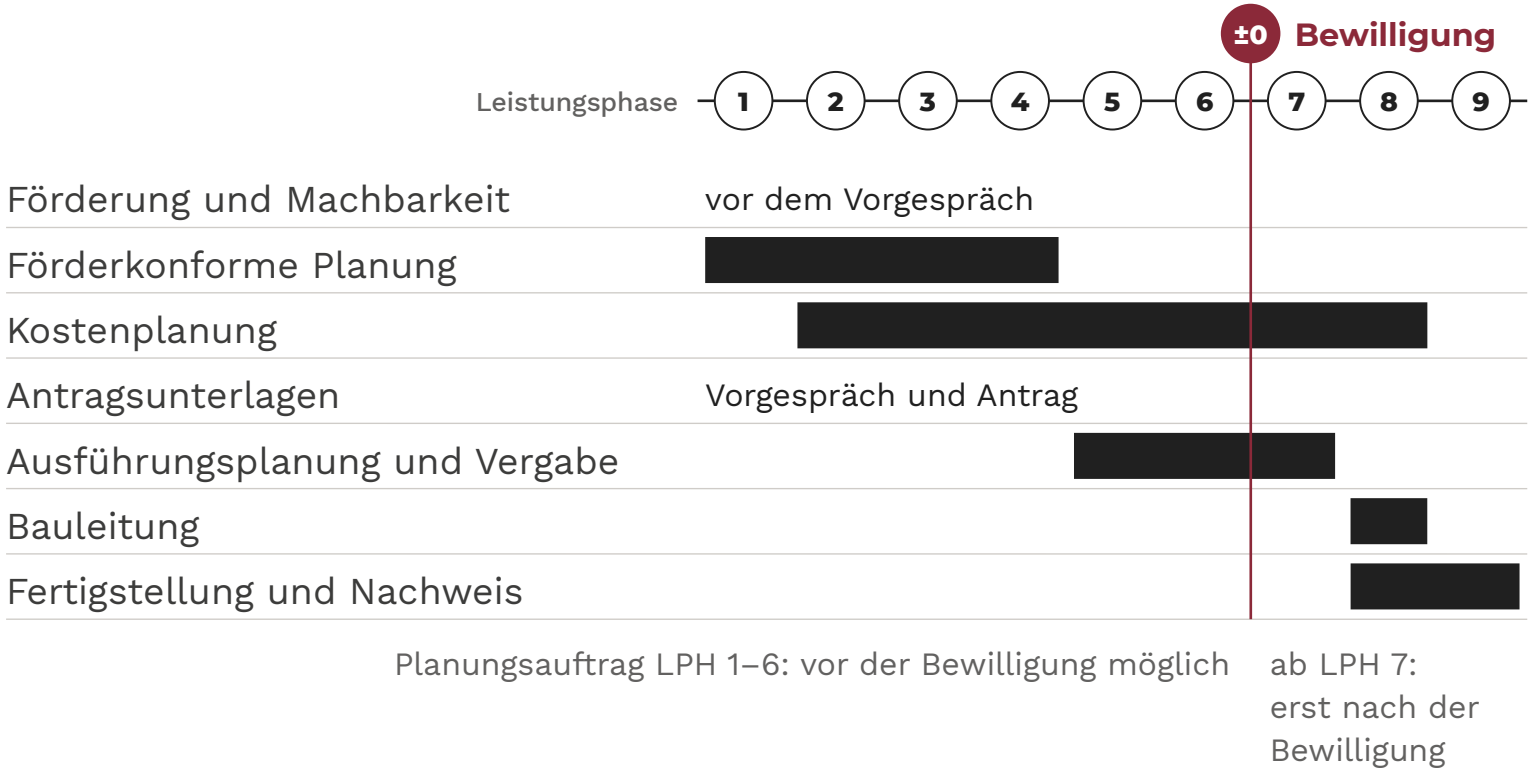



Visualisierung

Brauerstraße, Rotenburg (Wümme)
19 barrierefreie Wohnungen

MIT FÖRDERUNG DER NBANK


Erster Schritt: Förderung und Machbarkeit

- Programmteil, Standort und Mieterkreis klären
- Flächen und Kosten ermitteln
- Grundlage für Ihre Wirtschaftlichkeitsberechnung

AUS IHRER GUTEN IDEE

MACHEN WIR DEN *BESTEN PLAN.*

Wir planen Ihr Vorhaben im geförderten Mietwohnungsbau, in allen Leistungsphasen. Sprechen Sie uns an.

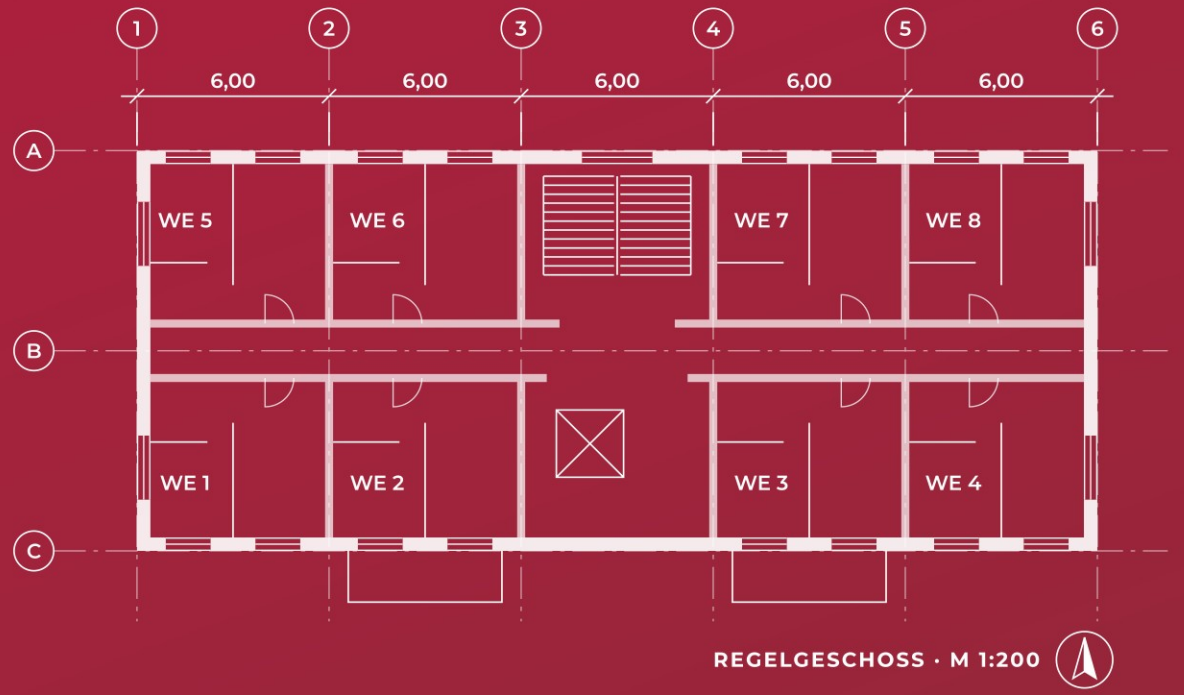

REGELGESCHOSS · M 1:200

PGN ARCHITEKTEN STADTPLANER INGENIEURE

PLANUNGSGEMEINSCHAFT NORD GMBH
Große Straße 49 · 27356 Rotenburg (Wümme)

Telefon
(+49) 4261 9293-0

E-Mail
info@pgn-architekten.de

Web
www.pgn-architekten.de

A ANHANG

Programmteile · Voraussetzungen und Verträge
Mieterkreis und Eckdaten · Rendite und Tilgungsschwelle
Quellen und Hinweis

PROGRAMMTEIL NACH VORHABEN

Die sechs Programmteile

Höchstsätze · B und C nur mit Zulassung

Neu schaffen oder erstmals erwerben: 2.1, 2.2, 2.4 · **Bestand modernisieren:** 2.3 · **Bestandswohnung binden:** 2.5 · **Bindung verlängern:** 2.6

	PROGRAMMTEIL	INSTRUMENT	BIS ZU	BINDUNG	EIGENMITTEL
2.1	**Neubau, Änderung und Erweiterung, Ersterwerb**	Darlehen + Zuschuss (Zuschuss nur mit Darlehen)	zusammen 80 %: A 40 + 40 · B 60 + 20 · C 70 + 10 %	35 Jahre	mind. 20 %
2.2	**Energetisch hochwertiger Neubau**	nur Zuschuss; nicht mit 2.1 kombinierbar	A 50 · B 40 · C 30 %, höchstens 90.000/75.000/60.000 € je Wohnung	35 Jahre	mind. 20 %
2.4	**Ostfriesische Inseln**	Darlehen + Zuschuss	zusammen 90 % der Herstellungskosten + 100 % der Grundstückskosten	35 Jahre	mind. 10 %
2.3	**Klimagerechte Modernisierung**	Zuschuss je gebundener Wohnung	10–40 %, höchstens 9.000–31.000 €	25 Jahre; vermietet ohne WBS 35 Jahre	mind. 20 %
2.5	**Belegungsbindungen erwerben**	Zuschuss	Festbetrag 2,00–3,00 € je m² und Monat, nach Bindungsdauer gestaffelt	5–20 Jahre	–
2.6	**Auslaufende Bindungen verlängern**	Zuschuss zur Zinsverbilligung; Antrag erst nach Prolongationsangebot der NBank	Zins 0 % auf bis zu 100 % der Restschuld, längstens 20 Jahre	+ bis zu 20 Jahre	–

ⓘ Den Antrag stellen Sie bei der Wohnraumförderstelle am Bauort, die NBank bewilligt.

SECHS VORAUSSETZUNGEN, DARUNTER BEDARF AM STANDORT

Grundcheck für Programmteil 2.1

1. **Antragsberechtigt, Finanzierung gesichert?**
2. **Vor der Bewilligung nicht begonnen?**
3. **Mehrfamilienhaus ab drei Wohnungen?**
4. **Bedarf am Standort?**
5. **Mindestens 20 % Eigenmittel?**
   Bezogen auf die zuwendungsfähigen Kosten.
6. **Grundstück gesichert?**
   Eigentum, Erbbaurecht oder gesicherter Erwerb.

Bedarfslage auf der NBank-Karte

Einheits- und Samtgemeinden



306
Bedarf gegeben

96
Bedarf gesondert nachweisen

AKTUELLE KARTE

ⓘ In beiden Fällen nötig: die einfache Bedarfsbestätigung der Wohnraumförderstelle zum Bauort.

RÜCKTRITTSKLAUSELN PRÜFT DIE NBANK IM EINZELFALL

✓ Zulässig

- Baugrundstück kaufen oder Erbbaurecht bestellen
- nicht bindende Reservierung beim Kauf
- Planung bis einschließlich Leistungsphase 6 HOAI
- Baugrund untersuchen, Grundstück herrichten

ⓘ Bedingt zulässig

- Vertrag mit eindeutigem, folgenlosem Rücktrittsrecht oder eindeutiger Bedingung für den Fall, dass die Förderung ausbleibt; die NBank prüft die Klausel im Einzelfall
- vorzeitiger Vorhabenbeginn nach Zulassung durch die NBank

⛔ Förderschädlich


- Werk-, Liefer-, Leistungs- oder Kaufvertrag (außer Baugrundstück)
- beim Ersterwerb: bindender Kaufvertrag über die Wohnungen
- Beauftragung ab Leistungsphase 7 HOAI
- erster Spatenstich
- bei 2.5: Mietvertrag oder Überlassung der Wohnung

A BIS ZUR EINKOMMENSGRENZE, B +40 %, C +60 %

Obergrenze Gesamtjahreseinkommen

in €, gültig seit 01.03.2025

A bis zur Einkommensgrenze B bis 40 % darüber C bis 60 % darüber

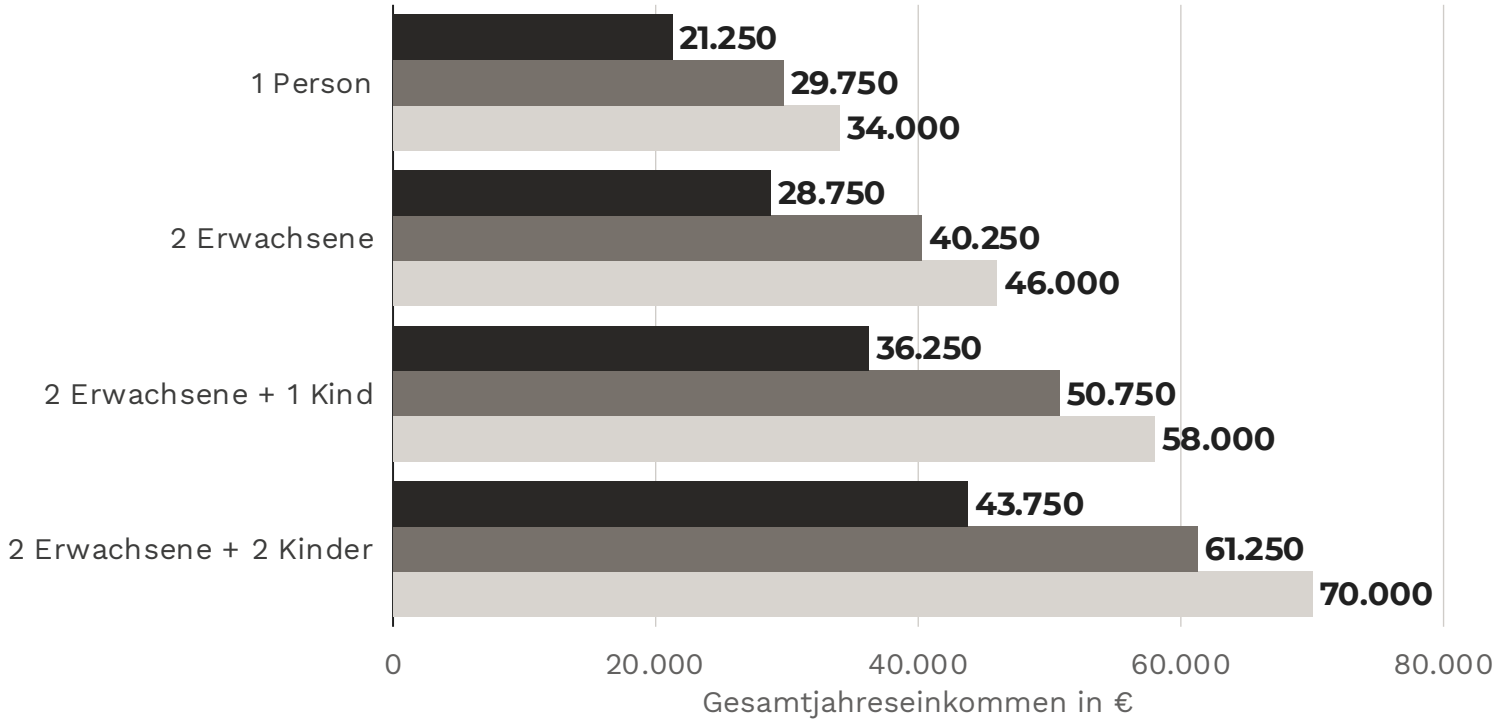

Zulassung von B und C

- Grundsatz ist Gruppe A
- B und C muss die NBank in der Förderentscheidung zulassen
- Das setzt eine besondere Lage oder Zweckbindung voraus, etwa einen angespannten Wohnungsmarkt
- Sonst sind höchstens 20 % über der Einkommensgrenze möglich, nur bei Vorhaben ab zwölf zusammenhängenden Wohnungen und für höchstens die Hälfte davon

Nachweis

- Wohnberechtigungsschein (WBS) der Kommune

PROGRAMMTEIL 2.1: DIE ZWÖLF ECKDATEN

Antrag, Bewilligung	Antrag bei der Wohnraumförderstelle am Bauort; die NBank bewilligt mit öffentlich-rechtlichem Fördervertrag
Sätze (Höchstwerte)	Darlehen 40/60/70 % plus Zuschuss 40/20/10 % (Gruppe A/B/C), zusammen 80 % der zuwendungsfähigen Kosten; Zuschuss nur mit Darlehen, B und C nur mit Zulassung
Eigenmittel	mindestens 20 % der zuwendungsfähigen Kosten; davon soll mindestens die Hälfte Geld oder lastenfreies Grundstück sein
Zins	0 % bis Ende des 35. Jahres nach Bezugsfertigkeit; danach bis zu 3 Prozentpunkte über dem Basiszinssatz, höchstens marktüblich
Tilgung	Satz legt die NBank fest; Beginn nach vollständiger Auszahlung, spätestens zwei Jahre nach dem Monat, der auf die Bekanntgabe der Förderentscheidung folgt
Kosten, laufend	Verwaltungskostenbeitrag 0,5 % p. a. auf das Restkapital, ab Auszahlungsbeginn

Kosten, einmalig	Bearbeitungsentgelt 1 % des bewilligten Darlehens und 0,75 % des bewilligten Zuschusses
Auszahlung	in Raten nach Baufortschritt; Darlehen und Zuschuss je Rate anteilig, Ihre Eigenmittel in der Regel zuerst
Sicherheiten	nachrangige Grundschuld direkt nach dem Bankdarlehen
Versicherung	Brand ab Baubeginn, Sturm ab Bezugsfertigkeit, jeweils gleitender Neuwert, bis zur vollständigen Rückzahlung
Vorzeitige Rückzahlung	Zuschuss anteilig für die restliche Bindungsdauer zurückzuzahlen; die Bindungen enden frühestens 20 Jahre nach Bindungsbeginn
Beihilferecht	Die NBank begrenzt jede Förderung so, dass die Eigenkapitalrendite angemessen bleibt (Prüfung auf Überkompensation). Bis 1 Prozentpunkt über dem 30-jährigen Swapsatz gilt sie stets als angemessen

RENDITE IN A: *7,05 %* MIT RESTWERT, 2,58 % OHNE RESTWERT

Eigenkapitalrendite über 35 Jahre, vor Steuern

Endvermögen nach 35 Jahren gegen Eigenkapital bei Bezug
frei finanziert zur Marktmiete

	POSITION	A	B	C	FREI
1	Eigenkapital bei Bezug, in €	**613.426**	**614.908**	**615.649**	**592.682**
2	Jahre mit Fehlbetrag, Jahr 1 bis 35	**0**	**0**	**0**	**1**
3	Tiefster Stand des Projektkontos, in €	**0**	**0**	**0**	**–1.691**
4	Restwert Ende Jahr 35, in Mio. €	**5,15**	**5,67**	**5,90**	**6,76**
5	**Rendite mit Restwert**	**7,05 %**	**7,28 %**	**7,40 %**	**8,36 %**
6	Rendite ohne Restwert	**2,58 %**	**2,61 %**	**2,75 %**	**4,84 %**
7	Anteil des Restwerts am Endvermögen	**78 %**	**79 %**	**79 %**	**69 %**


Annahmen

- Vor Steuern, ab Bezug: ohne Bauphase, Abschreibung und Sonder-AfA
- Grundstück im Bestand, nicht angesetzt: weder im Eigenkapital noch im Restwert
- Marktmiete 15,42 € je m²: Gutachterausschuss Lüneburg, Hamburger Umland, Neubau, Stand 01.01.2026
- Liegenschaftszins 2,80 %: Landesmodell des Oberen Gutachterausschusses
- Restwert: Ertragswert Ende Jahr 35. Marktmiete +2 % p. a.
- Fehlbeträge laufen auf ein Projektkonto zu 5 % Sollzins

BEI 2,38 % TILGUNG LIEGT GRUPPE A AB RUND *3.000 €* JE m² VORN

Tilgungsschwelle je Herstellungskosten

Tilgungssatz p. a., bis zu dem B oder C in Jahr 1 vor A liegt · Kosten in € je m²

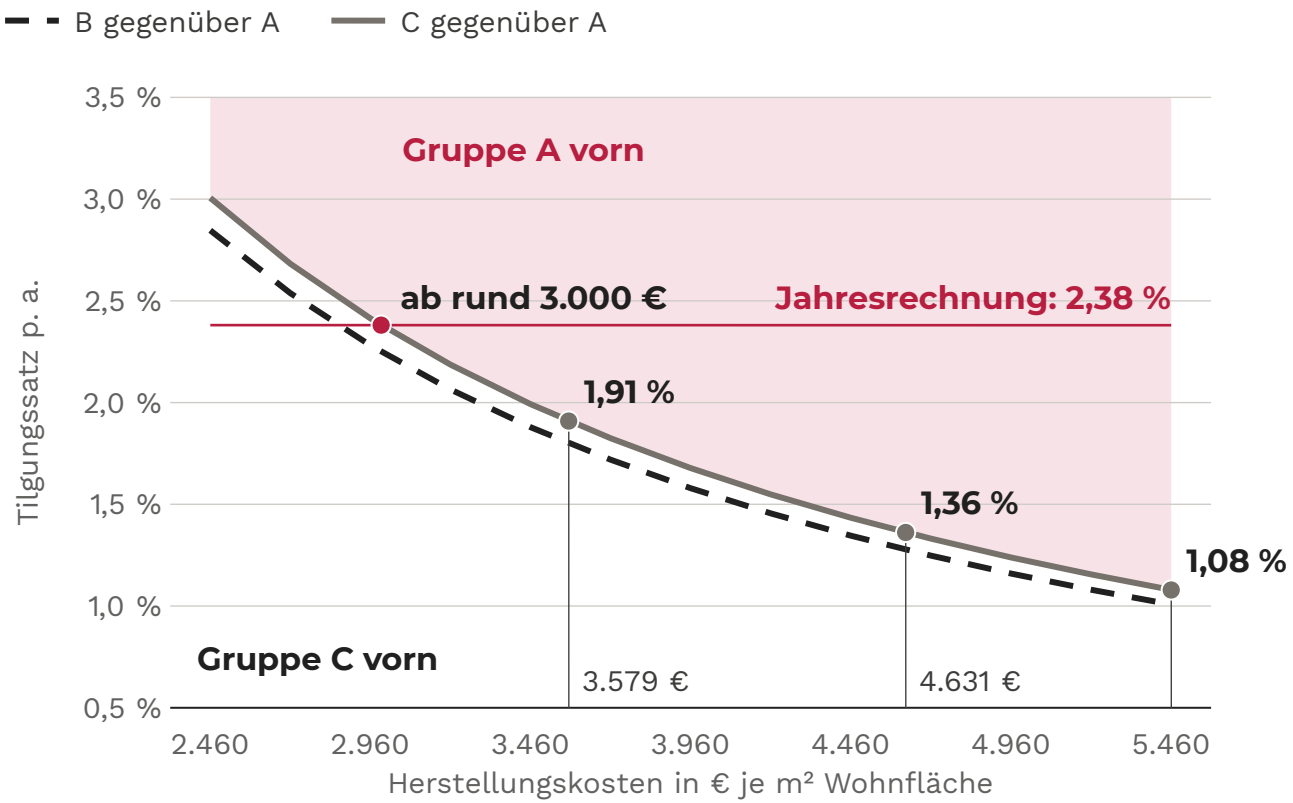

Schwelle gegenüber A

Tilgungssatz p. a. bei drei Herstellungskosten

JE m²	3.579 €	4.631 €	5.460 €
Gruppe B	**1,80 %**	**1,28 %**	**1,01 %**
Gruppe C	**1,91 %**	**1,36 %**	**1,08 %**

Lesehilfe

- über der Linie „C gegenüber A“ hat A den höchsten Zahlungsüberschuss in Jahr 1
- unter der Linie hat C den höchsten
- B hat ihn bei keinem Tilgungssatz

Warum die Schwelle mit den Kosten sinkt

- die Mehrmiete je m² ist fest vorgegeben
- die Mehrschuld wächst mit den Herstellungskosten

QUELLEN UND HINWEIS

FOLIE	QUELLE
alle	RL Mietwohnraum 2026, Runderlass des Niedersächsischen Ministeriums für Wirtschaft, Verkehr und Bauen vom 25.06.2026 (Nds. MBl. 2026 Nr. 319), gültig vom 01.07.2026 bis 31.12.2031; ergänzend NWoFG, DVO-NWoFG und WoGV; NBank-Produktinformation „Mietwohnungen in Mehrfamilienhäusern“, Stand 05.11.2026
3, 5, 22, 23	ARGE e. V. (2026): Wohnungsbau in Deutschland 2026 (Endbericht), S. 32, Abb. 20, und S. 34, Abb. 22 und 23; Folien 22 und 23: PGN (2026): eigene Auswertung von fünf Projekten, Kostenstand Q4 2025
4, 5	Zinsreihe: Dr. Klein Wowi Finanz AG (2026), Zinsentwicklung für die Wohnungswirtschaft, Monatswerte 01/2016 bis 11/2026; Folie 5: eigene Rechnung der PGN; Folie 5: GdW (2026): Präsentation zur Jahrespressekonferenz 2026, S. 15
6, 10	NBank-Wohnungsmarktbericht 2025; Folie 6: BT-Drs. 21/7303, Antwort der Bundesregierung vom 21.07.2026
9	NBank-Produktinformation „Allgemeine Mietwohnraumförderung“, Stand 01.04.2026 (Förderkonditionen bis 30.06.2026)
14–24, A6, A7	Modellrechnung der Planungsgemeinschaft Nord GmbH (Rechenmappe v3, Stand 11/2026)
A2	NBank-Landkarte Wohnraumförderung, abgerufen am 21.10.2026; Landesregierung, Pressemitteilung vom 25.11.2025
A6	Gutachterausschuss für Grundstückswerte Lüneburg: Mietübersicht Landkreis Harburg, Hamburger Umland, Stand 01.01.2026; Gutachterausschuss Niedersachsen: Landesmodell Mehrfamilienhäuser, Stand 01.01.2026
Hinweis	Alle Angaben ohne Gewähr, Stand 11/2026. Maßgeblich sind die RL Mietwohnraum 2026 und die Förderentscheidung der NBank. Fördersätze und Beträge sind Höchstwerte; die NBank prüft jede Förderung auf Überkompensation (EU-Beihilferecht). Modellrechnungen sind Rechenbeispiele, keine Förderzusage.

NBank und Land Niedersachsen sind nicht Herausgeber dieser Präsentation.
Alle Visualisierungen, Zeichnungen und Diagramme: Planungsgemeinschaft Nord GmbH