WOHNRAUM, DER SICH *RECHNEN* KANN.

Die RL Mietwohnraum 2026 für Wohnungsunternehmen, Genossenschaften, Investorinnen und Investoren sowie Kommunen.



Referenzprojekt Brauerstraße, Rotenburg (Wümme)
19 barrierefreie Wohnungen · mit Förderung der NBank

PGN ARCHITEKTEN STADTPLANER INGENIEURE

Herausgeber
Planungsgemeinschaft Nord GmbH Rotenburg (Wümme)

Stand **30.09.2026**


Vortrag

BIS ZU 80 %
Förderquote aus Darlehen und Zuschuss
der zuwendungsfähigen Kosten · Programmteil 2.1

KREDITE KOSTETEN ENDE 2025
DREI BIS VIER PROZENT

SOLLZINS P. A. NACH ZINSBINDUNG

in %, Monatswerte 01/2016 bis 07/2026, Top-Konditionen Wohnungswirtschaft

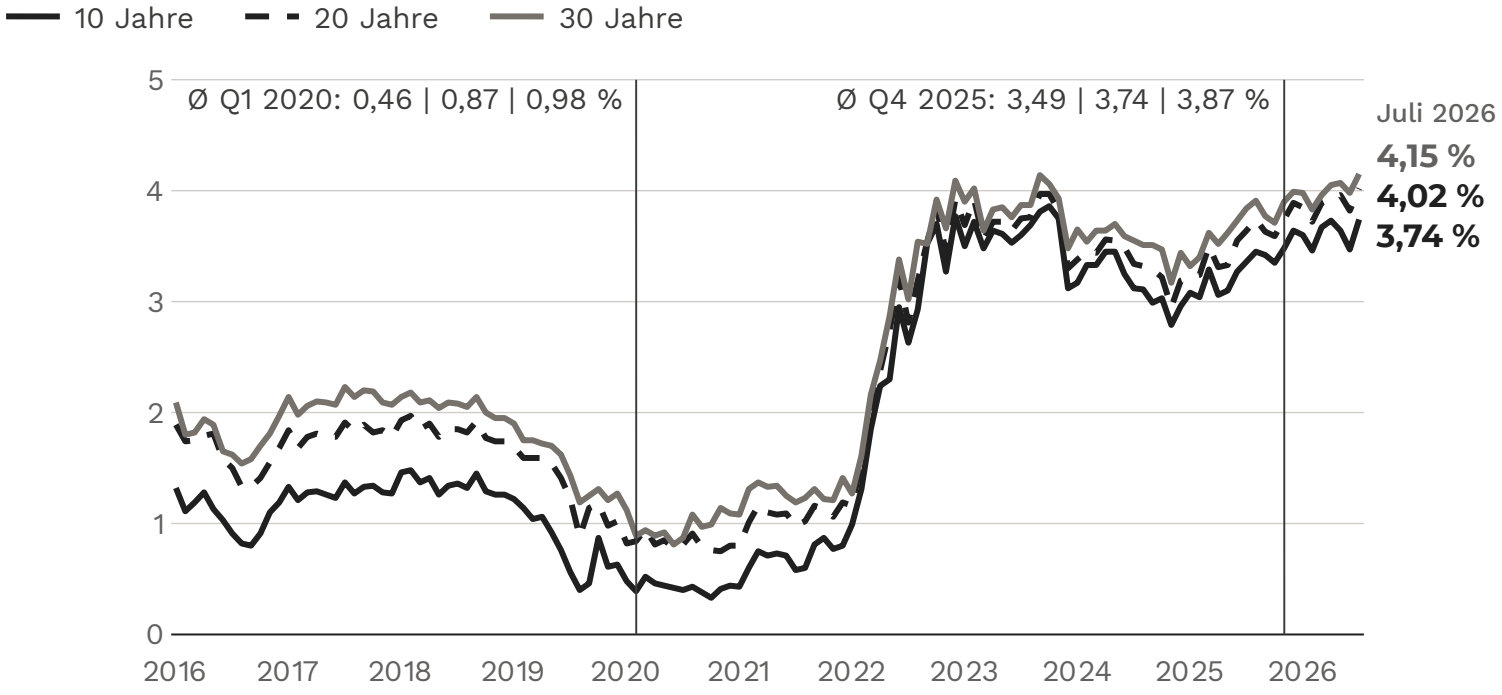

AUSGANGSLAGE

Bauen kostet mehr als doppelt so viel wie vor 25 Jahren, Kredite kosteten Ende 2025 drei bis vier Prozent, und die Zahl der Baugenehmigungen hat sich seit 2021 mehr als halbiert.

3,74 %

Juli 2026, 10 Jahre Zinsbindung. Mit diesem Zins rechnet die Modellrechnung das Bankdarlehen.

SEIT 01.07.2026: DARLEHEN PLUS *ZUSCHUSS* STATT TILGUNGSNACHLASS

BIS 30.06.2026

75 % Darlehen

Instrument: zinsloses Darlehen, 75 % der Gesamtkosten; Tilgungsnachlass 30 % des Darlehens nur bei geringen Einkommen

Bemessung je m² Wohnfläche: 5.330/5.550 € Gesamtkosten, Neubau inkl. Grundstück

Mieterkreis und Höchstmiete Jahre 1–3 (nettokalt je m²): geringe und mittlere Einkommen; 6,30/6,60 € (geringe)

→

SEIT 01.07.2026

80 % Förderung

Instrument: Darlehen + Zuschuss statt Tilgungsnachlass; zusammen 80 % der zuwendungsfähigen Kosten (Gruppe A: je 40 %)

Bemessung je m² Wohnfläche: Ausgangswerte 4.800/5.000 € Herstellungskosten; Grundstück separat bis Bodenrichtwert


Mieterkreis und Höchstmiete Jahre 1–3 (nettokalt je m²): Gruppen A, B, C (B/C nur mit Zulassung); A: 6,50/6,80 €

Programmteil 2.1 im Vergleich · Höchstsätze · Wertepaare: Mietenstufe I–III/IV–VII · Bemessung nicht direkt vergleichbar

HÖCHSTMIETE IN PROGRAMMTEIL 2.1: 6,50–9,00 € JE m², *DREI JAHRE FEST*

HÖCHSTMIETE NETTOKALT, JAHRE 1–3

€ je m² und Monat · nach Einkommensgruppe und Mietenstufe

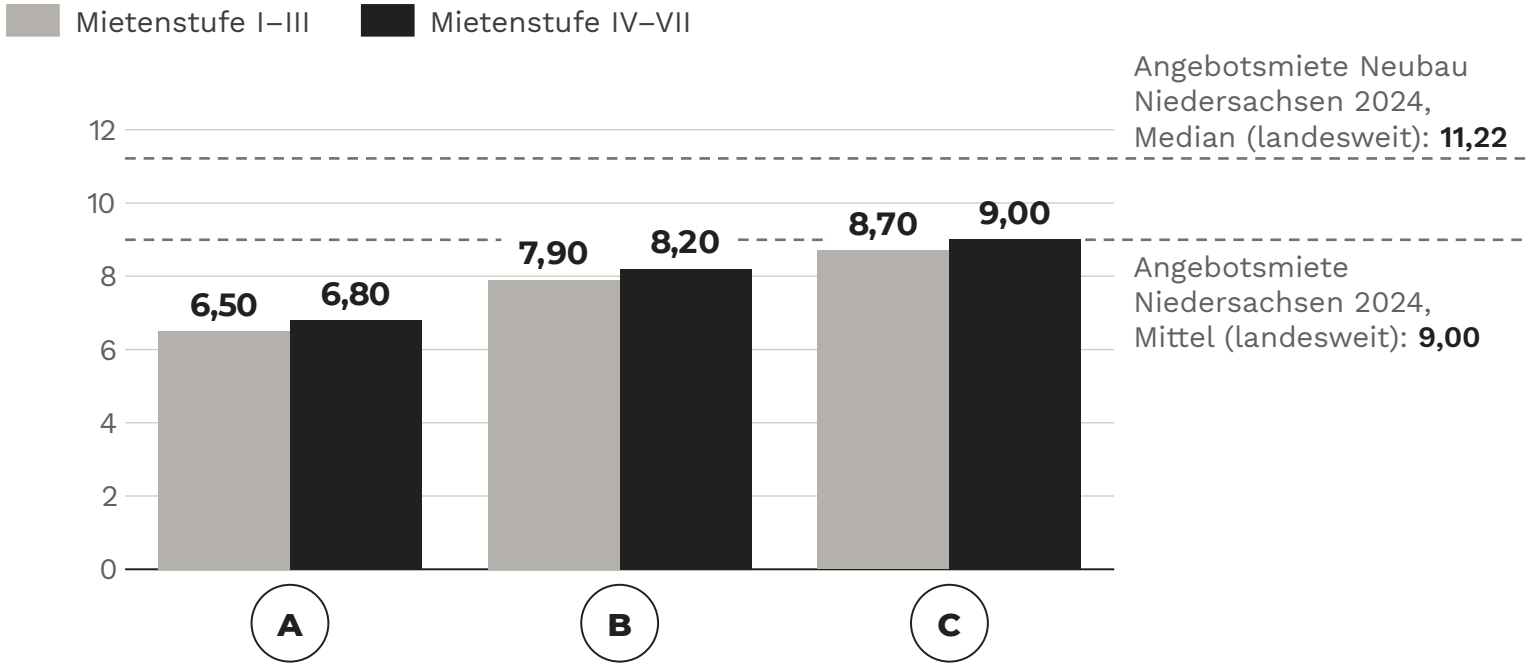

Ab EH-40-Niveau bis zu +0,30 €.

MIETPFAD

Gruppe A · Mietenstufe IV–VII

Jahr 1–3		**6,80 €**
ab Jahr 4	höchstens	**7,21 €**
ab Jahr 7	höchstens	**7,65 €**

REGEL

Ab Jahr 4 höchstens +6,15 % in drei Jahren, auch bei Wiedervermietung; keine Staffel- oder Indexmiete.


GRUPPEN

Grundsatz ist Gruppe A; B und C nur mit Zulassung in der Förderentscheidung.

IN JEDER EINKOMMENSGRUPPE BIS ZU *80 %* FÖRDERQUOTE

FÖRDERMIX JE EINKOMMENSGRUPPE

Höchstsätze in % der zuwendungsfähigen Kosten

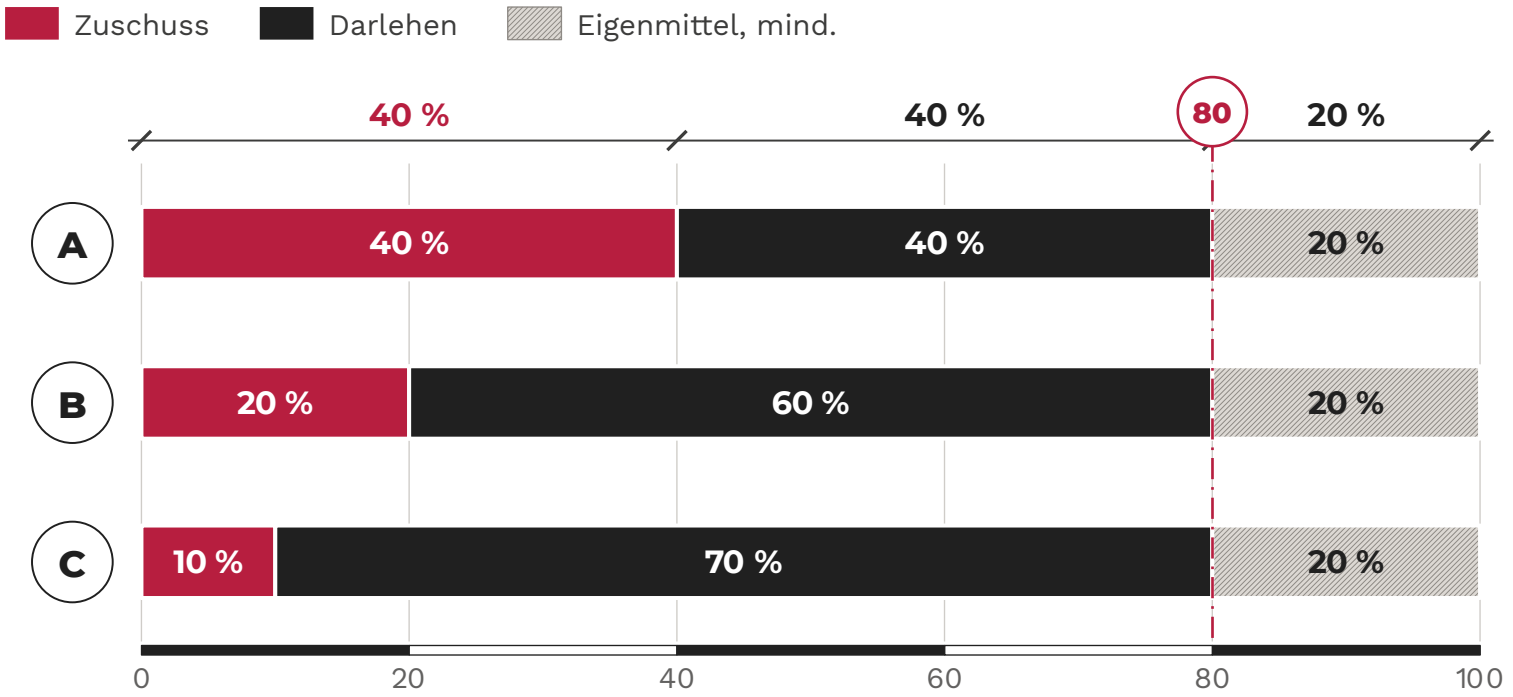

REGELFALL GRUPPE A

B und C mit Zulassung in der Förderentscheidung. Der Zuschuss wird nur zusammen mit dem Darlehen gewährt.

EIGENMITTEL


Mindestens 20 % der zuwendungsfähigen Kosten; mindestens die Hälfte als Geld oder lastenfreies Grundstück.

BEMESSUNGSGRENZE

4.800 € je m² Wohnfläche in Mietenstufe I–III, 5.000 € in IV–VII; Ausgangswerte, fortgeschrieben zum 01.04. und 01.10.; aktuell auf nbank.de.

35 JAHRE ZINSFREI UND GEBUNDEN, HÖCHSTENS 42 JAHRE LAUFZEIT

DARLEHEN UND BINDUNG IM ZEITVERLAUF

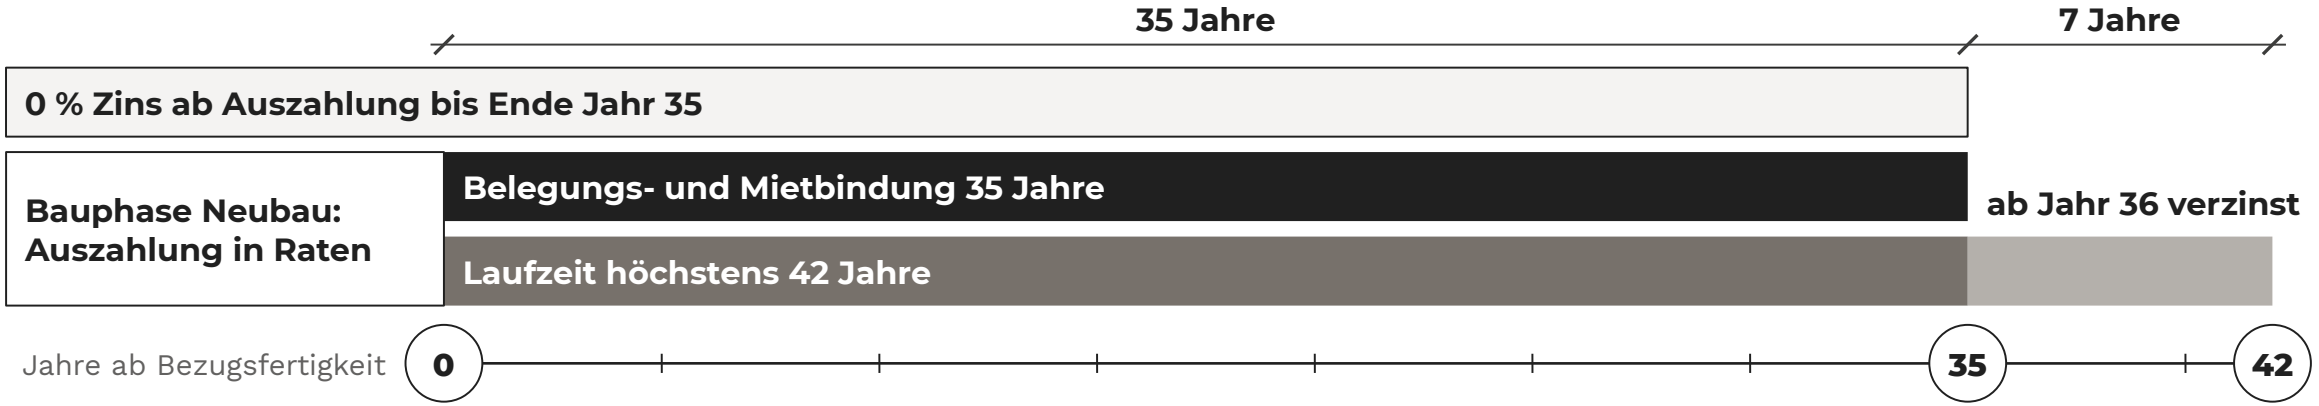

0,5 % p. a.

Verwaltungskostenbeitrag

auf das Restkapital, ab Auszahlungsbeginn

1 % / 0,75 %

Bearbeitungsentgelt, einmalig

des Darlehens / des Zuschusses

TILGUNG

Den Satz legt die NBank fest. Beginn nach vollständiger Auszahlung.

4

IHRE RECHNUNG: DAS *MODELLHAUS*

Ein Neubau mit 20 Wohnungen nach Programmteil 2.1, einmal gefördert und einmal frei finanziert gerechnet.
Die Rechnung zeigt die Liquidität in Jahr 1 bei Kostenstand 2026, keine Rendite.

fiktives Beispiel, keine Förderzusage **MODELLRECHNUNG**

20 WOHNUNGEN, 7,0 MIO. €: BIS ZU *5,6 MIO. €* FÖRDERUNG

20 NEUBAUWOHNUNGEN NACH PROGRAMMTEIL 2.1 · 1.400 m² WOHNFLÄCHE · GRUPPE A · MIETENSTUFE IV–VII

FINANZIERUNG 7,0 MIO. €, HÖCHSTSÄTZE



RECHENWEG, IN €

1		Herstellungskosten, 1.400 m² × 4.500 €	**6.300.000**
2	+	Grundstück	**700.000**
3	=	**zuwendungsfähige Kosten**	**7.000.000**
4		Eigenmittel, mindestens 20 %	**1.400.000**

Von den Eigenmitteln sollen mindestens 700.000 € Geld oder lastenfreies Grundstück sein. 4.500 € je m² liegen 500 € unter dem Ausgangswert der Bemessungsgrenze von 5.000 €.

BIS ZU

140.000 €

Ø Zuschuss je Wohnung

plus Darlehen in gleicher Höhe

MIND.

70.000 €

Ø Eigenmittel je Wohnung

20 % von 350.000 € Gesamtkosten

JAHR 1: ZAHLUNGSÜBERSCHUSS *455 €* IN A, FEHLBETRÄGE IN B UND C

JAHRESRECHNUNG JAHR 1, IN € P. A.

Höchstmiete nettokalt, Mietenstufe IV–VII: 6,80 | 8,20 | 9,00 € je m² (A | B | C)

		POSITION	A	B	C
1		Sollmiete zur Höchstmiete	**114.240**	**137.760**	**151.200**
	–	Mietausfall/Leerstand, 2 %	**2.285**	**2.755**	**3.024**
2	–	Objektverwaltung, 367 € je Wohnung	**7.340**	**7.340**	**7.340**
3	–	Instandhaltung, 14,40 € je m²	**20.160**	**20.160**	**20.160**
4	=	**Überschuss vor Kapitaldienst**	**84.455**	**107.505**	**120.676**
5	–	Verwaltungskostenbeitrag, 0,5 %	**14.000**	**21.000**	**24.500**
6	–	Zins NBank-Darlehen, 0 %	**0**	**0**	**0**
7	–	Tilgung 2,5 % p. a. (Annahme)	**70.000**	**105.000**	**122.500**
8	**=**	**Zahlungsüberschuss p. a.**	**455**	**–18.495**	**–26.324**

Einmalig, außerhalb der Jahresrechnung: Bearbeitungsentgelte 49.000 | 52.500 | 54.250 €

ANNAHMEN

Liquidität in Jahr 1 bei Kostenstand 2026, keine Rendite.

Tilgung auf 2,8 | 4,2 | 4,9 Mio. € Darlehen. Den Tilgungssatz legt die NBank fest.


B und C setzen eine Zulassung in der Förderentscheidung voraus.

MODELLRECHNUNG

KAPITALDIENST IN JAHR 1: *84.000 €* STATT 313.703 € FREI FINANZIERT

KAPITALDIENST IN JAHR 1

in € p. a. · dasselbe Haus, gefördert und frei finanziert

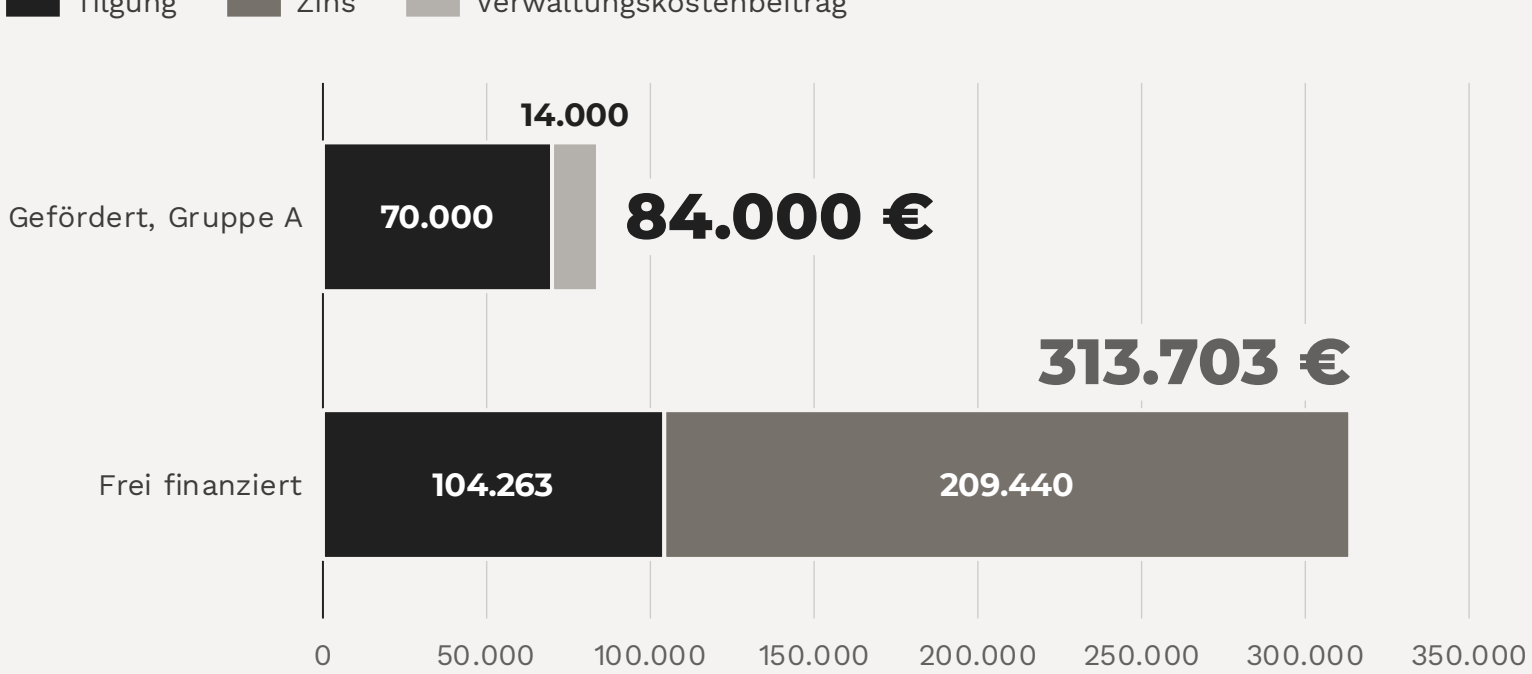

ANNAHMEN

Frei finanziert: gleiches Haus, Eigenmittel 1,4 Mio. €, Bankdarlehen 5,6 Mio. € zu 3,74 % Zins, Annuität über 30 Jahre. Objektverwaltung und Instandhaltung wie gefördert.


Gefördert: Zuschuss 2,8 Mio. €, Darlehen 2,8 Mio. € zu 0 % Zins, Tilgung 2,5 % p. a. (Annahme).

MODELLRECHNUNG

NÖTIGE MIETE: 6,77 € GEFÖRDERT, 20,72 € JE m² FREI FINANZIERT

NÖTIGE MIETE IN JAHR 1

Miete je m² und Monat, bei der der Zahlungsüberschuss null ist

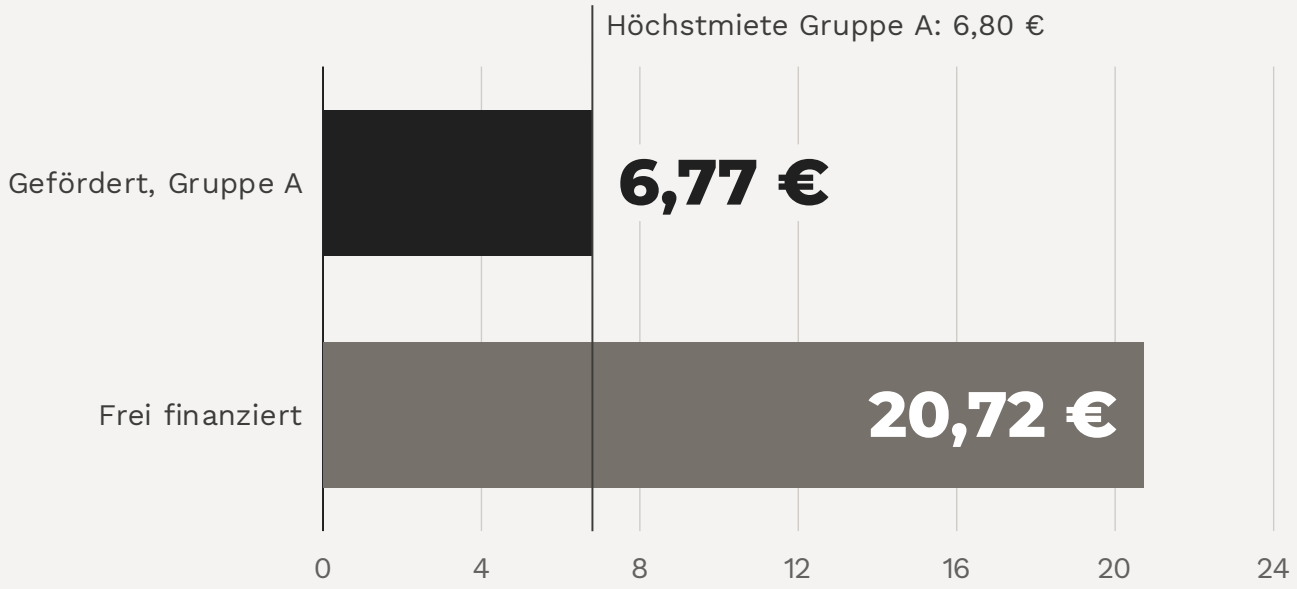

ZUM VERGLEICH: FREI FINANZIERT

JAHR 1	GEFÖRDERT (A)	FREI FINANZIERT
Zuschuss	2,8 Mio. €	0
Darlehen	2,8 Mio. €	5,6 Mio. €
Kapitaldienst p. a.	84.000 €	313.703 €
Nötige Miete je m²	**6,77 €**	**20,72 €**


MODELLRECHNUNG

DER *TILGUNGSSATZ* ENTSCHEIDET ÜBER DEN ZAHLUNGSÜBERSCHUSS IN JAHR 1

2.1

ZAHLUNGSÜBERSCHUSS JE TILGUNGSSATZ

Jahr 1, in € p. a. · Tilgungssatz p. a. auf das NBank-Darlehen

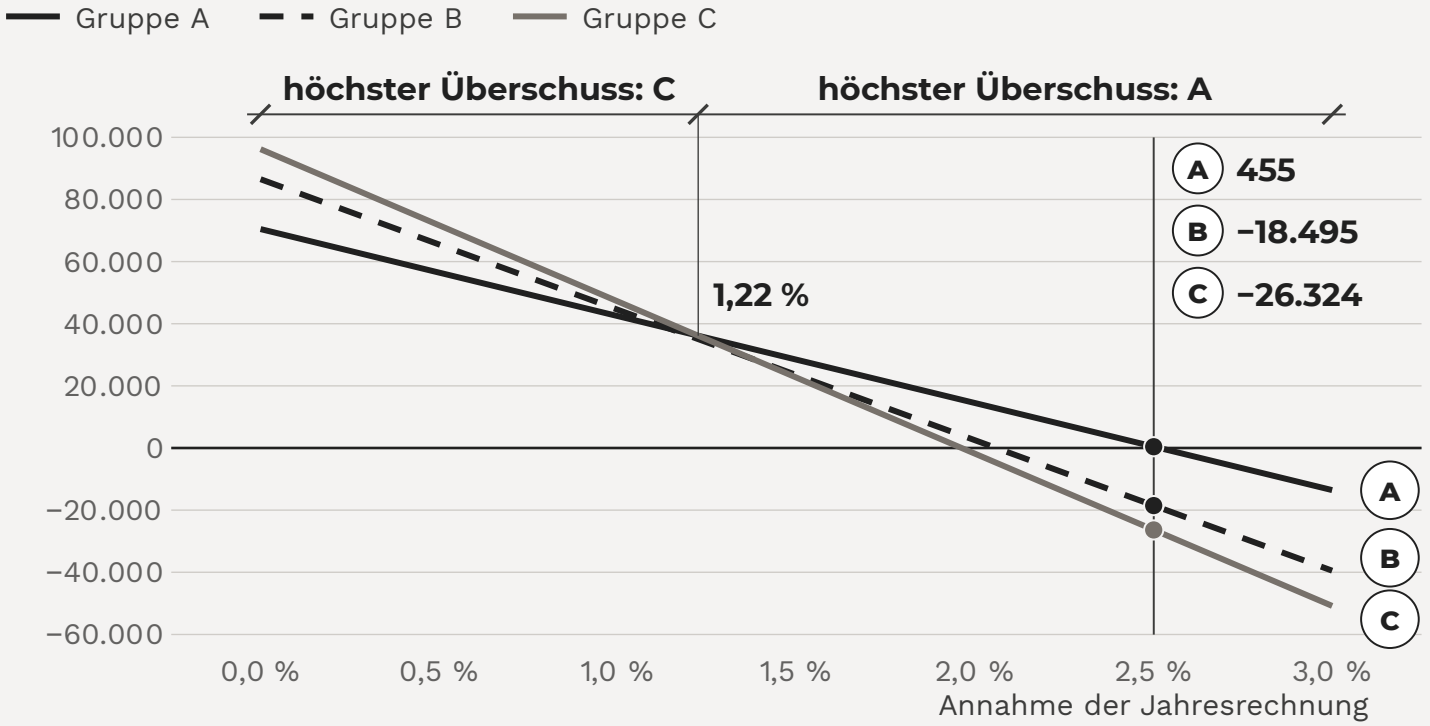

Unter 1,22 % Tilgung bringt C den höchsten Zahlungsüberschuss, darüber A.


B liegt in dieser Rechnung nie vorn.

Den Tilgungssatz legt die NBank fest, die Richtlinie nennt keinen.

AB JAHR 10 ZAHLUNGSÜBERSCHUSS IN ALLEN DREI EINKOMMENSGRUPPEN

ZAHLUNGSÜBERSCHUSS JAHR 1 BIS 35

in € p. a. · Modellhaus, Gruppen A, B und C

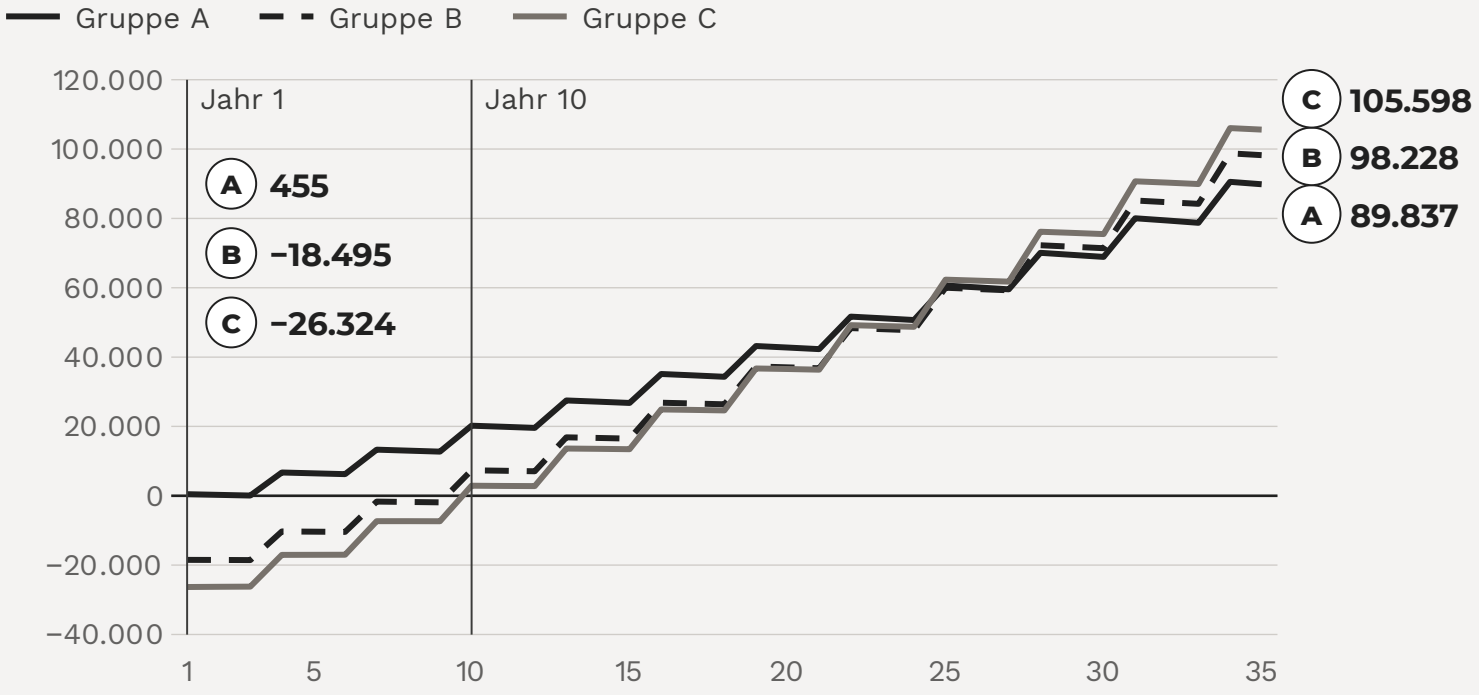

ANNAHMEN

Tilgung 2,5 % p. a. (Annahme). Miete alle drei Jahre +6,15 % (Höchstwert). Objektverwaltung und Instandhaltung ab Jahr 2 +2 % p. a.


B UND C

Neun Jahre mit Fehlbetrag, zusammen bis zu 92.052 € (B) und 151.922 € (C).

HERSTELLUNGSKOSTEN JE m² BESTIMMEN FÖRDERQUOTE UND ZAHLUNGSÜBERSCHUSS

ZAHLUNGSÜBERSCHUSS JAHR 1, GRUPPE A

in € p. a. · nach Herstellungskosten je m² Wohnfläche

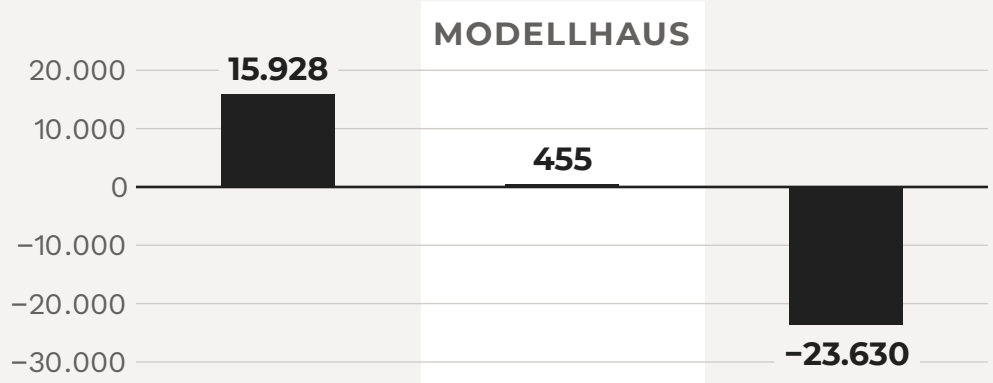

	JE m² WOHNFLÄCHE	3.579 €	4.500 €	5.200 €
1	Gesamtkosten	**5,71 Mio. €**	**7,00 Mio. €**	**7,98 Mio. €**
2	Förderung, Höchstsätze	**4,57 Mio. €**	**5,60 Mio. €**	**6,16 Mio. €**
3	Förderquote auf die Gesamtkosten	**80 %**	**80 %**	**77,2 %**
4	Nötige Miete je m², Gruppe A	**5,83 €**	**6,77 €**	**8,24 €**

SZENARIEN

Geändert sind nur die Herstellungskosten. Grundstück 700.000 €, Mieten und Annahmen wie im Modellhaus.

3.579 € JE m²

Median aus fünf PGN-Projekten, Kostengruppen 200–700, Kostenstand Q4 2025.

5.200 € JE m²

200 € über dem Ausgangswert der Bemessungsgrenze von 5.000 €. 0,28 Mio. € sind nicht zuwendungsfähig.

TILGUNGSSATZ, KOSTEN UND HÖCHSTMIETE BESTIMMEN *DAS ERGEBNIS*

BIS ZU

5,6 Mio. €

Förderung

80 % von 7,0 Mio. €: je 2,8 Mio. €
Darlehen und Zuschuss.
Bindung 35 Jahre.

KAPITALDIENST IN JAHR 1

84.000 €

gefördert, Gruppe A

Frei finanziert: 313.703 €.

NÖTIGE MIETE IN JAHR 1

6,77 € je m²

gefördert, Gruppe A

Frei finanziert: 20,72 €.
Höchstmiete: 6,80 €.

DAS ERGEBNIS HÄNGT AB VON

TILGUNGSSATZ

Annahme 2,5 % p. a.; den Satz legt die NBank fest.

HERSTELLUNGSKOSTEN JE m²

Zuwendungsfähig bis zur Bemessungsgrenze, Ausgangswert 5.000 € in Mietenstufe IV–VII.

HÖCHSTMIETE

Nach Einkommensgruppe und Mietenstufe; im Modellhaus 6,80 €.

ERST DIE BEWILLIGUNG, DANN *VERTRÄGE UND BAUBEGINN*

1 VORGESPRÄCH
Förderstelle mit Ihnen
Nachweise und Unterlagen vorab klären

2 ANTRAG
Sie
bei der Wohnraumförderstelle am Bauort

3 STELLUNGNAHME
Förderstelle
Bedarfsbestätigung, Weiterleitung an die NBank

4 ENTSCHEIDUNG
NBank
Fördervertrag oder Bescheid; Ziel: höchstens drei Monate

±0 BEWILLIGUNG Vor der Bewilligung begonnene Vorhaben werden nicht gefördert.

5 BAUAUSFÜHRUNG
Sie
Baubeginn spätestens vier Monate nach Bekanntgabe der Förderentscheidung

6 AUSZAHLUNG
NBank
in Raten nach Baufortschritt


7 FERTIGSTELLUNG
Förderstelle mit Ihnen
Vermietung nur mit WBS

8 VERWENDUNGSNACHWEIS
Sie
innerhalb von sechs Monaten nach Erfüllung des Förderzwecks

Als Beginn gilt ein Bau-, Liefer- oder Kaufvertrag (außer für das Baugrundstück) oder der erste Spatenstich.

PLANUNG BIS LEISTUNGSPHASE 6 IST *VOR DER BEWILLIGUNG* MÖGLICH

EIN ANSPRECHPARTNER FÜR ALLES, VON DER MACHBARKEIT BIS ZUR ÜBERGABE.

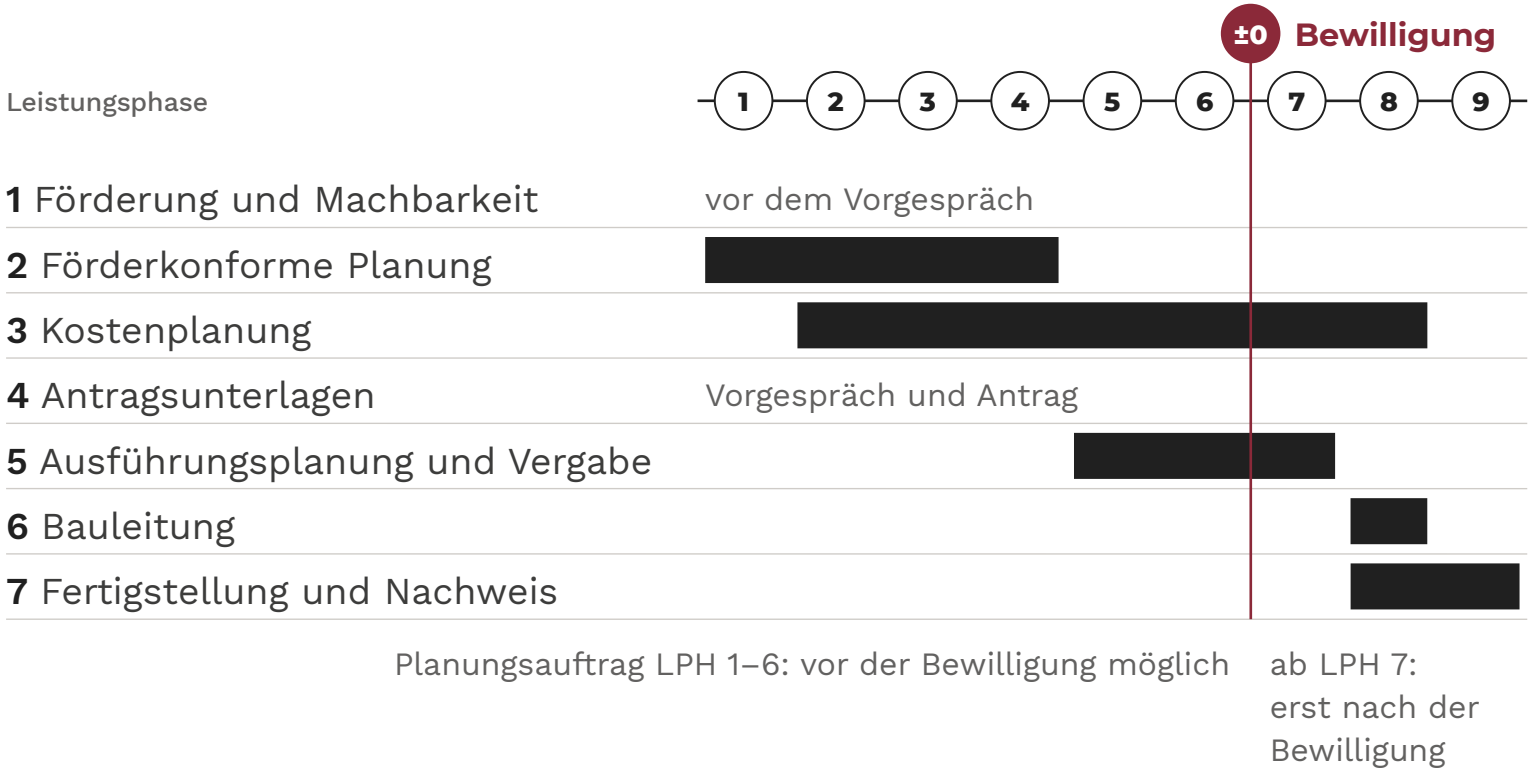



Visualisierung

Brauerstraße, Rotenburg (Wümme)
19 barrierefreie Wohnungen

MIT FÖRDERUNG DER NBANK


FÖRDERUNG UND MACHBARKEIT

Wir klären Programmteil, Standort und Mieterkreis und ermitteln Flächen und Kosten für Ihre Wirtschaftlichkeitsberechnung.

AUS IHRER GUTEN IDEE

MACHEN WIR DEN *BESTEN PLAN.*

Wir planen Ihr Vorhaben im geförderten Mietwohnungsbau, von der Machbarkeit bis zur Fertigstellung. Sprechen Sie uns an.

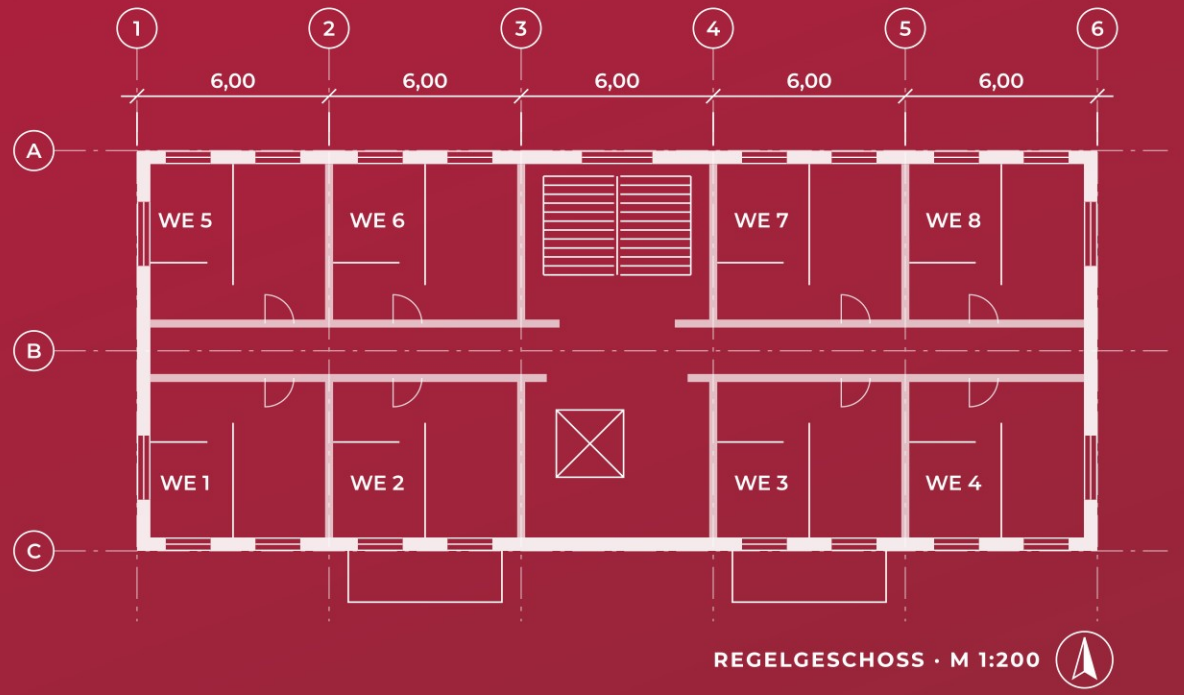

REGELGESCHOSS · M 1:200

PGN ARCHITEKTEN STADTPLANER INGENIEURE

PLANUNGSGEMEINSCHAFT NORD GMBH
Große Straße 49 · 27356 Rotenburg (Wümme)

Telefon
(+49) 4261 9293-0

E-Mail
info@pgn-architekten.de

Web
www.pgn-architekten.de

A ANHANG

Programmteile und Frist · Voraussetzungen und Verträge
Mieterkreis und Eckdaten · Herstellungskosten und Markt
Quellen

VIER AUSGANGSLAGEN FÜHREN ZU SECHS PROGRAMMTEILEN

DIE SECHS PROGRAMMTEILE

Höchstsätze · B und C nur mit Zulassung

Neu schaffen oder erstmals erwerben: 2.1, 2.2, 2.4 · **Bestand modernisieren:** 2.3 · **Bestandswohnung binden:** 2.5 · **Bindung verlängern:** 2.6

	PROGRAMMTEIL	INSTRUMENT	BIS ZU	BINDUNG	EIGENMITTEL
2.1	**Neubau, Änderung und Erweiterung, Ersterwerb**	Darlehen + Zuschuss (Zuschuss nur mit Darlehen)	zusammen 80 %: A 40 + 40 · B 60 + 20 · C 70 + 10 %	35 Jahre	mind. 20 %
2.2	**Energetisch hochwertiger Neubau**	nur Zuschuss; nicht mit 2.1 kombinierbar	A 50 · B 40 · C 30 %, max. 90.000/75.000/60.000 € je Wohnung	35 Jahre	mind. 20 %
2.4	**Ostfriesische Inseln**	Darlehen + Zuschuss	zusammen 90 % der Herstellungskosten + 100 % der Grundstückskosten	35 Jahre	mind. 10 %
2.3	**Klimagerechte Modernisierung**	Zuschuss je gebundener Wohnung; Wahlrecht bis 31.12.2026	10–40 %, höchstens 9.000–31.000 €	25 Jahre; vermietet ohne WBS 35 Jahre	mind. 20 %
2.5	**Belegungsbindungen erwerben**	Zuschuss	Festbetrag 2,00–3,00 € je m² und Monat, nach Bindungsdauer gestaffelt	5–20 Jahre	–
2.6	**Auslaufende Bindungen verlängern**	Zuschuss zur Zinsverbilligung; Antrag erst nach Prolongationsangebot der NBank	Zins 0 % auf bis zu 100 % der Restschuld, längstens 20 Jahre	+ bis zu 20 Jahre	–

Den Antrag stellen Sie bei Ihrer kommunalen Wohnraumförderstelle, die NBank bewilligt.

31.12.2026: WAHLRECHT FÜR MODERNISIERUNGSANTRÄGE

FRIST 31.12.2026

Geht Ihr Modernisierungsantrag bis 31.12.2026 bei der Wohnraumförderstelle ein, können Sie darin ausdrücklich das alte Recht (Förderregeln 2024) wählen. **Die Wahl ist bindend**; das alte Recht gilt dann bis zum Abschluss des Verfahrens. Ohne Wahl gilt die RL 2026; Neubau, Ersterwerb und alle übrigen Vorhaben werden nur nach RL 2026 gefördert.

STICHTAGE JUNI 2026 BIS DEZEMBER 2031

1 **30.06.2026**
Förderregeln 2024 enden

2 **01.07.2026**
RL Mietwohnraum 2026 in Kraft

3 **31.12.2026**
Wahlrecht Modernisierung
Antragseingang bei der Wohnraumförderstelle

4 **01.01.2027**
Neue Rechennorm für Energiebedarfsausweise
Klassengrenzen unverändert

5 **2027**
Neue Mietenstufen geplant
Entwurf

6 **31.12.2031**
RL Mietwohnraum 2026 läuft aus

2.3 Programmteil 2.3 nach RL 2026: Zuschuss je nach Klassensprung und Einkommensgruppe bis zu 10–40 %, höchstens 9.000–31.000 € je gebundener Wohnung.

SECHS VORAUSSETZUNGEN, DARUNTER BEDARF AM STANDORT

GRUNDCHECK FÜR PROGRAMMTEIL 2.1

1. **Antragsberechtigt, Finanzierung gesichert?**
2. **Vor der Bewilligung nicht begonnen?**
3. **Mehrfamilienhaus ab drei Wohnungen?**
4. **Bedarf am Standort?**
5. **Mindestens 20 % Eigenmittel?**
   Bezogen auf die zuwendungsfähigen Kosten.
6. **Grundstück gesichert?**
   Eigentum, Erbbaurecht oder gesicherter Erwerb.

BEDARFSLAGE AUF DER NBANK-KARTE

Einheits- und Samtgemeinden



306
Bedarf gegeben

96
Bedarf gesondert nachweisen

In beiden Fällen nötig: die einfache Bedarfsbestätigung der Wohnraumförderstelle zum Bauort.

VERTRÄGE UND MASSNAHMEN VOR DER BEWILLIGUNG

✓ ZULÄSSIG

- Baugrundstück kaufen oder Erbbaurecht bestellen
- nicht bindende Reservierung beim Kauf
- Planung bis einschließlich Leistungsphase 6 HOAI
- Baugrund untersuchen, Grundstück herrichten

ⓘ BEDINGT ZULÄSSIG

- Vertrag mit eindeutigem, folgenlosem Rücktrittsrecht oder eindeutiger Bedingung für den Fall, dass die Förderung ausbleibt; die NBank prüft die Klausel im Einzelfall
- vorzeitiger Vorhabenbeginn nach Zulassung durch die NBank

⛔ FÖRDERSCHÄDLICH


- Bau-, Werk-, Liefer-, Leistungs- oder Kaufvertrag (außer Baugrundstück)
- beim Ersterwerb: bindender Kaufvertrag über die Wohnungen
- Beauftragung ab Leistungsphase 7 HOAI
- erster Spatenstich
- bei 2.5: Mietvertrag oder Überlassung der Wohnung

GRUNDSATZ GRUPPE A, B UND C NUR MIT ZULASSUNG

OBERGRENZE GESAMTJAHRESEINKOMMEN

in €, gültig seit 01.03.2025

A bis zur Einkommensgrenze B bis 40 % darüber C bis 60 % darüber

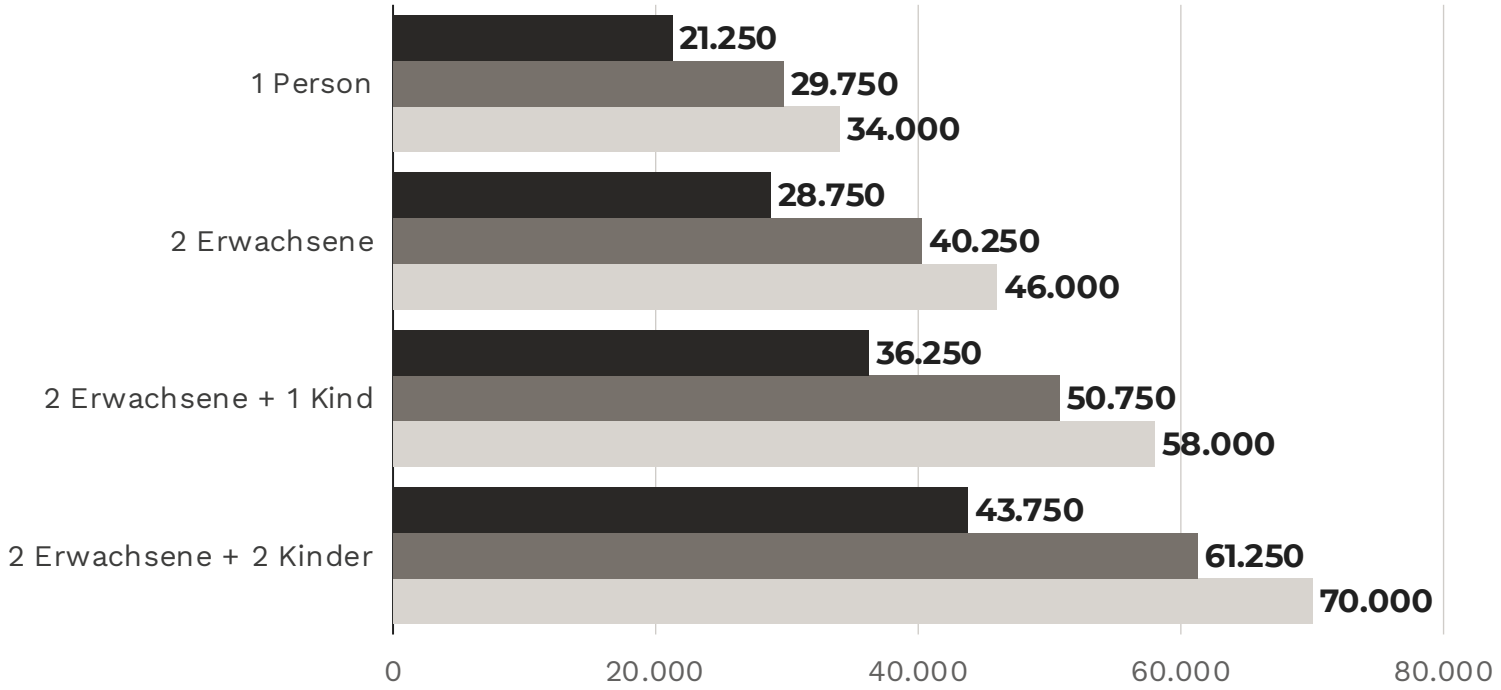

ZULASSUNG VON B UND C

Grundsatz ist Gruppe A; B und C muss die NBank in der Förderentscheidung zulassen. Bis 60 % über der Einkommensgrenze setzt das eine besondere Lage oder Zweckbindung voraus, etwa einen angespannten Wohnungsmarkt; sonst sind bei Vorhaben ab zwölf zusammenhängenden Wohnungen bis +20 % für höchstens die Hälfte der Wohnungen möglich; C entfällt dann.

NACHWEIS

Wohnberechtigungsschein (WBS) der Kommune.


ECKDATEN DES PROGRAMMTEILS 2.1

Antrag, Bewilligung	Antrag bei der Wohnraumförderstelle am Bauort; die NBank bewilligt mit öffentlich-rechtlichem Fördervertrag
Sätze (Höchstwerte)	Darlehen 40/60/70 % plus Zuschuss 40/20/10 % (Gruppe A/B/C), zusammen 80 % der zuwendungsfähigen Kosten; Zuschuss nur mit Darlehen, B und C nur mit Zulassung
Eigenmittel	mindestens 20 % der zuwendungsfähigen Kosten; mindestens die Hälfte als Geld oder lastenfreies Grundstück
Zins	0 % bis Ende des 35. Jahres nach Bezugsfertigkeit; danach bis zu 3 Prozentpunkte über dem Basiszinssatz, höchstens marktüblich
Tilgung	Satz legt die NBank fest; Beginn nach vollständiger Auszahlung, spätestens zwei Jahre nach dem auf die Bekanntgabe der Förderentscheidung folgenden Monat
Kosten, laufend	Verwaltungskostenbeitrag 0,5 % p. a. auf das Restkapital, ab Auszahlungsbeginn
Kosten, einmalig	Bearbeitungsentgelt 1 % des bewilligten Darlehens und 0,75 % des bewilligten Zuschusses
Auszahlung	in Raten nach Baufortschritt; Darlehen und Zuschuss je Rate anteilig, Ihre Eigenmittel in der Regel zuerst
Sicherheiten	nachrangige Grundschuld direkt nach den Kapitalmarktmitteln
Versicherung	Brand ab Baubeginn, Sturm ab Bezugsfertigkeit, jeweils gleitender Neuwert, bis zur vollständigen Rückzahlung
Vorzeitige Rückzahlung	Zuschuss anteilig für die restliche Bindungsdauer zurückzuzahlen; die Bindungen enden frühestens 20 Jahre nach Bindungsbeginn
Beihilferecht	Die NBank prüft jede Förderung auf Überkompensation. Eine Eigenkapitalrendite bis 1 Prozentpunkt über dem 30-jährigen Swapsatz gilt stets als angemessen.

PGN-MEDIAN 3.579 € JE m², ARGE-MEDIAN 4.631 €

HERSTELLUNGSKOSTEN JE m² WOHNFLÄCHE, MEDIAN

in €, Bruttokosten, Kostenstand Q4 2025 · PGN: fünf Projekte · ARGE: deutsche Großstädte

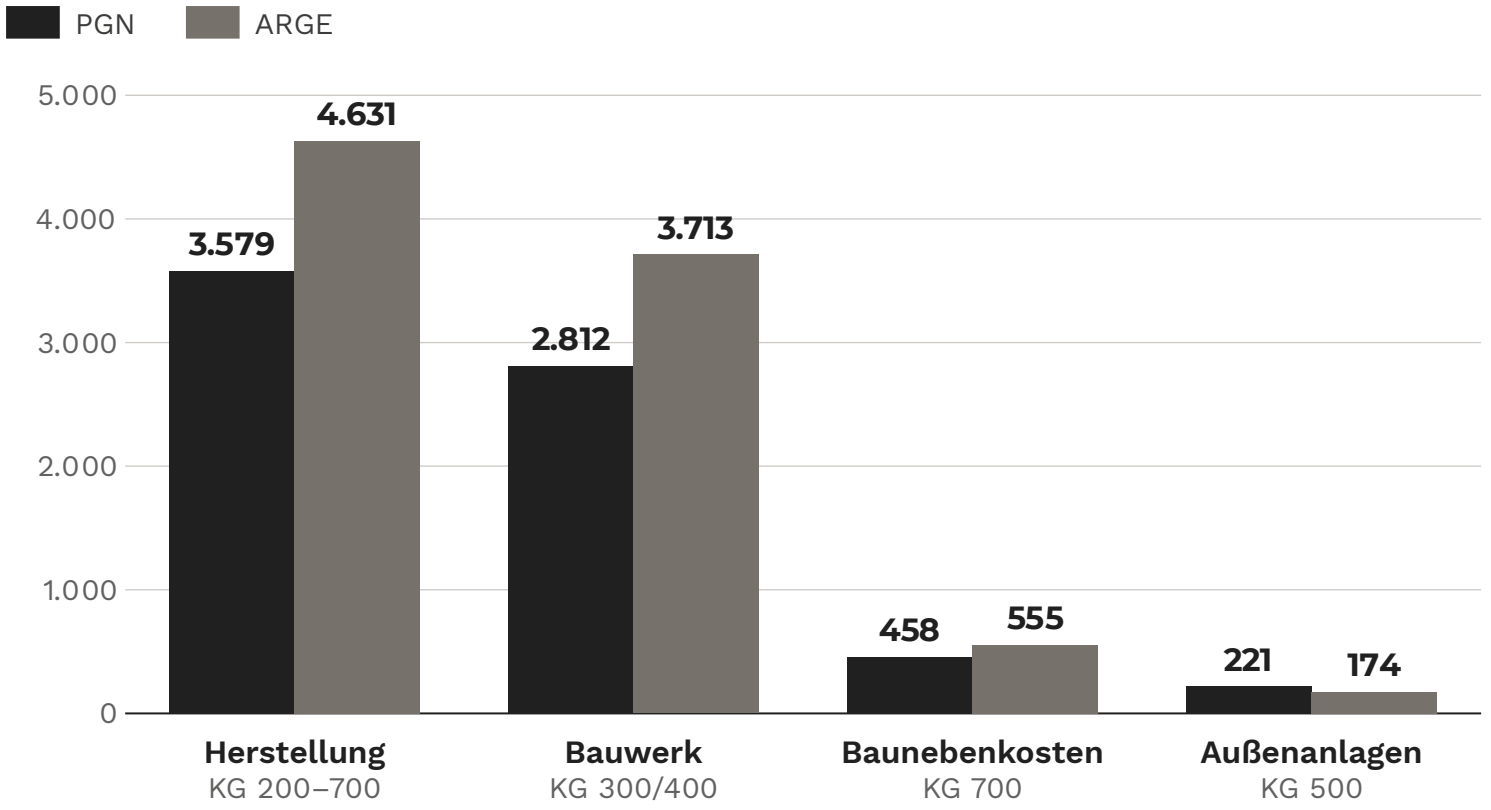

SPANNE KG 200–700

€ je m² Wohnfläche

	MIN	MEDIAN	MAX
PGN	**3.321**	**3.579**	**3.861**
ARGE	**3.221**	**4.631**	**8.592**

ARGE-Median KG 200–700 im Q1 2020: 3.028 €.


Ansatz im Modellhaus: 4.500 € je m².

SEIT 2015 NUR 28 % DER BINDUNGEN ERSETZT

28 %

der seit 2015 ausgelaufenen Bindungen neu gefördert

Seit 2015 hat die Neuförderung nur 28 % der ausgelaufenen Sozialbindungen ersetzt.

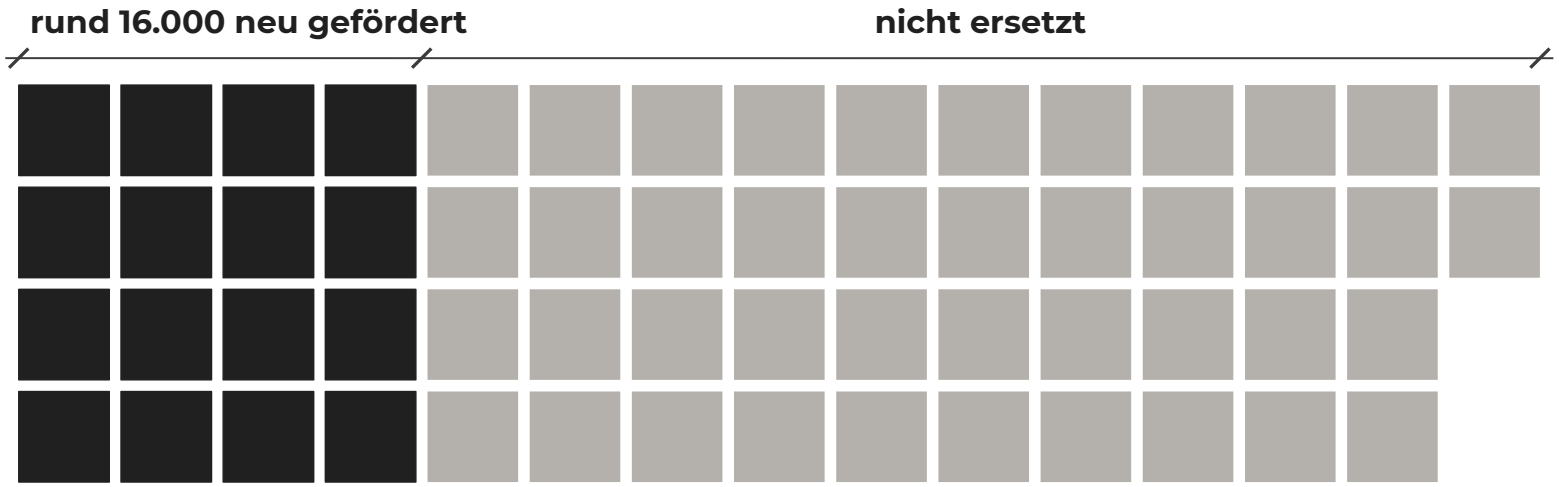

1 Quadrat = 1.000 Wohnungen · 2015–2024: 58.024 Bindungen ausgelaufen

Bestand 2024: 50.495 Sozialwohnungen, gegenüber 2015 nahezu halbiert

QUELLEN UND HINWEIS

FOLIE	QUELLE
alle	RL Mietwohnraum 2026, Runderlass des Niedersächsischen Ministeriums für Wirtschaft, Verkehr und Bauen vom 25.06.2026 (Nds. MBl. 2026 Nr. 319), gültig vom 01.07.2026 bis 31.12.2031; ergänzend NWoFG, DVO-NWoFG und WoGV
2	NBank-Pressemitteilung zur Wohnungsmarktbeobachtung vom 05.12.2025; Zinsreihe: Dr. Klein Wowi Finanz AG (2026), Zinsentwicklung für die Wohnungswirtschaft, Monatswerte 01/2016 bis 07/2026
4, A8	NBank-Wohnungsmarktbericht 2025
8–15	Modellrechnung der Planungsgemeinschaft Nord GmbH (VOFI-Mappe v3, Stand 11/2026)
14, A7	PGN (2026): eigene Auswertung von fünf Projekten, Kostenstand Q4 2025; ARGE e.V. (2026): Wohnungsbau in Deutschland 2026 (Endbericht), S. 32 und 34
A3	NBank-Landkarte Wohnraumförderung, abgerufen am 21.10.2026; Landesregierung, Pressemitteilung vom 25.11.2025

HINWEIS Alle Angaben ohne Gewähr, Stand 30.09.2026. Maßgeblich sind die RL Mietwohnraum 2026 und die Förderentscheidung der NBank. Fördersätze und Beträge sind Höchstwerte; die NBank prüft jede Förderung auf Überkompensation (EU-Beihilferecht). Modellrechnungen sind fiktive Beispiele, keine Förderzusage.

NBank und Land Niedersachsen sind nicht Herausgeber dieser Präsentation.
Alle Visualisierungen, Zeichnungen und Diagramme: Planungsgemeinschaft Nord GmbH