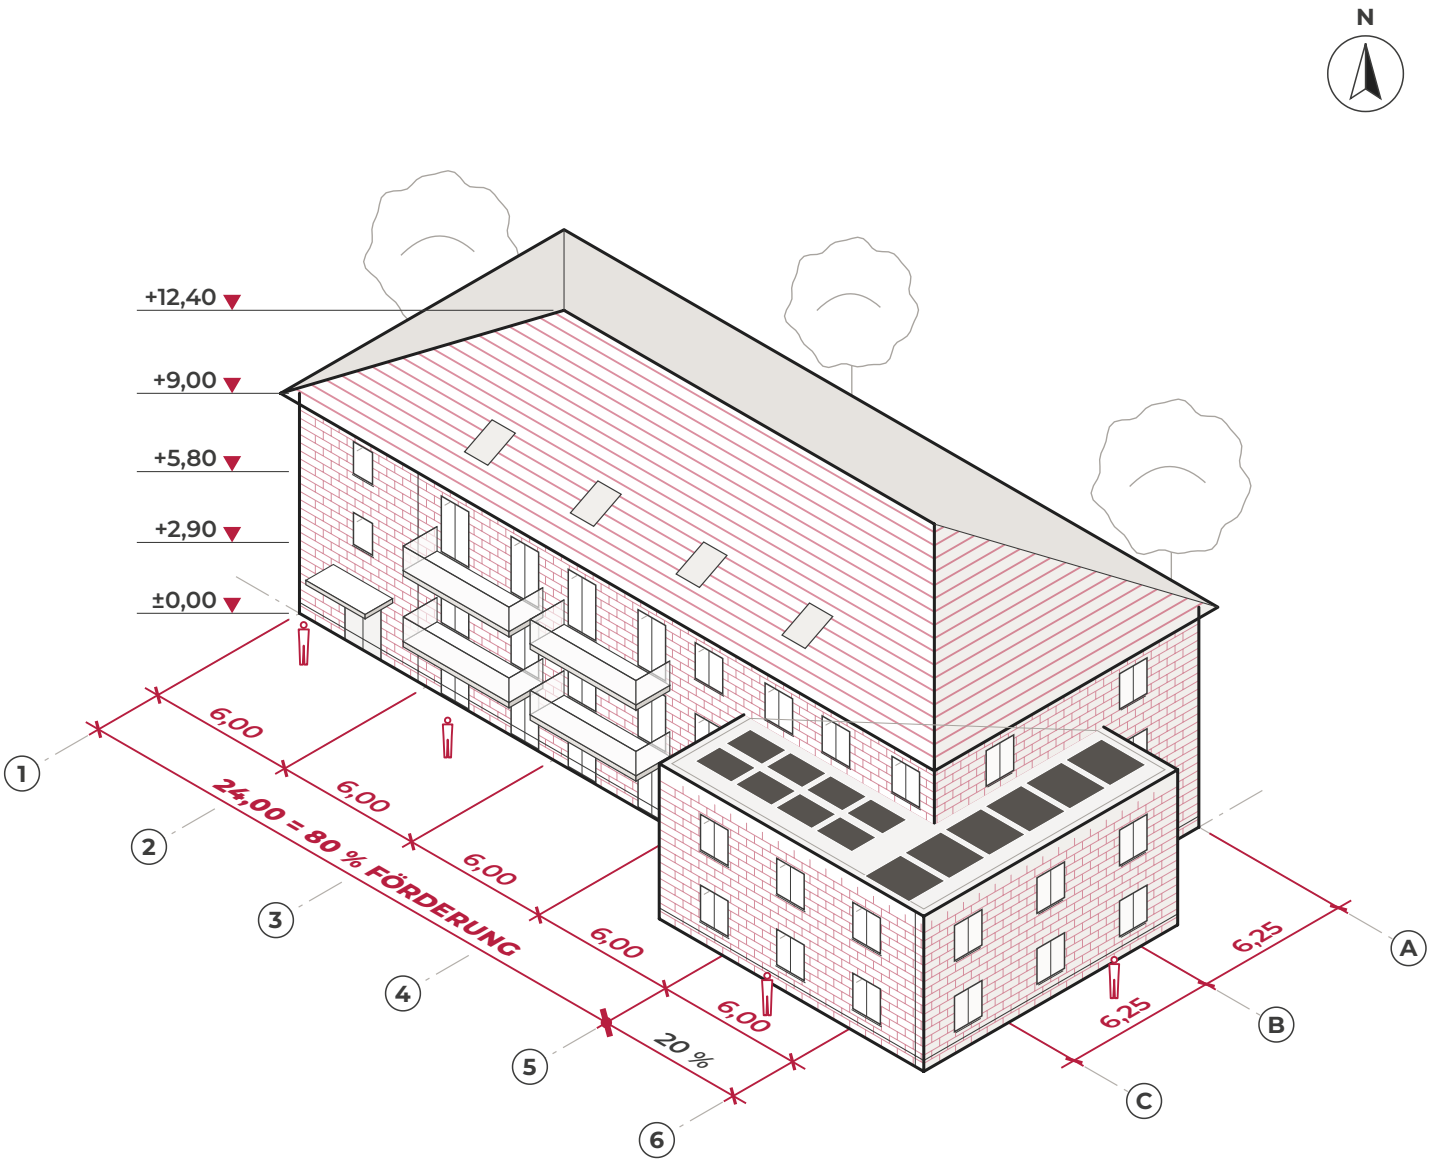


AXONOMETRIE nach dem Projekt Brauerstraße, Rotenburg (Wümme)

WOHNRAUM, DER SICH *RECHNEN* KANN.

Ein Leitfaden der PGN zur RL Mietwohnraum 2026 – für Wohnungsunternehmen, Genossenschaften, Investorinnen und Investoren sowie Kommunen.

BIS ZU

80%

Förderquote aus Darlehen und Zuschuss

der zuwendungsfähigen Kosten · Programmteil 2.1

PGN ARCHITEKTEN STADTPLANER INGENIEURE

Herausgeber
Planungsgemeinschaft Nord GmbH Rotenburg (Wümme)

Stand
21.10.2026

Blatt
U1

EDITORIAL

DAMIT SICH INVESTIEREN **WIEDER *RECHNET***

Bauen kostet mehr als doppelt so viel wie vor 25 Jahren, Kredite kosteten Ende 2025 drei bis vier Prozent, und die Zahl der Baugenehmigungen hat sich seit 2021 mehr als halbiert.

Seit dem 01.07.2026 gilt die neue RL Mietwohnraum 2026, befristet bis 31.12.2031. Für Ihre Rechnung heißt das vor allem: Statt Tilgungsnachlässen gibt es jetzt Zuschüsse, die nicht zurückgezahlt werden.

Seit 1981 planen wir Bauprojekte – heute von Rotenburg (Wümme) aus in ganz Norddeutschland, auch für Wohnungsunternehmen, Genossenschaften, Investorinnen und Investoren sowie Kommunen. Dieses Heft liest die Richtlinie aus Sicht der Planung: Was gilt, was rechnet sich, wann darf es losgehen? Das Herzstück ist **„Ihre Rechnung“ auf S. 10–11** – vom Finanzierungsaufbau bis zum laufenden Überschuss.

IHRE PGN – ARCHITEKTEN. STADTPLANER. INGENIEURE.

> *„Bezahlbarer Wohnraum entsteht nur, wenn Investitionen wieder wirtschaftlich möglich sind. Genau hier setzen wir an: Wir vereinfachen die Förderung, erhöhen die Zuschussanteile und schaffen verlässliche Rahmenbedingungen für Kommunen, Wohnungsunternehmen, Genossenschaften und private Bauherren.“*
>
> **GRANT HENDRIK TONNE**
> Niedersächsischer Wirtschafts- und Bauminister
> Pressemitteilung MW vom 03.07.2026

INHALT

ÜBERBLICK
3 Kennzahlen
4 Neu und Grundcheck
5 Navigator

ERTRAGSSEITE
6 Mieterkreis
7 Mieten

FINANZIERUNG
8 2.1 Neubau, Änderung, Ersterwerb
9 Term Sheet

IHRE RECHNUNG
10 Finanzierung
11 Wirtschaftlichkeit

NEUBAU
12 2.2 EH-40-Neubau
13 2.4 Ostfriesische Inseln

BESTAND
14 2.3 Modernisierung
15 Stichtag 31.12.2026
16 2.5 Bindungserwerb
17 2.6 Bindungsverlängerung

UMSETZUNG
18 Standort und Kommune
19 Antragsweg
20 So begleiten wir Ihr Förderprojekt
21 Unterlagen, Kontakte, Verfahrensdetails

PGN
22 Über PGN
23 Impressum und Hinweise

IHR EINSTIEG

Wohnungsunternehmen und Genossenschaften: Neubau, Modernisierung, Bindungen im Bestand – genossenschaftlich überlassener Wohnraum zählt als Mietwohnraum.
→ S. 8–17

Investorinnen und Investoren: Konditionen, Finanzierung und laufender Überschuss auf drei Seiten.
→ S. 9–11

Projektentwicklung: Verkaufen Sie bis zwei Jahre nach Fertigstellung an Käuferinnen und Käufer, die den Ersterwerb fördern lassen – den Kaufvertrag erst nach deren Bewilligung oder mit folgenlosem Rücktrittsrecht.
→ S. 8, 19

Kommunen: Selbst antragsberechtigt. Legen Sie geförderten Mietwohnraum in entsprechender Anzahl im Bebauungsplan, städtebaulichen Vertrag oder Baulandmodell fest, gilt der Bedarf als gegeben.
→ S. 18

KENNZAHLEN

DIE FÖRDERUNG IN *SIEBEN* ZAHLEN

BEGRIFF: zuwendungsfähige Kosten

Die Bezugsgröße der Förderquote – in 2.1 die Herstellungskosten bis zur Bemessungsgrenze plus Grundstückskosten bis zum Bodenrichtwert, beim Ersterwerb Kaufpreis und Erwerbskosten.

2.1

BIS ZU
80 %

Förderquote

Darlehen + Zuschuss, alle Gruppen; mehr bei Housing First und Modellprojekten → S. 8

2.1

BIS ZU
40 %

Zuschuss

Gruppe A, nur mit Darlehen; B bis zu 20 %, C bis zu 10 %, B/C nur mit Zulassung → S. 6

2.1 / 2.4

0 %

Zins bis Ende des 35. Jahres

gezählt ab Bezugsfertigkeit; dazu 0,5 % Verwaltungskostenbeitrag p. a. und einmalige Bearbeitungsentgelte → S. 9

2.1

AUSGANGSWERTE
4.800/ 5.000 €
je m² Wohnfläche

Bemessungsgrenze Herstellungskosten

Mietenstufe I–III/IV–VII; halbjährlich fortgeschrieben → S. 8

2.2

BIS ZU
90.000 €

Zuschuss je Wohnung im EH-40-Neubau

Gruppe A, höchstens 50 % der zuwendungsfähigen Kosten; nicht mit 2.1 kombinierbar → S. 12

2.3

BIS ZU
31.000 €

Modernisierungszuschuss je gebundener Wohnung

Gruppe A, ab 5 Effizienzklassen besser; höchstens 40 % der zuwendungsfähigen Kosten → S. 14

2.5

FESTBETRAG
3,00 €
je m² Wohnfläche und Monat

Zuschuss für den Bindungserwerb

15–20 Jahre Bindung; ab 5 Jahren 2,00 €, ab 10 Jahren 2,50 €; nur Gruppe A → S. 16

UND EIN STICHTAG
31.12.2026

Wahlrecht für Modernisierungsanträge

Geht Ihr Antrag bis dahin bei der Wohnraumförderstelle ein, können Sie das alte Recht wählen → S. 15

MARKT IN NIEDERSACHSEN


Wo Bedarf gilt → S. 18

50.495
Sozialwohnungen 2024
gegenüber 2015 nahezu halbiert

2015–2024 · Wohnungen

Bindungen ausgelaufen **58.024**

neu gefördert **rund 16.000**

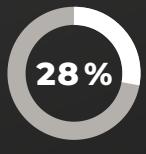

der Abgänge ersetzt

WAS NEU IST – UND OB IHR PROJEKT *PASST*

PROGRAMMTEIL 2.1 IM VERGLEICH · HÖCHSTSÄTZE

Paarwerte: Mietenstufe I–III/IV–VII · Bemessung nicht 1:1 vergleichbar	BIS **30.06.2026**	→	SEIT **01.07.2026**
Instrument	zinsloses Darlehen, **75 %** der Gesamtkosten; Tilgungsnachlass **30 %** des Darlehens nur bei geringen Einkommen	→	Darlehen + Zuschuss statt Tilgungsnachlass; zusammen **80 %** der zuwendungsfähigen Kosten (Gruppe A: je **40 %**)
Bemessung je m² Wohnfläche	**5.330/5.550 €** Gesamtkosten, Neubau inkl. Grundstück	→	Ausgangswerte **4.800/5.000 €** Herstellungskosten; Grundstück separat bis Bodenrichtwert
Mieterkreis und Höchstmiete Jahre 1–3 (nettokalt je m²)	geringe und mittlere Einkommen; **6,30/6,60 €** (geringe)	→	Gruppen A, B, C (B/C nur mit Zulassung); A: **6,50/6,80 €**

GRUNDCHECK IN SECHS FRAGEN

	GILT FÜR
☐ **Antragsberechtigt und solide finanziert?** Privatpersonen, Unternehmen mit eigener Rechtspersönlichkeit, Genossenschaften, Kommunen – und die erzielbare Miete muss Finanzierung und Bewirtschaftung dauerhaft tragen → S. 11.	2.1 2.2 2.3 2.4 2.5 2.6
☐ **Noch nicht begonnen?** Vor der Bewilligung kein Spatenstich und kein Bau-, Werk-, Liefer-, Leistungs- oder Kaufvertrag (außer Grundstück und Planung bis Leistungsphase 6 HOAI); bei 2.5 weder vermieten noch überlassen → S. 19.	2.1 2.2 2.3 2.4 2.5 2.6
☐ **Mehrfamilienhaus ab drei Wohnungen?** Bei Modernisierung: fertiggestellt vor dem 08.12.2004.	2.1 2.2 2.3 2.4
☐ **Bedarf am Standort?** In sechs Gebietsarten gilt er als gegeben, überall sonst wird er vermutet → S. 18.	2.1 2.2 2.6
☐ **Mindestens 20 % Eigenmittel?** Gerechnet auf die zuwendungsfähigen Kosten; auf den Inseln reichen 10 % der zuwendungsfähigen Herstellungskosten.	2.1 2.2 2.3 2.4
☐ **Grundstück gesichert?** Eigentum, Erbbaurecht oder gesicherter Erwerb.	2.1 2.2 2.4

EINMAL NEIN? Sprechen Sie zuerst mit der Wohnraumförderstelle – es gibt Ausnahmen → S. 21.

VOM VORHABEN ZUM *PASSENDEN* PROGRAMMTEIL

Vier Ausgangslagen führen zu sechs Programmteilen. Den Antrag stellen Sie bei Ihrer kommunalen Wohnraumförderstelle, die NBank bewilligt.

WAS HABEN SIE VOR?

A **Wohnraum im Mehrfamilienhaus neu schaffen oder bis zwei Jahre nach Fertigstellung erstmals erwerben**

Auf Borkum, Norderney, Juist, Wangerooge, Baltrum, Langeoog oder Spiekeroog?

- **Ja** → **Ostfriesische Inseln ▶**

Nein, weiter

Neubau ab EH-40-Niveau, nur Zuschuss gewünscht?

- **Ja** → **Energetisch hochwertiger Neubau ▶**
- **Nein** → **Neubau, Änderung und Erweiterung, Ersterwerb ▶**

B **Bestand klimagerecht modernisieren**

Mehrfamilienhaus vor dem 08.12.2004 fertiggestellt und nach der Modernisierung mindestens zwei Energieeffizienzklassen besser (ausnahmsweise eine, wenn die NBank das zulässt)?

- **Ja** → **Klimagerechte Modernisierung ▶**

C **Freie Bestandswohnung für Gruppe A binden**

Frei, ungebunden, vor der Bewilligung weder vermietet noch überlassen?

- **Ja** → **Belegungsbindungen erwerben ▶**

D **Auslaufende Landesbindung verlängern**

Bindung aus Landesförderung nach altem Recht läuft planmäßig aus, NBank-Darlehen läuft noch?

- **Ja** → **Auslaufende Bindungen verlängern ▶**

DIE SECHS PROGRAMMTEILE AUF EINEN BLICK

S. 13 — 2.4
Instrument **Darlehen + Zuschuss**
Bis zu zusammen 90 % der Herstellungskosten + 100 % der Grundstückskosten Bindung 35 Jahre
Eigenmittel mind. 10 % der zuwendungsfähigen Herstellungskosten

2.2 — S. 12
Instrument **nur Zuschuss**
Bis zu A 50 · B 40 · C 30 %, max. 90.000/75.000/60.000 € je Wohnung Bindung 35 Jahre
Eigenmittel mind. 20 %
Nicht mit 2.1 kombinierbar

2.1 — S. 8
Instrument **Darlehen + Zuschuss (Zuschuss nur mit Darlehen)**
Bis zu zusammen 80 %: A 40 + 40 · B 60 + 20 · C 70 + 10 % Bindung 35 Jahre
Eigenmittel mind. 20 %

2.3 — S. 14
Instrument **Zuschuss je gebundener Wohnung**
Bis zu 10–40 %, höchstens 9.000–31.000 €
Bindung 25 Jahre; vermietete Wohnungen ohne WBS-Nachweis 35 Jahre Eigenmittel mind. 20 %
Wahlrecht bis 31.12.2026 → S. 15

2.5 — S. 16
Instrument **Zuschuss**
Festbetrag 2,00–3,00 € je m² und Monat, nach Bindungsdauer gestaffelt Bindung 5–20 Jahre

S. 17 — 2.6
Instrument **Zuschuss zur Zinsverbilligung**
Zins 0 % auf bis zu 100 % der Restschuld, längstens 20 Jahre Bindung + bis zu 20 Jahre
Antrag erst nach Prolongationsangebot der NBank

ERST BEWILLIGUNG, DANN VERTRAG ODER SPATENSTICH → S. 19

NICHT FÖRDERFÄHIG Ferienwohnungen, Ferien- und Wochenendhäuser ▪ Heime im Sinne des NuWG ▪ Wohnraum für stationäre oder quasistationäre Versorgung ▪ an Pflege- oder Betreuungsvertrag gekoppelter Wohnraum ▪ Gemeinschaftsunterkünfte ▪ Wohnungen ohne Bindung ▪ Eigentumswohnungen zur Vermietung (2.1, 2.2, 2.4) ▪ Standorte außerhalb Niedersachsens

ERTRAGSSEITE


IHR MIETERKREIS: *DREI* EINKOMMENSGRUPPEN

Grundsatz ist Gruppe A. B und C bringen höhere Mieten, aber weniger Zuschuss – und es gibt sie nur, wenn die NBank sie in der Förderentscheidung zulässt.

OBERGRENZE GESAMTJAHRESEINKOMMEN IN €

A, B und C im Vergleich → S. 11

Einkommensgrenzen seit 01.03.2025 · B = Grenze + 40 %, C = + 60 %

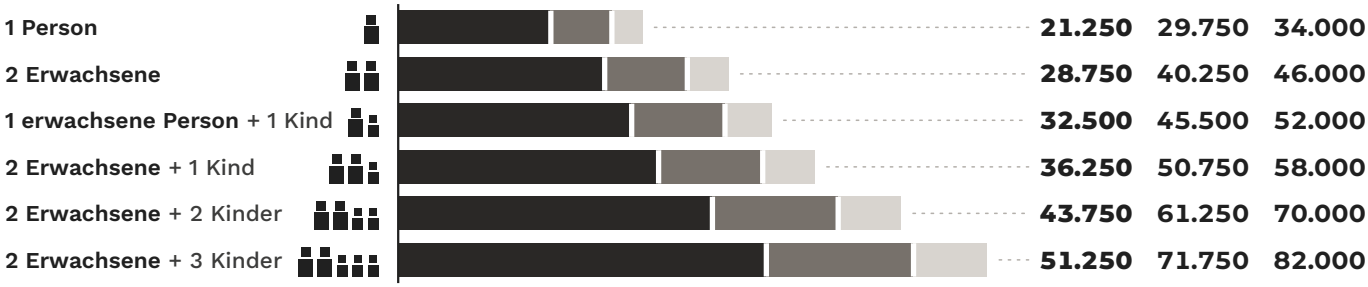

	A	B	C
1 Person	21.250	29.750	34.000
2 Erwachsene	28.750	40.250	46.000
1 erwachsene Person + 1 Kind	32.500	45.500	52.000
2 Erwachsene + 1 Kind	36.250	50.750	58.000
2 Erwachsene + 2 Kinder	43.750	61.250	70.000
2 Erwachsene + 3 Kinder	51.250	71.750	82.000
je weitere Person ab der dritten, zusätzlich je Kind	**+3.750**	**+5.250**	**+6.000**

WANN B UND C MÖGLICH SIND

bis +60 % in Gebieten mit kommunalem Wohnraumversorgungs- oder städtebaulichem Entwicklungskonzept, mit kommunaler Festlegung von gefördertem Wohnraum (Bebauungsplan, städtebaulicher Vertrag, Baulandmodell), mit Gemeindeverordnung zu erhöhtem Wohnungsbedarf oder mit per Verordnung bestimmtem angespanntem Wohnungsmarkt – oder für Wohnraum, der Älteren, Menschen mit Behinderungen oder Hilfe- und Pflegebedürftigen vorbehalten ist

sonst nur bis +20 % also nur ein Teil von B, kein C – und nur ab 12 zusammenhängenden Wohnungen, für höchstens die Hälfte davon

ANGEMESSENE WOHNFLÄCHE

Personen	bis m²
1	50
2	60
3	75
4	85
je weitere	+10

Rollstuhlgerecht nach DIN 18040-2 „R“: +12 m², mit Freisitz stattdessen +15 m². Wohnungen sollen mindestens 30 m² groß sein.

NACHWEIS

Mieterinnen und Mieter weisen ihre Gruppe mit dem Wohnberechtigungsschein (WBS) nach. Ihn stellt die Kommune aus, meist Landkreis oder Stadt; der allgemeine WBS gilt ein Jahr und legt auch die angemessene Wohnungsgröße fest.

Die Grenzen in der Grafik meinen nicht das Brutto. Ausgangspunkt ist das in den zwölf Monaten ab Antragstellung erwartete Einkommen aller Haushaltsmitglieder. Davon gehen je 10 % ab, wenn Steuern, Kranken-/Pflege- oder Rentenbeiträge gezahlt werden, dazu Freibeträge und Unterhalt. Das Bruttoeinkommen kann daher deutlich höher liegen.

> *„Der Mangel an bezahlbarem Wohnraum ist längst in der Mitte unserer Gesellschaft angekommen – er betrifft nicht mehr nur wenige, sondern viele. Umso wichtiger ist es, dass die neuen Richtlinien den Kreis der Berechtigten spürbar erweitern. So öffnet sich eine Tür für all jene, die bisher knapp durchs Raster gefallen sind.“*
>
> **MICHAEL KIESEWETTER**
> Vorstandsvorsitzender der NBank
> Pressemitteilung MW vom 03.07.2026

MIETEN: GEDECKELT, ABER *PLANBAR*

Was Sie verlangen dürfen, bestimmen Programmteil, Einkommensgruppe und Mietenstufe. Drei Jahre bleibt die Miete fest, danach darf sie nach klaren Regeln steigen.

HÖCHSTMIETE NETTOKALT,

€ je m² und Monat, Jahre 1–3


PROGRAMMTEIL	MIETENSTUFE	A	B	C
2.1 · 2.3	I–III	6,50	7,90	8,70
	IV–VII	6,80	8,20	9,00
2.5 (nur A)	I–III	6,50	–	–
	IV–VII	6,80	–	–
2.2	I–III	6,80	8,20	9,00
	IV–VII	7,10	8,50	9,30
2.4	alle	9,50	11,50	12,50
2.6	alle	bisherige Miete, drei Jahre ab Verlängerung eingefroren, auch bei Wiedervermietung		

Ab EH-40-Niveau bis zu +0,30 € (2.1, 2.3, 2.5); in 2.2 enthalten. 2.3 mit verlängerter Bindung: Jahre 1–3 ab der ersten WBS-Belegung → S. 14.

MIETPFAD UND MARKT,

€ je m² nettokalt

Programmteil 2.1 · Gruppe A · Mietenstufe IV–VII

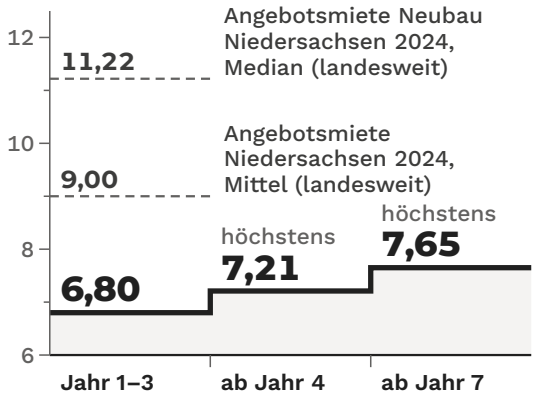

Ab Jahr 4 höchstens +6,15 % in drei Jahren, auch bei Wiedervermietung; keine Staffel- oder Indexmiete.

KALKULATIONSNOTIZ

Kalkulieren Sie mit dem Mietpfad, nicht mit der Marktmiete: Selbst nach zwei Erhöhungen liegt die Fördermiete mit höchstens 7,65 € unter dem Landesmittel 2024 von 9,00 €.

MIETENSTUFE

Die Mietenstufe Ihrer Gemeinde bestimmt Höchstmiete und Bemessungsgrenze.

VI	Buchholz i. d. Nordheide, Neu Wulmstorf
V	Hannover, Buxtehude, Seevetal, die sieben Inselgemeinden
IV	Adendorf, Braunschweig, Garbsen, Göttingen, Hemmingen, Jork, Laatzen, Langenhagen, Lüneburg, Oldenburg (Oldb), Osnabrück, Ronnenberg, Rosengarten, Stade, Stelle, Winsen (Luhe), Wolfsburg
I–III	übrige Festlandgemeinden

Stufe VII gibt es in Niedersachsen nicht. Zuordnung nach Wohngeldrecht seit 2023; neue Stufen sind ab 2027 geplant → S. 15.

SPIELREGELN

- ✓ nur an Haushalte mit WBS, auch bei Wiedervermietung
- ✓ unbefristeter Mietvertrag, der die Förderbestimmungen zur Mietbindung wiedergibt; Wohnung bezugsfertig übergeben
- ✓ Stellplätze getrennt vermietbar, nicht an die Wohnung gekoppelt
- ✗ keine Zuschläge (Ausstattung, Keller, Energie- und Wärmeeinrichtungen); Zusatzleistungen nur freiwillig
- ✗ keine Abwälzung von Kosten für Bezugsfertigkeit oder Instandhaltung über das BGB-Mietrecht hinaus
- ✗ keine Zwischenvermietung (Ausnahmen, z. B. Housing First → S. 8)
- ! Verstöße (ohne WBS, überhöhte Miete) kosten Geldleistungen bis 5 € je m² und Monat und Bußgeld bis 10.000 €; bei Vermietung ohne WBS drohen Kündigung und Räumung, die Förderung kann zurückgefordert werden.

2.1

PROGRAMMTEIL

Zuschuss + Darlehen

NEUBAU, ÄNDERUNG, ERSTERWERB

BIS ZU *80 %* FÖRDERQUOTE

DARLEHEN PLUS ZUSCHUSS IN JEDER EINKOMMENSGRUPPE – MIT ZUSCHLAG BIS ZU **90 %**

Für gebundene Mietwohnungen in Mehrfamilienhäusern ab drei Wohnungen. Drei Wege: Neubau, Änderung und Erweiterung – Dachausbau, Aufstockung, Anbau, Umnutzung – sowie der Ersterwerb unvermieteter, ungebundener Wohnungen bis zwei Jahre nach Fertigstellung, höchstens zum Marktwert. **Den Zuschuss gibt es nur mit dem Darlehen.**

FÖRDERMIX

Höchstsätze in % der zuwendungsfähigen Kosten


Eigenmittel, mind.

Zuschlag +5 / +10

Regelfall Gruppe A; B und C mit Zulassung in der Förderentscheidung

Bindung 35 Jahre

Konditionen → S. 9

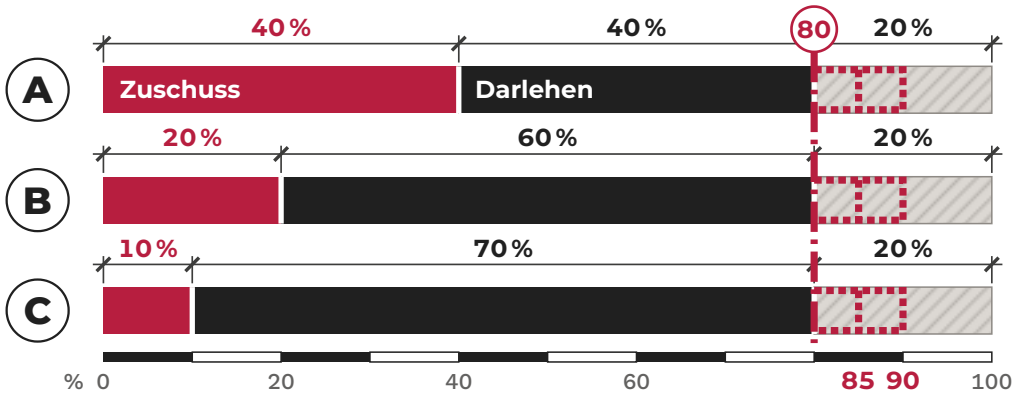

WAS ZÄHLT

Herstellungskosten (Kostengruppen 200–700 nach DIN 276)
höchstens Bemessungsgrenze × Wohnfläche

\+ **Grundstückskosten (Kostengruppe 100)**
in der Regel höchstens Bodenrichtwert bei Antragstellung × Grundstücksfläche

= **zuwendungsfähige Kosten**
nur für den geförderten Wohnraum. Beim Ersterwerb: Kaufpreis + Erwerbskosten.

BEMESSUNGSGRENZE **4.800 €** je m² Wohnfläche in Mietenstufe I–III, **5.000 €** in IV–VII – Ausgangswerte, fortgeschrieben zum 01.04. und 01.10.; aktueller Wert auf nbank.de.

EIGENMITTEL **mindestens 20 %**, mit Zuschlag entsprechend weniger; mindestens die Hälfte als Geld oder lastenfreies Grundstück.

ZUSCHLÄGE UND SONDERFORMEN

HOUSING FIRST Zuschuss bis zu +10 Prozentpunkte

Gruppe A: 50 %, zusammen 90 %. Bedingungslose Wohnangebote für wohnungslose Menschen, in verbindlicher Zusammenarbeit mit der Wohnungslosenhilfe (§§ 67 ff. SGB XII); Zwischenvermietung an gemeinnützige Träger möglich.

MODELLPROJEKT Zuschuss bis zu +5 Prozentpunkte

Für übertragbare neue Konzepte, etwa serielles oder modulares Bauen, flexible Grundrisse oder weniger Wohnfläche je Kopf. Sie liefern Daten und informieren die Öffentlichkeit.

GEMEINSCHAFTLICHE WOHNFORMEN

Cluster-Wohnung, Wohngemeinschaft oder Wohngruppe, in der Regel höchstens 40 m² je Person inklusive Gemeinschaftsflächen.


KOMBINIERBAR Je Wohnung ein KfW-Kredit, **298 oder 296** (Neubau; Ersterwerb bis zwölf Monate nach Bauabnahme), zusammen höchstens bis zu den förderfähigen KfW-Kosten. Die EH-55-Stufe der 298 nur bei KfW-Antrag bis 31.12.2026. **Nicht kombinierbar mit Programmteil 2.2**

TERM SHEET · PROGRAMMTEIL 2.1

KONDITIONEN AUF *EINEM BLATT*

Zinsfrei ist nicht kostenfrei: **0,5 % Verwaltungskostenbeitrag p. a.** und einmalige Entgelte gehören in den Finanzplan.

DARLEHEN UND BINDUNG IM ZEITVERLAUF

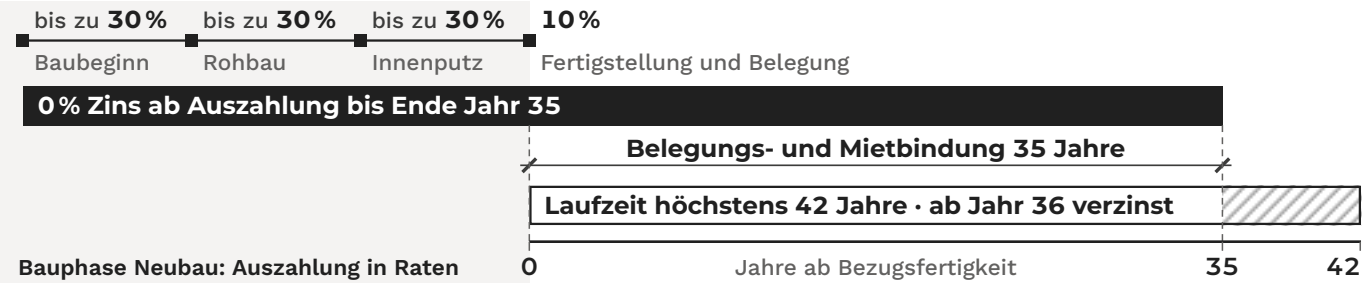

Ersterwerb: Laufzeit und Bindung ab Eigentumsübergang; 0 % Zins bis Ende Jahr 35 nach Bezugsfertigkeit.


POSITION	KONDITION
ANTRAG, BEWILLIGUNG	Antrag bei der Wohnraumförderstelle am Bauort; die NBank bewilligt und schließt mit Ihnen einen öffentlich-rechtlichen Fördervertrag
SÄTZE (HÖCHSTWERTE)	Darlehen **40/60/70 %** plus Zuschuss **40/20/10 %** (Gruppe A/B/C), zusammen **80 %** der zuwendungsfähigen Kosten; Zuschuss nur mit Darlehen, B und C nur mit Zulassung. Zuschlag auf den Zuschuss: Modellprojekt +5, Housing First +10 Prozentpunkte → S. 8
EIGENMITTEL	**mindestens 20 %** der zuwendungsfähigen Kosten, mit Zuschlag entsprechend weniger; mindestens die Hälfte als Geld oder lastenfreies Grundstück
ZINS	**0 %** bis Ende des 35. Jahres nach Bezugsfertigkeit; danach bis zu 3 Prozentpunkte über dem Basiszinssatz, höchstens marktüblich
TILGUNG	Satz legt die NBank fest; Beginn nach vollständiger Auszahlung, spätestens zwei Jahre nach dem auf die Bekanntgabe folgenden Monat – also in der zinsfreien Zeit → S. 21
KOSTEN, LAUFEND	Verwaltungskostenbeitrag **0,5 % p. a.** auf das Restkapital, ab Auszahlungsbeginn
KOSTEN, EINMALIG	Bearbeitungsentgelt **1 %** des bewilligten Darlehens und **0,75 %** des bewilligten Zuschusses, jeweils mit der ersten Auszahlung verrechnet
AUSZAHLUNG	in Raten nach Baufortschritt (Neubau: Zeitstrahl oben); Darlehen und Zuschuss je Rate anteilig, Ihre Eigenmittel in der Regel zuerst
SICHERHEITEN	nachrangige Grundschuld direkt nach den Kapitalmarktmitteln; Details → S. 21
VERSICHERUNG	Brand ab Baubeginn, Sturm ab Bezugsfertigkeit, jeweils gleitender Neuwert, bis zur vollständigen Rückzahlung
EXIT	Freiwillige vorzeitige Volltilgung: Zuschuss anteilig für die restliche Bindungszeit zurück; die Bindung endet frühestens **20 Jahre** nach Bindungsbeginn → S. 21
BEIHILFERECHT	Die NBank prüft jede Förderung auf Überkompensation. Eine Eigenkapitalrendite bis 1 Prozentpunkt über dem 30-jährigen Swapsatz gilt stets als angemessen.

MODELLRECHNUNG – fiktives Beispiel, keine Förderzusage

20 WOHNUNGEN, 7,0 MIO. €: BIS ZU *5,6 MIO. €* FÖRDERUNG

2.1

FINANZIERUNG 7,0 MIO. €, HÖCHSTSÄTZE

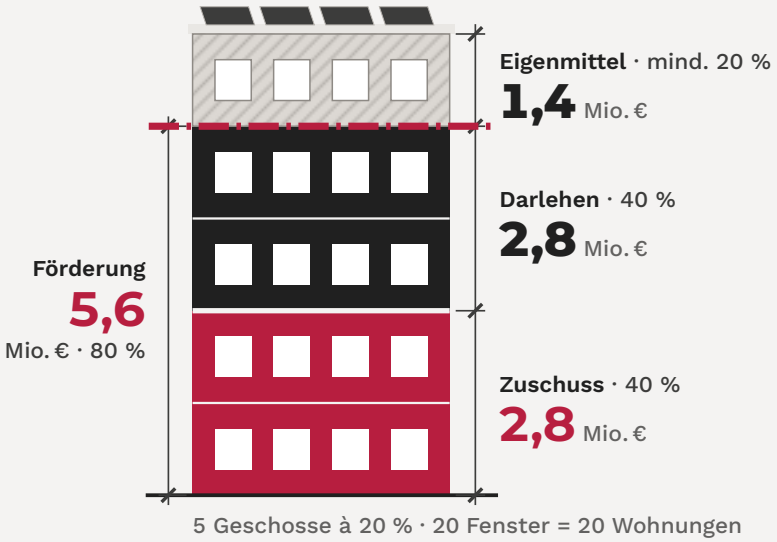

5 Geschosse à 20 % · 20 Fenster = 20 Wohnungen

DAS MODELLHAUS

20 Neubauwohnungen nach Programmteil 2.1 (2 × 50, 6 × 60, 8 × 75, 4 × 85 m²) – jeweils die angemessene Höchstgröße für ein bis vier Personen –, zusammen 1.400 m² Wohnfläche, alle für Einkommensgruppe A. Standort: eine Gemeinde der Mietenstufe IV–VII, per Verordnung angespannter Wohnungsmarkt – der Bedarf gilt als gegeben. Herstellungskosten 4.500 € je m², also 500 € unter dem Ausgangswert der Bemessungsgrenze von 5.000 € und damit voll zuwendungsfähig. Grundstück 700.000 €, unter Bodenrichtwert × Grundstücksfläche.


RECHENWEG

	POSITION	€
1	Herstellungskosten, 1.400 m² × 4.500 €	6.300.000
2	+ Grundstück	700.000
3	= **zuwendungsfähige Gesamtkosten**	7.000.000
4	Eigenmittel, mindestens 20 %; davon sollen mindestens 700.000 € Geld oder lastenfreies Grundstück sein	1.400.000

BIS ZU
140.000 €
Ø Zuschuss je Wohnung im Modellhaus
plus Darlehen in gleicher Höhe

BIS ZU
4 €
Förderung je 1 € Mindest-Eigenmittel
davon 2 € Darlehen

SENSITIVITÄT: HERSTELLUNGSKOSTEN 5.200 € JE m²

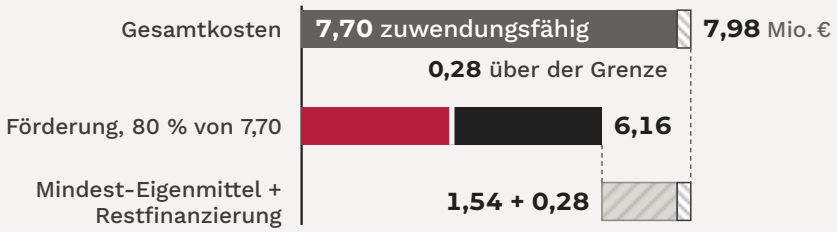

BIS ZU
77,2 %
Förderquote auf die Gesamtkosten

KALKULATIONSNOTIZ Die 80 % gelten nur bis zur Bemessungsgrenze – jeden Euro darüber finanzieren Sie ohne Förderung.

Was davon im Betrieb bleibt: rechts →


MEHR MIETE, MEHR DARLEHEN: *WAS BLEIBT IM JAHR?*

Dasselbe Haus wie links, immer 80 % Förderung, nur anders gemischt: Von A nach C wird Zuschuss zu Darlehen – und die Höchstmiete steigt. B und C setzen eine Zulassung in der Förderentscheidung voraus (→ S. 6); im Modell ist sie möglich, weil der Standort per Verordnung als angespannter Wohnungsmarkt gilt.

Darlehen · Zuschuss · Eigenmittel, mind. · Förderung, bis zu 80 %

FINANZIERUNG IN MIO. €

Gesamtkosten je 7,0 Mio. € · Höchstwerte

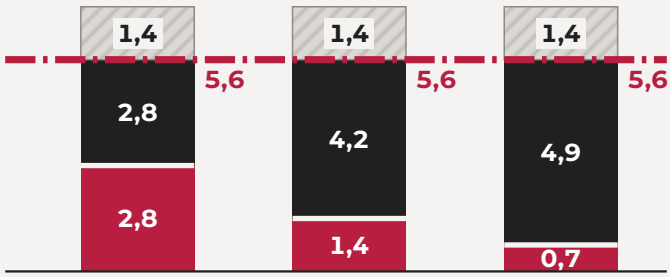

JAHRESRECHNUNG JAHRE 1–3, IN € P. A.

	POSITION	A	B	C
1	Höchstmiete nettokalt, Mietenstufe IV–VII (1.400 m² × 6,80 | 8,20 | 9,00 € × 12)	114.240	137.760	151.200
2	– Mietausfallwagnis [PGN-Rechnung: … % der Miete]	[PGN-Rechnung]	[PGN-Rechnung]	[PGN-Rechnung]
3	– nicht umlagefähige Bewirtschaftungskosten [PGN-Rechnung: … € je Wohnung p. a.]	[PGN-Rechnung]	[PGN-Rechnung]	[PGN-Rechnung]
4	– Instandhaltung [PGN-Rechnung: … € je m² p. a.]	[PGN-Rechnung]	[PGN-Rechnung]	[PGN-Rechnung]
5	= **Überschuss vor Kapitaldienst**	[PGN-Rechnung]	[PGN-Rechnung]	[PGN-Rechnung]
6	– Verwaltungskostenbeitrag, 0,5 % des Restkapitals (Jahr 1, nach Vollauszahlung)	14.000	21.000	24.500
7	– Zins NBank-Darlehen, 0 % bis Ende Jahr 35	0	0	0
8	– Tilgung [PGN-Rechnung: Tilgungssatz … %] auf 2,8 | 4,2 | 4,9 Mio. € Darlehen	[PGN-Rechnung]	[PGN-Rechnung]	[PGN-Rechnung]
9	= **Zahlungsüberschuss p. a.**	[PGN-Rechnung]	[PGN-Rechnung]	[PGN-Rechnung]
	Einmalig, außerhalb der Jahresrechnung: Bearbeitungsentgelte (1 % des Darlehens + 0,75 % des Zuschusses)	49.000	52.500	54.250

KALKULATIONSNOTIZ

1,26 % **2,1 Mio. € × 1,26 % = 26.460 €**

Tilgungssatz auf die Mehrschuld, ab dem C gegenüber A keinen Liquiditätsvorteil mehr bringt

C bringt gegenüber A 36.960 € mehr Jahresmiete, kostet aber 10.500 € mehr Verwaltungskostenbeitrag – die übrigen 26.460 € zehrt die Tilgung der 2,1 Mio. € Mehrschuld ab 1,26 % auf (B: 16.520 €, Schwelle 1,18 % auf 1,4 Mio. €).

SO LESEN SIE DIE RECHNUNG

Bewirtschaftung und Instandhaltung sind in A, B und C gleich – sie verschieben das Niveau, nicht den Vergleich. Nur das Mietausfallwagnis wächst mit der Miete und senkt die Tilgungsschwellen von 1,26 % (C) und 1,18 % (B). Die Rechnung zeigt Liquidität bei festen Höchstmieten, keine Rendite; Mischungen aus A, B und C liegen dazwischen. Den Tilgungssatz legt die NBank fest (→ S. 9).

Wir rechnen Ihr Projekt mit Ihnen durch – mit Ihren Kosten und Ihrem Standort.

2.2

PROGRAMMTEIL

Zuschuss

ENERGETISCH HOCHWERTIGER NEUBAU

REINER *ZUSCHUSS* STATT DARLEHEN

BIS ZU **50 %** DER ZUWENDUNGSFÄHIGEN KOSTEN, HÖCHSTENS **90.000 €** JE WOHNUNG (GRUPPE A)


Wer ab KfW-Effizienzhaus-40-Niveau neu baut, erhält einen reinen Zuschuss – ohne Darlehen, also ohne Verwaltungskostenbeitrag. Es gilt der niedrigere Wert aus Satz und Höchstbetrag. **2.2 lässt sich nicht mit 2.1 und nicht mit anderen Förderdarlehen der Richtlinie kombinieren.**

Das Haus von S. 10 (350.000 € je Wohnung) bekäme als EH-40-Bau **1,8 Mio. € Zuschuss** – aus 2.1 dagegen **2,8 Mio. € Zuschuss plus 2,8 Mio. € Darlehen.**

2.2 bringt mehr Zuschuss als 2.1, solange die zuwendungsfähigen Kosten je Wohnung unter **225.000 € (A), 375.000 € (B) bzw. 600.000 € (C)** liegen.

ZUSCHUSS JE WOHNUNG NACH KOSTEN JE WOHNUNG

Höchstsätze · B und C nur mit Zulassung (→ S. 6)

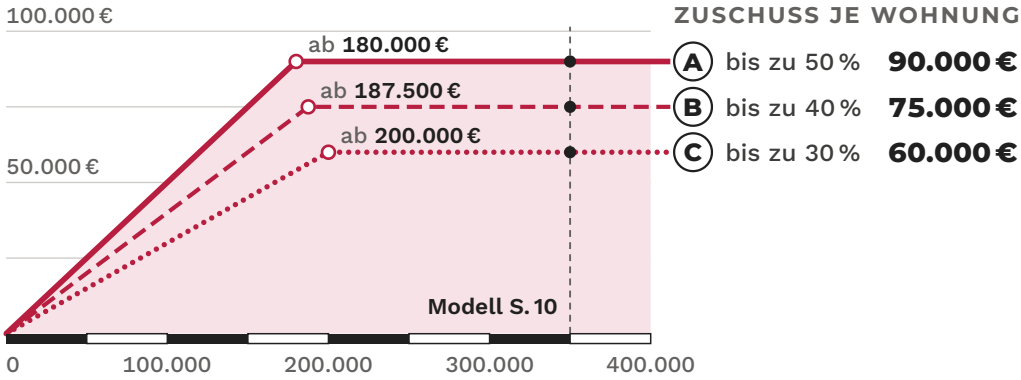

KOMBINIERBAR MIT **KfW 298 (Kommunen: 498) oder 296**, je Wohnung eines (→ S. 8). Für die KfW-Stufe „Klimafreundliches Wohngebäude“ reicht EH 40 allein nicht, die KfW verlangt zusätzlich Lebenszyklus-Anforderungen; EH 55 nur bei KfW-Antrag bis 31.12.2026. Alle Förderungen zusammen dürfen die förderfähigen KfW-Kosten ohne Grundstück nicht übersteigen.

SPIELREGELN

- **Höchstmiete Jahre 1–3:** 6,80–9,30 € je m² nettokalt je nach Gruppe und Mietenstufe, EH-40-Aufschlag enthalten (→ S. 7); danach höchstens +6,15 % in drei Jahren
- **Bindung 35 Jahre** ab Bezugsfertigkeit, grundsätzlich per Dienstbarkeit im Grundbuch gesichert
- **Auszahlung in vier Raten** nach Baufortschritt (→ S. 9); Bearbeitungsentgelt 0,75 % (675 € bei 90.000 €)

VORAUSSETZUNGEN

- **nur Neubau**
- **gemeinschaftliche Wohnformen** möglich; keine Zuschläge für Housing First oder Modellprojekte
- **wie 2.1:** Bedarf, gesichertes Grundstück, mindestens zwei gebundene Wohnungen je Neubau, Eigenmittel mindestens 20 %
- **EH-40-Nachweis** mit der Fertigstellungsanzeige, ausgestellt von Fachleuten mit Energieausweis-Berechtigung oder aus der Energieeffizienz-Expertenliste; bei KfW-Mitfinanzierung genügt die KfW-Bescheinigung
- **Brand- und Sturmversicherung** bis Bindungsende

OSTFRIESISCHE INSELN

HÖHERE KOSTENGRENZE, *10 %* EIGENMITTEL

2.4

PROGRAMMTEIL

Zuschuss + Darlehen


BIS ZU **90 %** DER GEDECKELTEN HERSTELLUNGSKOSTEN, BIS ZU **100 %** DER ZUWENDUNGSFÄHIGEN GRUNDSTÜCKSKOSTEN

Sie bauen neu, ändern oder erweitern ein Gebäude oder kaufen Neubauwohnungen als Ersterwerb bis zwei Jahre nach Fertigstellung – gefördert werden gebundene Mietwohnungen in Mehrfamilienhäusern auf allen sieben bewohnten Ostfriesischen Inseln. **Einen Bedarfsnachweis brauchen Sie nicht.**

FINANZIERUNG JE m² WOHNFLÄCHE, KOSTEN AM DECKEL

MODELLRECHNUNG

Höchstsätze · B und C nur mit Zulassung (→ S. 6)

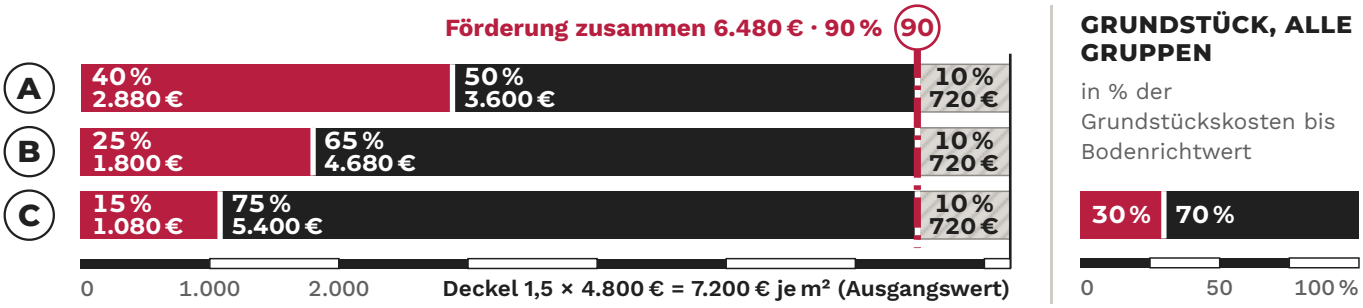

GRUNDSTÜCK, ALLE GRUPPEN

in % der Grundstückskosten bis Bodenrichtwert

Deckel: das 1,5-Fache der Bemessungsgrenze für Mietenstufe I–III (→ S. 8), unabhängig von der Mietenstufe der Insel. Eigenmittel: mindestens 10 % der zuwendungsfähigen Herstellungskosten; mindestens die Hälfte davon soll Geld oder lastenfreies Grundstück sein.

Nettokaltmiete je m² und Monat, Jahre 1–3, unabhängig von der Mietenstufe; danach höchstens +6,15 % in drei Jahren.

HÖCHSTENS	HÖCHSTENS	HÖCHSTENS
9,50 €	**11,50 €**	**12,50 €**
Einkommensgruppe A	Einkommensgruppe B	Einkommensgruppe C

DARLEHEN WIE IN 2.1

Zuschuss nur mit Darlehen. Es gelten die Konditionen von 2.1 (→ S. 9): 0 % Zins bis Ende Jahr 35, 0,5 % Verwaltungskostenbeitrag p. a., einmalig 1 % (Darlehen) bzw. 0,75 % (Zuschuss) Bearbeitungsentgelt, **35 Jahre** Bindung – beim Ersterwerb ab Eigentumsübergang. Wenig Eigenmittel heißt viel Darlehen: Planen Sie Tilgung und Verwaltungskostenbeitrag fest ein.

VORAUSSETZUNGEN UND KOMBINATION

- **Eigentum oder Erbbaurecht** (mindestens 60 Jahre); gesicherter Erwerb genügt
- je neuem Gebäude **mindestens zwei gebundene Mietwohnungen**
- **nicht gefördert:** Ferienwohnungen, Ferien- und Wochenendhäuser, zur Vermietung bestimmte Eigentumswohnungen
- Neubau und Ersterwerb bis zwölf Monate nach Bauabnahme: **kombinierbar mit KfW 298 oder 296** wie in 2.1 (→ S. 8); Kommunen selbst: KfW 498



2.3

PROGRAMMTEIL

Zuschuss

KLIMAGERECHTE MODERNISIERUNG


ZUSCHUSS NACH *KLASSENSPRUNG*

Bis zu **40 %** der Modernisierungskosten, höchstens **31.000 €** je gebundener Wohnung (Einkommensgruppe A, ab 5 Klassen)

Reiner Zuschuss, kein Bedarfsnachweis: für Mietwohnungen in Mehrfamilienhäusern ab drei Wohnungen, fertiggestellt vor dem 08.12.2004.

EFFIZIENZKLASSEN

Endenergiebedarf in kWh je m² Gebäudenutzfläche und Jahr

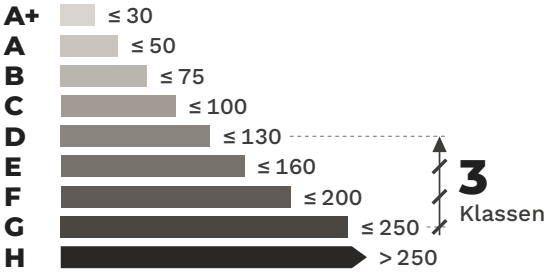

Mindestens 2 Klassen besser, belegt per Energiebedarfsausweis vor Bewilligung und bei Fertigstellung.

Ausnahme, etwa beim Baudenkmal: Ist das unverhältnismäßig aufwendig, kann die NBank eine Klasse zulassen (gefördert wie zwei Klassen). **Mitgefördert:** Barrierefreiheit, Bleileitungstausch, unmittelbar zugehörige Instandsetzung.

ZUSCHUSS JE GEBUNDENER WOHNUNG, HÖCHSTSÄTZE

in % der Modernisierungskosten · Kostengruppen 300–700 nach DIN 276

	A	B	C
2 Klassen	**25 %** max. 25.000 € ab 100.000 €	**20 %** max. 17.000 € ab 85.000 €	**10 %** max. 9.000 € ab 90.000 €
3 Klassen	**30 %** max. 27.000 € ab 90.000 €	**25 %** max. 19.000 € ab 76.000 €	**15 %** max. 11.000 € ab 73.400 €
4 Klassen	**35 %** max. 29.000 € ab 82.900 €	**30 %** max. 21.000 € ab 70.000 €	**20 %** max. 13.000 € ab 65.000 €
ab 5 Klassen	**40 %** max. 31.000 € ab 77.500 €	**35 %** max. 23.000 € ab 65.800 €	**25 %** max. 15.000 € ab 60.000 €

Satz · **Höchstbetrag** · ab … € Kosten je Wohnung gilt der Höchstbetrag

BINDUNG UND MIETE

- **25 Jahre ab Abschluss**, grundsätzlich per Dienstbarkeit im Grundbuch gesichert; bei Mieterwechsel nur an WBS-Haushalte
- Ist die Wohnung vermietet, **verlängert sich die Bindung um 10 Jahre** – außer der Haushalt hat einen WBS. Dann passen Sie den Mietvertrag umgehend an Höchstmiete und Erhöhungsregeln an.
- **Höchstmieten wie in 2.1** (→ S. 7): 6,50–9,00 € je m², ab EH-40-Niveau bis zu +0,30 €. Drei Jahre keine Mieterhöhung; bei verlängerter Bindung beginnen die drei Jahre erst mit dem ersten WBS-Haushalt.

ABLAUF UND KOMBINATION

Auszahlung in drei Raten: bis zu 30 % nach Baubeginn, 60 % gegen Kostennachweis, 10 % nach Abschluss. **Bearbeitungsentgelt:** einmalig 0,75 % des Zuschusses. **Eigenmittel:** mindestens 20 % der förderfähigen Kosten, in der Regel mindestens die Hälfte als Geld.

Zusätzlich nutzbar: BEG Wohngebäude (KfW 261) oder BEG Einzelmaßnahmen – eines von beiden, das andere erst drei Jahre später. Decken öffentliche Mittel samt NBank-Zuschuss mehr als 60 % derselben Kosten, kürzt die BEG (Kommunen bei BEG Einzelmaßnahmen: 90 %).

Antrag bis 31.12.2026 bei der Wohnraumförderstelle: altes Recht verbindlich wählbar (→ S. 15).

Die energetische Gesamtmaßnahme planen wir mit Ihnen – Architektur und Haustechnik aus einem Haus.

STICHTAG 31.12.2026

ALTES RECHT ODER RL 2026: SIE HABEN DIE *WAHL*

Nur für **Modernisierungsanträge** – einmalig, mit dem Antrag

STICHTAGE JUNI 2026 BIS DEZEMBER 2031

30.06.2026
Förderregeln 2024 enden


01.07.2026
RL Mietwohnraum 2026 in Kraft

FRIST

31.12.2026

WAHLRECHT MODERNISIERUNG
Antragseingang bei der Wohnraumförderstelle

Geht Ihr Modernisierungsantrag bis 31.12.2026 bei der Wohnraumförderstelle ein, können Sie darin das alte Recht (Förderregeln 2024) wählen – ausdrücklich, **bindend und später nicht änderbar**. Es gilt dann bis zum Abschluss des Verfahrens. Ohne Wahl gilt die RL 2026; Neubau, Ersterwerb und alle übrigen Vorhaben laufen immer nach RL 2026.

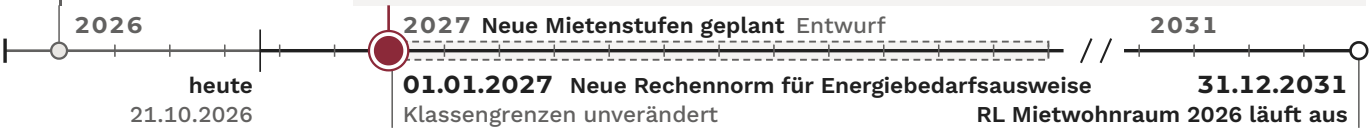

ALTES RECHT UND RL 2026 IM VERGLEICH

	ALTES RECHT	RL 2026 · PROGRAMMTEIL 2.3
Förderart	anfangs zinsloses Darlehen bis zu 75 % der Kosten, max. zwei Drittel eines vergleichbaren Neubaus; 30 % Tilgungsnachlass bei geringen Einkommen	Zuschuss je nach Klassensprung und Einkommensgruppe bis zu 10–40 %, höchstens 9.000–31.000 € je gebundener Wohnung
Zins und Kosten	0 % Zins für 35 Jahre (geringe Einkommen) bzw. 30 Jahre (mittlere), danach marktüblich; 0,5 % Verwaltungskostenbeitrag p. a.	kein Darlehen; 0,75 % Bearbeitungsentgelt
Barrierefreiheit	+5.000 € Zuschuss je barrierefreier Wohnung	Teil der Gesamtmaßnahme, kein Extra-Zuschuss
Höhere Einkommen	mittlere Einkommen: nur energetisch, ohne Tilgungsnachlass	Gruppen B und C mit niedrigeren Sätzen
Kombination	ausgeschlossen, wenn dieselbe Maßnahme nach RL Mietwohnraum, Junges Wohnen oder Wohneigentum 2026 gefördert wird	BEG Wohngebäude (KfW 261) oder BEG Einzelmaßnahmen (→ S. 14)

VIER PRÜFFRAGEN

- ☐ **Fertiggestellt zwischen 01.02.2002 und 07.12.2004?** Dann nur RL 2026: Das alte Recht verlangt Fertigstellung vor dem 01.02.2002.
- ☐ **Zwei Effizienzklassen erreichbar?** Die RL 2026 verlangt sie. Nur wenn das nicht oder nur mit unverhältnismäßigem Aufwand geht, etwa beim Baudenkmal, kann die NBank eine Klasse zulassen (→ S. 14).
- ☐ **Darlehen mit Tilgungsnachlass oder Zuschuss** – was passt zu Ihrer Finanzierung?
- ☐ **Antrag mit ausdrücklicher Wahl bis 31.12.2026** bei der Wohnraumförderstelle?

2.5

PROGRAMMTEIL

Zuschuss

BELEGUNGSBINDUNGEN ERWERBEN

FESTBETRAG FÜR FREIE BESTANDSWOHNUNGEN

ZUSCHUSS **2,00–3,00 €** JE m² WOHNFLÄCHE UND MONAT DER BINDUNG, **5–20 JAHRE**

Sie binden eine freie Bestandswohnung für Haushalte der Einkommensgruppe A und erhalten einen nicht rückzahlbaren Festbetrag – ohne Bau, ohne Darlehen. Der Zuschuss kommt zur gedeckelten Miete hinzu.

MIETE UND BINDUNG

- Bindung ab der ersten Belegung mit einem WBS-Haushalt, grundsätzlich per Dienstbarkeit im Grundbuch gesichert
- Miete Jahre 1–3 höchstens 6,50 € (Mietenstufe I–III) bzw. 6,80 € (IV–VII) je m², ab EH-40-Niveau bis zu +0,30 €
- danach höchstens +6,15 % in drei Jahren; keine Staffel- oder Indexmiete

WER UND WELCHE WOHNUNG

- Sie brauchen Eigentum, Erbbaurecht oder ein vergleichbares langfristiges Nutzungsrecht an der Wohnung.
- Wohnung frei, ungebunden, abgeschlossen, gut erhalten, angemessen groß, mit Mindestausstattung (u. a. Heizung, Bad, Küchenanschluss); die Wohnraumförderstelle besichtigt sie
- Binden Sie die Wohnung für eine besondere Bedarfsgruppe – etwa wohnungslose Menschen, Frauen aus Frauenhäusern oder Haftentlassene –, vermieten Sie ausschließlich an diese Haushalte; mindestens ein volljähriges Haushaltsmitglied weist das per wohnungsbezogenem WBS nach.
- ⛔ **vor der Bewilligung weder Mietvertrag noch Überlassung** – sonst keine Förderung
- Schließt die neue Bindung direkt an eine auslaufende an, greift 2.5 nicht. Für planmäßig auslaufende Landesbindungen mit noch laufendem NBank-Darlehen gibt es **2.6** (→ S. 17).

6,50 €
Miete, höchstens


+ 3,00 €
Zuschuss

BIS ZU
= 9,50 €
je m² und Monat, Jahre 1–3 · Mietenstufe I–III, 15–20 Jahre Bindung

ZUSCHUSS FÜR EINE 60-m²-WOHNUNG

angemessene Größe für zwei Personen

MODELLRECHNUNG

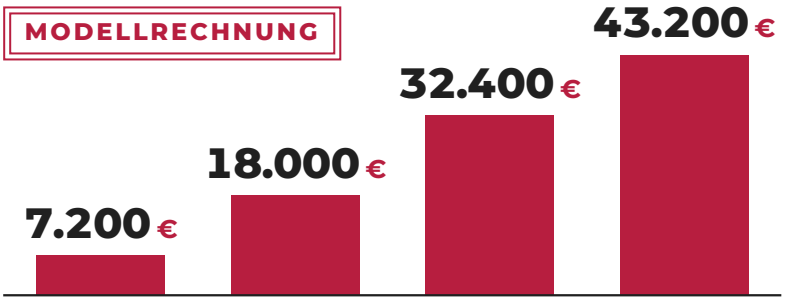


SATZ JE m² UND MONAT

2,00 €	2,50 €	3,00 €	3,00 €

Zwischenlaufzeiten: Satz der erreichten Stufe (12 Jahre: 2,50 €).

AUSZAHLUNG IN ZWEI HÄLFTEN

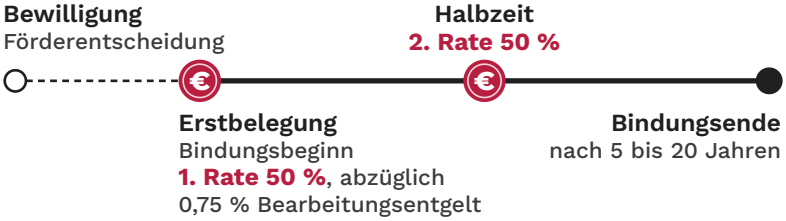

60 m², 20 Jahre: 21.276 € nach Erstbelegung (21.600 € abzüglich 324 € Entgelt), 21.600 € nach 10 Jahren

AUSLAUFENDE BINDUNGEN VERLÄNGERN

BINDUNG VERLÄNGERN, ZINS AUF *0 %*

2.6

PROGRAMMTEIL

☐ Zinsverbilligung

ZINSVERBILLIGUNG FÜR BIS ZU **100 %** DER RESTSCHULD, LÄNGSTENS **20 JAHRE**

Läuft Ihre Belegungs- und Mietbindung planmäßig aus, das NBank-Darlehen aber weiter, kann der Zins auf 0 % sinken. Im Gegenzug verlängert sich die Bindung.


BIS ZU
100 %
der Restschuld zu 0 % Zins
Sie zahlen nur noch Tilgung und Verwaltungskostenbeitrag – kein neues Darlehen, keine Auszahlung

LÄNGSTENS
20 Jahre
Zinsverbilligung
solange das Darlehen läuft

EINMALIG
0,75 %
Bearbeitungsentgelt
auf die bewilligte Zinsverbilligung

ZINS, BINDUNG UND MIETE IM ZEITVERLAUF

Schema, nicht maßstäblich

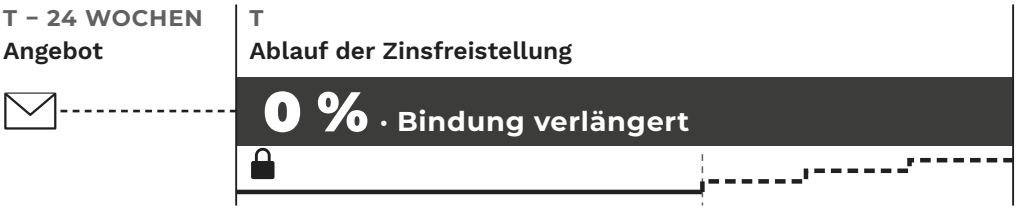

JAHR 1–3
bisherige Nettokaltmiete eingefroren
auch bei Wiedervermietung (→ S. 7)

DANACH
Nettokaltmiete höchstens +6,15 % in drei Jahren
auch bei Wiedervermietung; Betriebskosten ausgenommen; keine Staffel- oder Indexmiete

IN VIER SCHRITTEN ZUR VERLÄNGERUNG

1 **NBANK** — **ANGEBOT** Prolongationsangebot mit Antragsvordruck 1011b, in der Regel 24 Wochen vor Ablauf der Zinsfreistellung

2 **SIE** — **ANTRAG** erst danach, bei der Wohnraumförderstelle am Bauort; sie bestätigt den Bedarf

3 **SIE** — **ANNAHME** angenommenes Angebot direkt an die NBank

4 **NBANK** — **ENTSCHEIDUNG** entscheidet über Zinsverbilligung und Verlängerung der Bindung

VORAUSSETZUNGEN

- Eigentum an der Wohnung und Rückzahlungspflicht für das laufende NBank-Darlehen
- früher vom Land gefördert, Bindung läuft planmäßig aus – bereits ausgelaufene Bindungen und Wohnungen ohne niedersächsische Landesbindung zählen nicht ⊖
- Wohnung abgeschlossen, dauerhaft bewohnbar, gut erhalten, mit Mindestausstattung und angemessener Größe
- Bedarf besteht weiter (→ S. 18)

WO *BEDARF* GILT – UND WAS KOMMUNEN TUN KÖNNEN

SECHS GEBIETSARTEN, **EINE** KARTE, **DREI** HEBEL FÜR KOMMUNEN

Für **2.1**, **2.2** und **2.6** muss am Bauort mehr als nur kurzfristig Bedarf an gebundenen Mietwohnungen bestehen. Modernisierung (**2.3**), Inseln (**2.4**) und Bindungserwerb (**2.5**) brauchen keinen Bedarfsnachweis. Klären Sie den Standort zuerst mit der Wohnraumförderstelle – er entscheidet über Förderfähigkeit, Vorrang und Mieterkreis.

BEDARF GILT ALS ERFÜLLT – VORRANG IN DIESER REIHENFOLGE



Angespannter Wohnungsmarkt
derzeit 57 Kommunen

Erhöhter Wohnungsbedarf
per Verordnung der Gemeinde

Hochschulstandort

Ostfriesische Inseln

Mietenstufe IV–VII
derzeit 29 Gemeinden (→ S. 7)

Kommunale Festlegung
im Bebauungsplan, städtebaulichen Vertrag oder Baulandmodell

Vorrang zählt nur bei knappen Mitteln. Im selben Rang sollen bei sonst gleichen Voraussetzungen kostengünstigere Vorhaben gleicher Güte und Ausstattung vorgehen; danach zählen etwa Barrierefreiheit, Familien mit Kindern und Klimaziele.

BEDARFSLAGE AUF DER NBANK-KARTE

Einheits- und Samtgemeinden



96
Bedarf gesondert nachweisen

306
Bedarf gegeben

AKTUELLE KARTE

Immer nötig: die einfache Bedarfsbestätigung der Wohnraumförderstelle zum Bauort. Zeigt die Karte „gesondert nachweisen“, belegen Sie den Bedarf zusätzlich – etwa mit Wohnraumversorgungskonzept, Marktanalysen, Wartelisten oder Daten der Wohnungsmarktbeobachtung; die NBank entscheidet.

WERKZEUGKASTEN DER KOMMUNE

KONZEPT ODER FESTLEGUNG

Ein Wohnraumversorgungskonzept oder eine kommunale Festlegung (Rang 6) belegt den Bedarf. Dann kann die NBank auch die Gruppen B und C zulassen (→ S. 6; nicht bei 2.5).

§ BEDARFSVERORDNUNG DER GEMEINDE

Per Verordnung legt die Gemeinde für ein Gebiet mit erhöhtem Wohnungsbedarf ein Benennungsrecht fest (Rang 2). Auf Verlangen vermieten Sie dann an einen von mindestens drei benannten wohnberechtigten Haushalten. Genossenschaftlicher Wohnraum lässt sich ausnehmen.

KOMMUNE ALS BAUHERRIN

Auch die Kommune selbst ist antragsberechtigt; für sie gilt zusätzlich das Vergaberecht.


Kein WBS-Haushalt gefunden? Dann können Sie bei der Wohnraumförderstelle eine befristete Freistellung von der Belegungsbindung beantragen – mit Nachweis Ihrer Vermarktung, in der Regel spätestens vier Wochen vor Freiwerden oder Bezugsfertigkeit, für höchstens fünf Jahre, einmal verlängerbar. Die Mietbindung bleibt. Ausgleich: etwa 0,50 € je m² und Monat (nicht auf die Miete umlegbar) oder Belegungsrechte an Ersatzwohnungen.

VOM VORGESPRÄCH BIS ZUM *VERWENDUNGSNACHWEIS*

Sie beantragen bei der Wohnraumförderstelle am Bauort, die NBank entscheidet – in acht Schritten.

ACHT SCHRITTE, DREI BETEILIGTE

Wie wir Sie Station für Station begleiten → S. 20

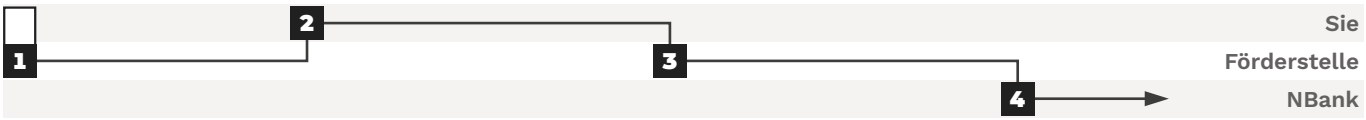

VORGESPRÄCH
Nachweise und Unterlagen vorab klären


ANTRAG
bei der Wohnraumförderstelle am Bauort; für 2.6 erst nach dem Prolongationsangebot (→ S. 17)

STELLUNGNAHME
Bedarfsbestätigung, ggf. Anhörung der Gemeinde, Weiterleitung an die NBank

ENTSCHEIDUNG
Fördervertrag, bei reinem Zuschuss Bewilligungsbescheid

Ziel: höchstens drei Monate

BEI BAUVORHABEN

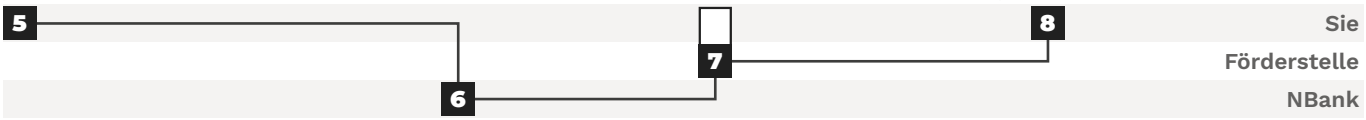

BAUEN
Aufträge im Wettbewerb vergeben, Baubeginn anzeigen (→ S. 21)

Baubeginn unverzüglich, spätestens vier Monate nach Bekanntgabe der Förderentscheidung

AUSZAHLUNG
in Raten auf Ihre Anforderung, nach Baufortschritt (→ S. 9)

FERTIGSTELLUNG
Fertigstellung anzeigen; Vermietung nur mit WBS; letzte 10 % nach Schlussbescheinigung und Belegung

VERWENDUNGSNACHWEIS
an die Wohnraumförderstelle; ein einfacher Nachweis genügt

innerhalb von sechs Monaten nach Erfüllung des Förderzwecks

ERST BEWILLIGUNG, DANN VERTRAG

Wer vor der Bewilligung einen Bau-, Liefer- oder Kaufvertrag unterschreibt – außer für das Baugrundstück – oder den ersten Spatenstich setzt, verliert die ganze Förderung. Bewilligt ist Ihr Vorhaben erst mit Fördervertrag oder Bescheid der NBank.

WAS IST VOR DER BEWILLIGUNG ERLAUBT?

✔ ERLAUBT

- Baugrundstück kaufen oder Erbbaurecht bestellen
- nicht bindende Reservierung beim Kauf
- Planung bis einschließlich Leistungsphase 6 HOAI
- Baugrund untersuchen, Grundstück herrichten

! GENAU PRÜFEN

- Vertrag mit eindeutigem, folgenlosem Rücktrittsrecht oder eindeutiger Bedingung für den Fall, dass die Förderung ausbleibt
- vorzeitiger Vorhabenbeginn auf Antrag (→ S. 21)

✕ FÖRDERSCHÄDLICH

- Bau-, Werk-, Liefer-, Leistungs- oder Kaufvertrag (außer Baugrundstück)
- beim Ersterwerb: bindender Kaufvertrag über die Wohnungen
- Beauftragung ab Leistungsphase 7 HOAI
- erster Spatenstich
- bei 2.5: Mietvertrag oder Überlassung der Wohnung

MIT PGN

SO BEGLEITEN WIR IHR *FÖRDERPROJEKT*

EIN ANSPRECHPARTNER FÜR ALLES –
VON DER ERSTEN IDEE BIS ZUR OBJEKTÜBERGABE.

Wir achten darauf, dass Planung, Kosten und Unterlagen zu den Förderregeln passen – und dass kein Vertrag zu früh unterschrieben wird. Antrag und Entscheidung liegen bei Wohnraumförderstelle und NBank (→ S. 19).

Vor dem Vorgespräch	1	**FÖRDERUNG UND MACHBARKEIT** Wir klären Programmteil, Standort und Mieterkreis – und rechnen, ob die Miete Finanzierung und Bewirtschaftung trägt (→ S. 11).
Leistungsphasen 1–4	2	**PLANUNG NACH FÖRDERREGELN** Wir planen angemessene Wohnungsgrößen (→ S. 6), Freisitze bis zu einem Zehntel davon – auf Wunsch rollstuhlgerecht oder auf EH-40-Niveau.
Leistungsphasen 2–3, dann laufend	3	**KOSTEN IM GRIFF** Wir steuern die Herstellungskosten mit Blick auf die Bemessungsgrenze; was darüber liegt, finanzieren Sie ohne Förderung (→ S. 8).
Vorgespräch und Antrag	4	**ANTRAGSUNTERLAGEN** Wir erstellen Pläne, Wohnflächen- und Raumberechnung, Baubeschreibung und Kostenaufteilung – und kommen mit zum Vorgespräch.
Leistungsphasen 5–7	5	**AUSFÜHRUNGSPLANUNG UND VERGABE** Nach der Bewilligung fordern wir mindestens drei Unternehmen zum Angebot auf und dokumentieren die Vergabe.
Leistungsphase 8	6	**BAULEITUNG** Wir halten Termine und Kosten im Blick und dokumentieren den Baufortschritt – auch per Drohne – für jede Teilrate (→ S. 9).
Leistungsphasen 8–9	7	**FERTIGSTELLUNG UND NACHWEIS** Wir bereiten die Fertigstellungsanzeige mit Bescheinigung der Bauleitung vor und liefern Bau- und Kostendaten für Ihren Verwendungsnachweis (→ S. 19).



1 Grundlagen · **2** Vorplanung · **3** Entwurf · **4** Genehmigung · **5** Ausführungsplanung · **6** Vorbereitung der Vergabe · **7** Mitwirkung bei der Vergabe · **8** Objektüberwachung · **9** Objektbetreuung

SCHLÜSSELFERTIG

Über die PGN Projektgesellschaft Nord GmbH bauen wir auch schlüsselfertig als Generalübernehmer. Förderfähig ist das, wenn Sie mindestens drei Unternehmen zum Angebot auffordern, erst nach der Bewilligung beauftragen und die Gesellschaft vorab schriftlich der Prüfung von Kalkulation, Nachunternehmervergabe und Abrechnung zustimmt.

FÜR KOMMUNEN

Unsere Stadtplanung erarbeitet Bebauungspläne. Legt die Gemeinde darin geförderte Mietwohnungen fest, gilt für diese Wohnungen der Bedarf als gegeben (→ S. 18).

UNTERLAGEN, KONTAKTE UND VERFAHRENSDETAILS

UNTERLAGEN BEREITLEGEN (AUSZUG)

- ☐ **Antrag:** Vordruck **1011** (**2.1**–**2.4**) · **1011a** + **1012** je Wohnung (**2.5**) · **1011b** (**2.6**)
- ☐ **Natürliche Personen**, auch Gesellschafterinnen und Gesellschafter: Selbstauskunft (Vordruck **3076**), SCHUFA-Auskunft, Identitätsfeststellung nach Geldwäschegesetz
- ☐ **Unternehmen:** Jahresabschlüsse (zwei Jahre), BWA (höchstens drei Monate alt), Handels- und Transparenzregisterauszug, Ertrags-, Finanz- und Liquiditätsplanung (→ S. 11)
- ☐ Grundbuchauszug, Lageplan, Bauzeichnungen, Baubeschreibung (Vordruck **1021**)
- ☐ Wohnflächenberechnung (WoFlV), umbauter Raum (DIN 277), Kosten-Finanzierungsaufteilung
- ☐ **Bei 2.3:** Energiebedarfsausweis mit Ausgangsklasse

VERFAHRENSDETAILS UND SONDERFÄLLE

AUSNAHMEN ZUM GRUNDCHECK

zu S. 4

Wer noch? Auch rechtsfähige Baugemeinschaften; beim Ersterwerb die Käuferseite.

Kein Mehrfamilienhaus? Gemeinschaftliche Wohnformen, im Einzelfall auch Reihen- oder Doppelhäuser. In **2.1**, **2.2** und **2.4**: je neuem Gebäude mindestens zwei gebundene Wohnungen.

Grundstück und Eigenmittel? Erbbaurecht mit mindestens 60 Jahren Restlaufzeit. Eigenleistung zählt bis zur Hälfte der Eigenmittel.

FINANZIERUNG UND SICHERHEITEN

zu S. 9

Sicherheiten? Grundschuld direkt hinter den Kapitalmarktmitteln; vorrangig nur übliche erststellige Darlehen mit mindestens 1 % Tilgung plus ersparter Zinsen, ohne Revalutierung. Je nach Bonität weitere Sicherheiten, etwa eine Bürgschaft – bei reinen Objektgesellschaften immer.

Tilgung später? Bei vorübergehendem Fehlbetrag kann die NBank den Beginn um bis zu fünf Jahre verschieben.

Vorzeitig ganz zurückzahlen? Die Bindung endet nach Ablauf des zehnten folgenden Kalenderjahres – frühestens 20 Jahre nach Bindungsbeginn, spätestens zum regulären Ende.

BEGINN, VERGABE, ANZEIGEN

zu S. 19

Vorzeitig beginnen? Nur nach Zulassung durch die NBank, beantragt frühestens mit dem Förderantrag – auf eigenes Risiko.

Vergabe? Mindestens drei Unternehmen zum Angebot auffordern, Verfahren und Ergebnis dokumentieren; Direktauftrag bis 25.000 € netto. Kommunen: zusätzlich Vergaberecht.

Anzeigen? Baubeginn erst anzeigen, wenn er erfolgt ist – für Unternehmen subventionserheblich. Beim Ersterwerb keine Baubeginn- und Fertigstellungsanzeige. Bauschild mit Förderhinweis.

HIER BEGINNT IHR ANTRAG

Wohnraumförderstelle am Bauort

Landkreis, Stadt oder Gemeinde: Vorabklärung, Formulare, Antrag

FÖRDERBERATUNG

NBank-Förderberatung Wohnraumförderung

0511 30031-9333

Mo–Fr 08:00–17:00 Uhr · wohnraumfoerderung@nbank.de · fünf Beratungsstellen im Land

IMMER AKTUELL

nbank.de

Förderstellen-Verzeichnis, Bemessungsgrenzen, Bedarfskarte, Vordrucke, Arbeitshilfen, Entgeltkatalog, Bauschild-Vorgaben

PLANUNG UND UNTERLAGEN

PGN

(+49) 4261 9293-0

Wir stellen die Antragsunterlagen mit Ihnen zusammen (→ S. 20) · info@pgn-architekten.de

IHRE GENERALPLANER AUS DEM NORDEN. *SEIT 1981.*

Von Rotenburg (Wümme) aus planen wir private, gewerbliche und kommunale Bauprojekte in ganz Norddeutschland – Architektur, Stadtplanung und Ingenieurwesen unter einem Dach.


ALLES AUS EINEM HAUS

Wir arbeiten für Wohnungsunternehmen und Wohnungsbaugenossenschaften, Investorinnen und Investoren, öffentliche Bauträger und Kommunen. Generalplanung, Architektur, Tragwerksplanung, Haustechnik sowie Stadt- und Landschaftsplanung greifen bei uns ineinander – in allen Leistungsphasen. Im Projektcontrolling planen wir mit der Finanzierung im Hinterkopf. Über die **PGN Projektgesellschaft Nord GmbH** entwickeln wir Projekte und bauen als Generalübernehmer auch schlüsselfertig. 3D-Druck und AR machen Entwürfe greifbar.

FÜR SIE DENKEN WIR AN:

- **VERANTWORTUNG.**
- **KOSTENSICHERHEIT.**
- **INNOVATION.**
- **VERTRAUEN.**

WOHNUNGSBAU-REFERENZEN

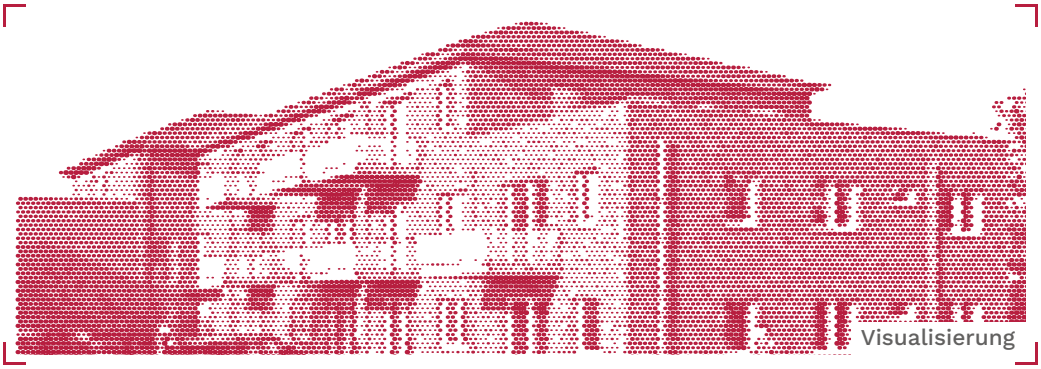

Visualisierung

MIT FÖRDERUNG DER NBANK

19 barrierefreie Wohnungen

BRAUERSTRASSE

Rotenburg (Wümme)

Neubau mit Aufzug, ca. 50–61 m², Luft-Wasser-Wärmepumpe, PV



Visualisierung

29 Wohnungen

PORSTWEG

Rotenburg (Wümme)
Wohnungsbau-Genossenschaft Rotenburg (Wümme) eG

drei Wohnhäuser, 50–95 m², Gemeinschaftsraum



Visualisierung

15 barrierefreie Wohnungen

DEHNENWEG

Hohenhameln
kwg Kreiswohnbaugesellschaft Hildesheim mbH

43–63 m², Aufzug



Visualisierung

40 barrierefreie Wohnungen

BURGSIEDLUNG

Stade
IDB mbH & Co. Stade-Altes Land KG

vier Stadthäuser, Aufzug in jedem Gebäude



Visualisierung

93 Mietwohnungen

WOHNEN IM LINDENHOF

Gifhorn

Quartier mit 15 Gebäuden, fertiggestellt Frühjahr 2018

Weitere Projekte: → **pgn-architekten.de**

IMPRESSUM UND HINWEISE

Die Investitions- und Förderbank Niedersachsen – NBank bewilligt die Förderung, die kommunale Wohnraumförderstelle am Bauort nimmt den Antrag entgegen. NBank und Land Niedersachsen sind nicht Herausgeber dieser Broschüre.

HERAUSGEBER	**Planungsgemeinschaft Nord GmbH** Große Straße 49, 27356 Rotenburg (Wümme)
KONTAKT	Telefon (+49) 4261 9293-0 · Telefax (+49) 4261 9293-90 info@pgn-architekten.de · www.pgn-architekten.de
GESCHÄFTSFÜHRUNG	Norbert Behrens, Stephan Müller, Nils Neumann, Matthias Mock
REGISTERGERICHT	Amtsgericht Walsrode, HRB 70348
UST-IDNR.	DE 116 324 794
VERANTWORTLICH FÜR DEN INHALT	[PGN: Name bestätigen]

HINWEIS

Alle Angaben ohne Gewähr, Stand 21.10.2026. Maßgeblich sind die RL Mietwohnraum 2026 und die Förderentscheidung der NBank. Fördersätze und Beträge sind Höchstwerte; die NBank prüft jede Förderung auf Überkompensation (EU-Beihilferecht). Modellrechnungen sind fiktive Beispiele, keine Förderzusage.

RECHTSGRUNDLAGE


RL Mietwohnraum 2026, Runderlass des Niedersächsischen Ministeriums für Wirtschaft, Verkehr und Bauen vom 25.06.2026 (Nds. MBl. 2026 Nr. 319), gültig vom 01.07.2026 bis 31.12.2031; ergänzend Niedersächsisches Wohnraum- und Wohnquartierfördergesetz (NWoFG) mit Durchführungsverordnung (DVO-NWoFG) und Wohngeldverordnung (WoGV, Mietenstufen).

QUELLEN

Zitate: Grant Hendrik Tonne und Michael Kiesewetter, Pressemitteilung MW vom 03.07.2026 (→ S. 2, 6). **Marktzahlen:** NBank-Wohnungsmarktbericht 2025 (→ S. 3, 7); NBank-Pressemitteilung zur Wohnungsmarktbeobachtung vom 05.12.2025 (→ S. 2); Landesregierung, Pressemitteilung vom 25.11.2025 (→ S. 18); NBank-Landkarte Wohnraumförderung, abgerufen am 21.10.2026 (→ S. 18).

Bildnachweis: Visualisierungen S. 22: [PGN: Urheber bestätigen] · Titelzeichnung, Diagramme und Illustrationen: Planungsgemeinschaft Nord GmbH

Druck: [Platzhalter] · **Stand:** 21.10.2026

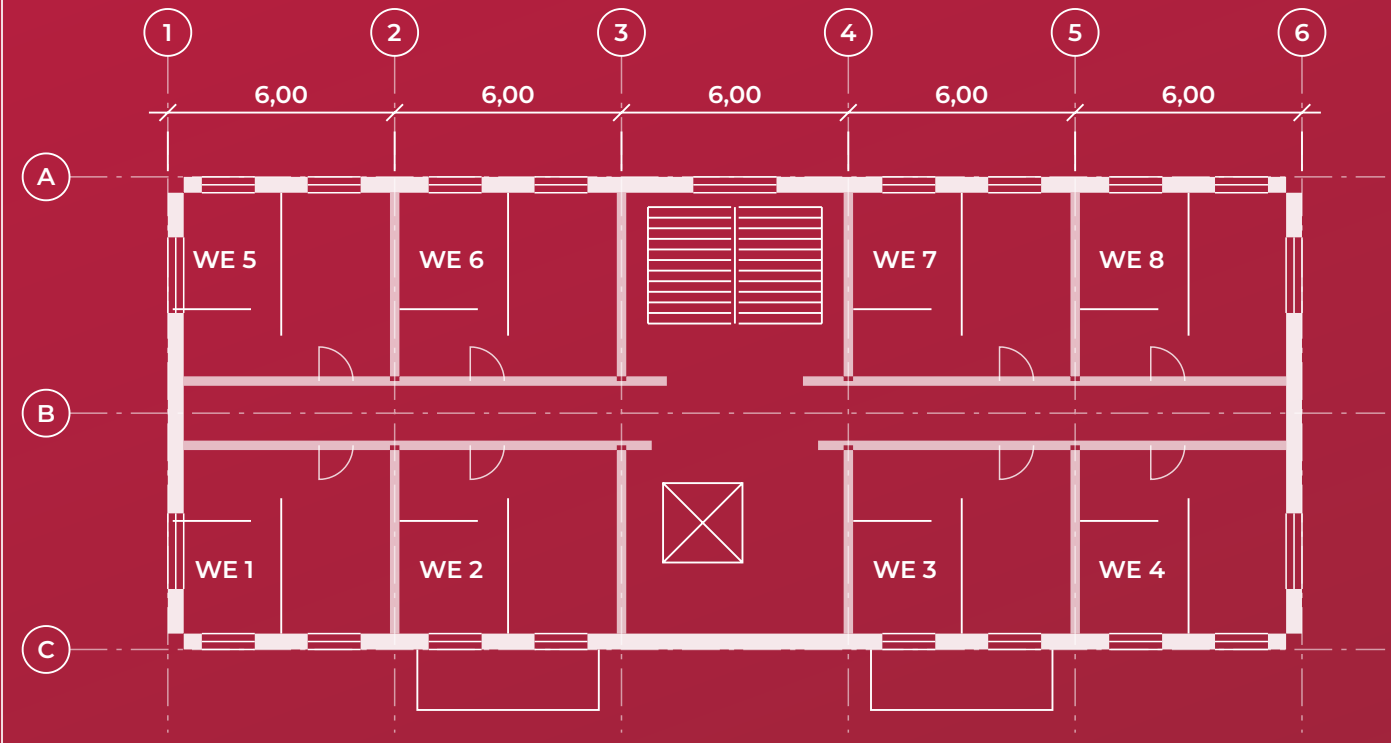

REGELGESCHOSS · M 1:200

AUS IHRER GUTEN IDEE –

MACHEN WIR DEN *BESTEN PLAN.*

Sprechen Sie uns an: Wir prüfen mit Ihnen, welcher Programmteil zu Ihrem Projekt passt und wie es sich rechnet.

PLANUNGSGEMEINSCHAFT NORD GMBH
Große Straße 49 · 27356 Rotenburg (Wümme)

Telefon
(+49) 4261 9293-0

E-Mail
info@pgn-architekten.de

Web
www.pgn-architekten.de

www.pgn-architekten.de

PGN ARCHITEKTEN STADTPLANER INGENIEURE

Projekt
Mietwohnraumförderung Niedersachsen 2026

Stand
21.10.2026

Blatt
U4